


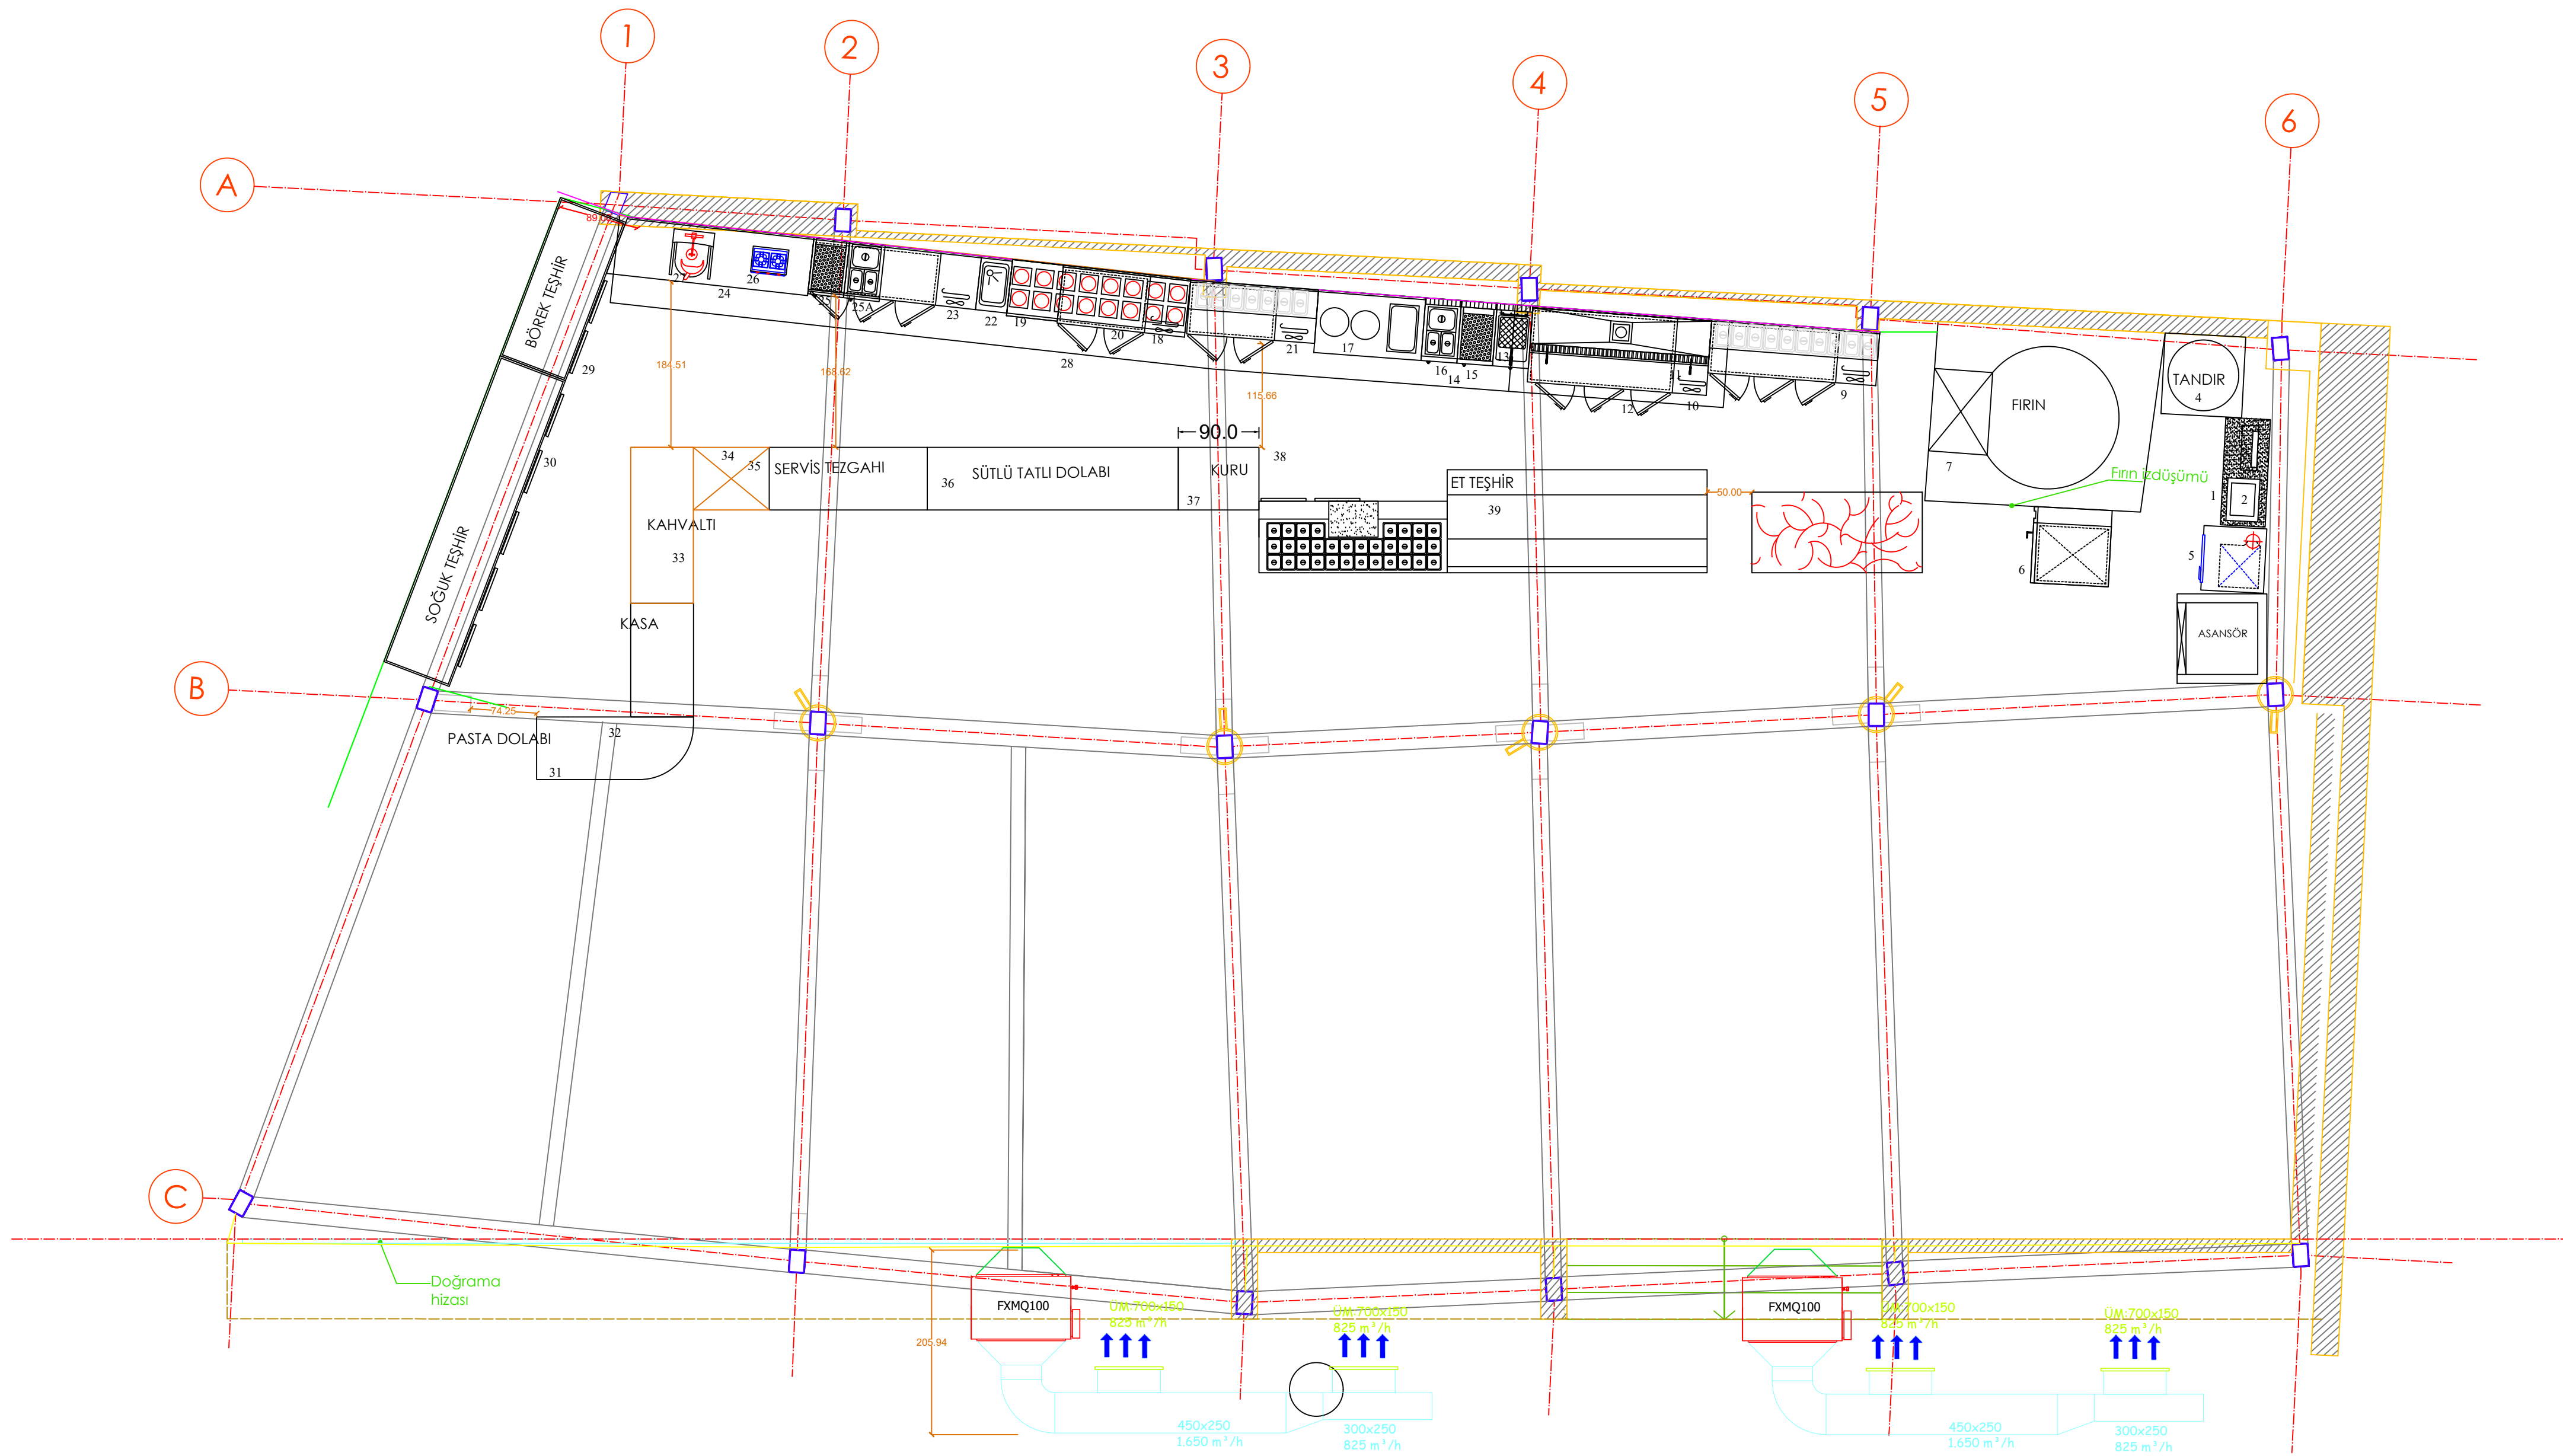

P.NO	ÜRÜN ADI	ÖLÇÜ	AD.
BÖLÜM			
1	MERMER TABLALI ÇALIŞMA TEZGAHI	120*50*85	1
2	VAKUM MAKİNASI, LİPOVAK MV20	-	1
3	HAMUR AÇMA MAKİNASI	MEVCUT	1
4	TANDIR FIRINI	MEVCUT	1
5	DEPO TİPİ BUZDOLABI (40*60 TEPŞİ RAFLI)	72*80*205	1
6	FIRIN	MEVCUT	1
7	TAŞ FIRIN	MEVCUT	1
8	MERMER TABLALI ÇALIŞMA TEZGAHI	MEVCUT	1
9	MAKE-UP ÜNİTESİ, 3 KAPILI	MEVCUT	1
10	TEZGAH TİPİ BUZDOLABI	200*85*85	1
11	KÖMÜRLÜ İZGARA (ARKA DUVAR TUĞLA KAPLI)	180*70*30	1
12	DAVLUMBAZ, DUVAR TİPİ, FİLTRELİ	200*95*45	1
13	FİRİTÖZ, FRYMASTER	MEVCUT	1
14	PATATES DİNLENDİRME, ELK.	40*70*29	1
15	SOS BAINMARIE, ELK.	40*70*29	1
16	ÇALIŞMA TEZGAHI	80*65*56	1
17	ÇORBALIK TEZGAHI	MEVCUT	1
18	SETALTI BUZDOLABI, 2 KAPILI	MEVCUT	1
19	SETALTI ÇALIŞMA TEZGAHI	MEVCUT	1
20	YUMURTA OCAĞI	MEVCUT	1
21	MAKE-UP ÜNİTESİ, 2 KAPILI	MEVCUT	1
22	TEK EVYELİ ÇALIŞMA TEZGAHI	MEVCUT	1
23	TEZGAH TİPİ BUZDOLABI, 3 KAPILI	MEVCUT	1
24	ÇALIŞMA TEZGAHI	MEVCUT	1
25	PATATES DİNLENDİRME, ELK.	40*65*20	1
25A	SOS BAINMARIE	40*65*20	1
26	İSKENDER OCAĞI	MEVCUT	1
27	DÖNER OCAĞI	MEVCUT	1
28	DAVLUMBAZ, DUVAR TİPİ, FİLTRELİ	1020*95*45	1
29	BÖREK TEŞHİR DOLABI	MEVCUT	1
30	SÖĞÜK TEŞHİR DOLABI, MOTORU DIŞARIDA	MEVCUT	1
31	PASTA DOLABI	170*70*110	1
32	KASA TEZGAHI	MOBİLYA M.T.	1
33	KAHVALTI DOLABI	MEVCUT	1
34	SERVİS TEZGAHI	MEVCUT	1
35	SERVİS TEZGAHI	175*70*85	1
36	SÜTLÜ TATLI DOLABI, MOTORU DIŞARIDA	MEVCUT	1
37	KURABIYE DOLABI	MEVCUT	1
38	SALATA DOLABI, ÇEKMECELİ, MOTORU DIŞARIDA	210*80*125	1
39	ET TEŞHİR DOLABI	MEVCUT	1