
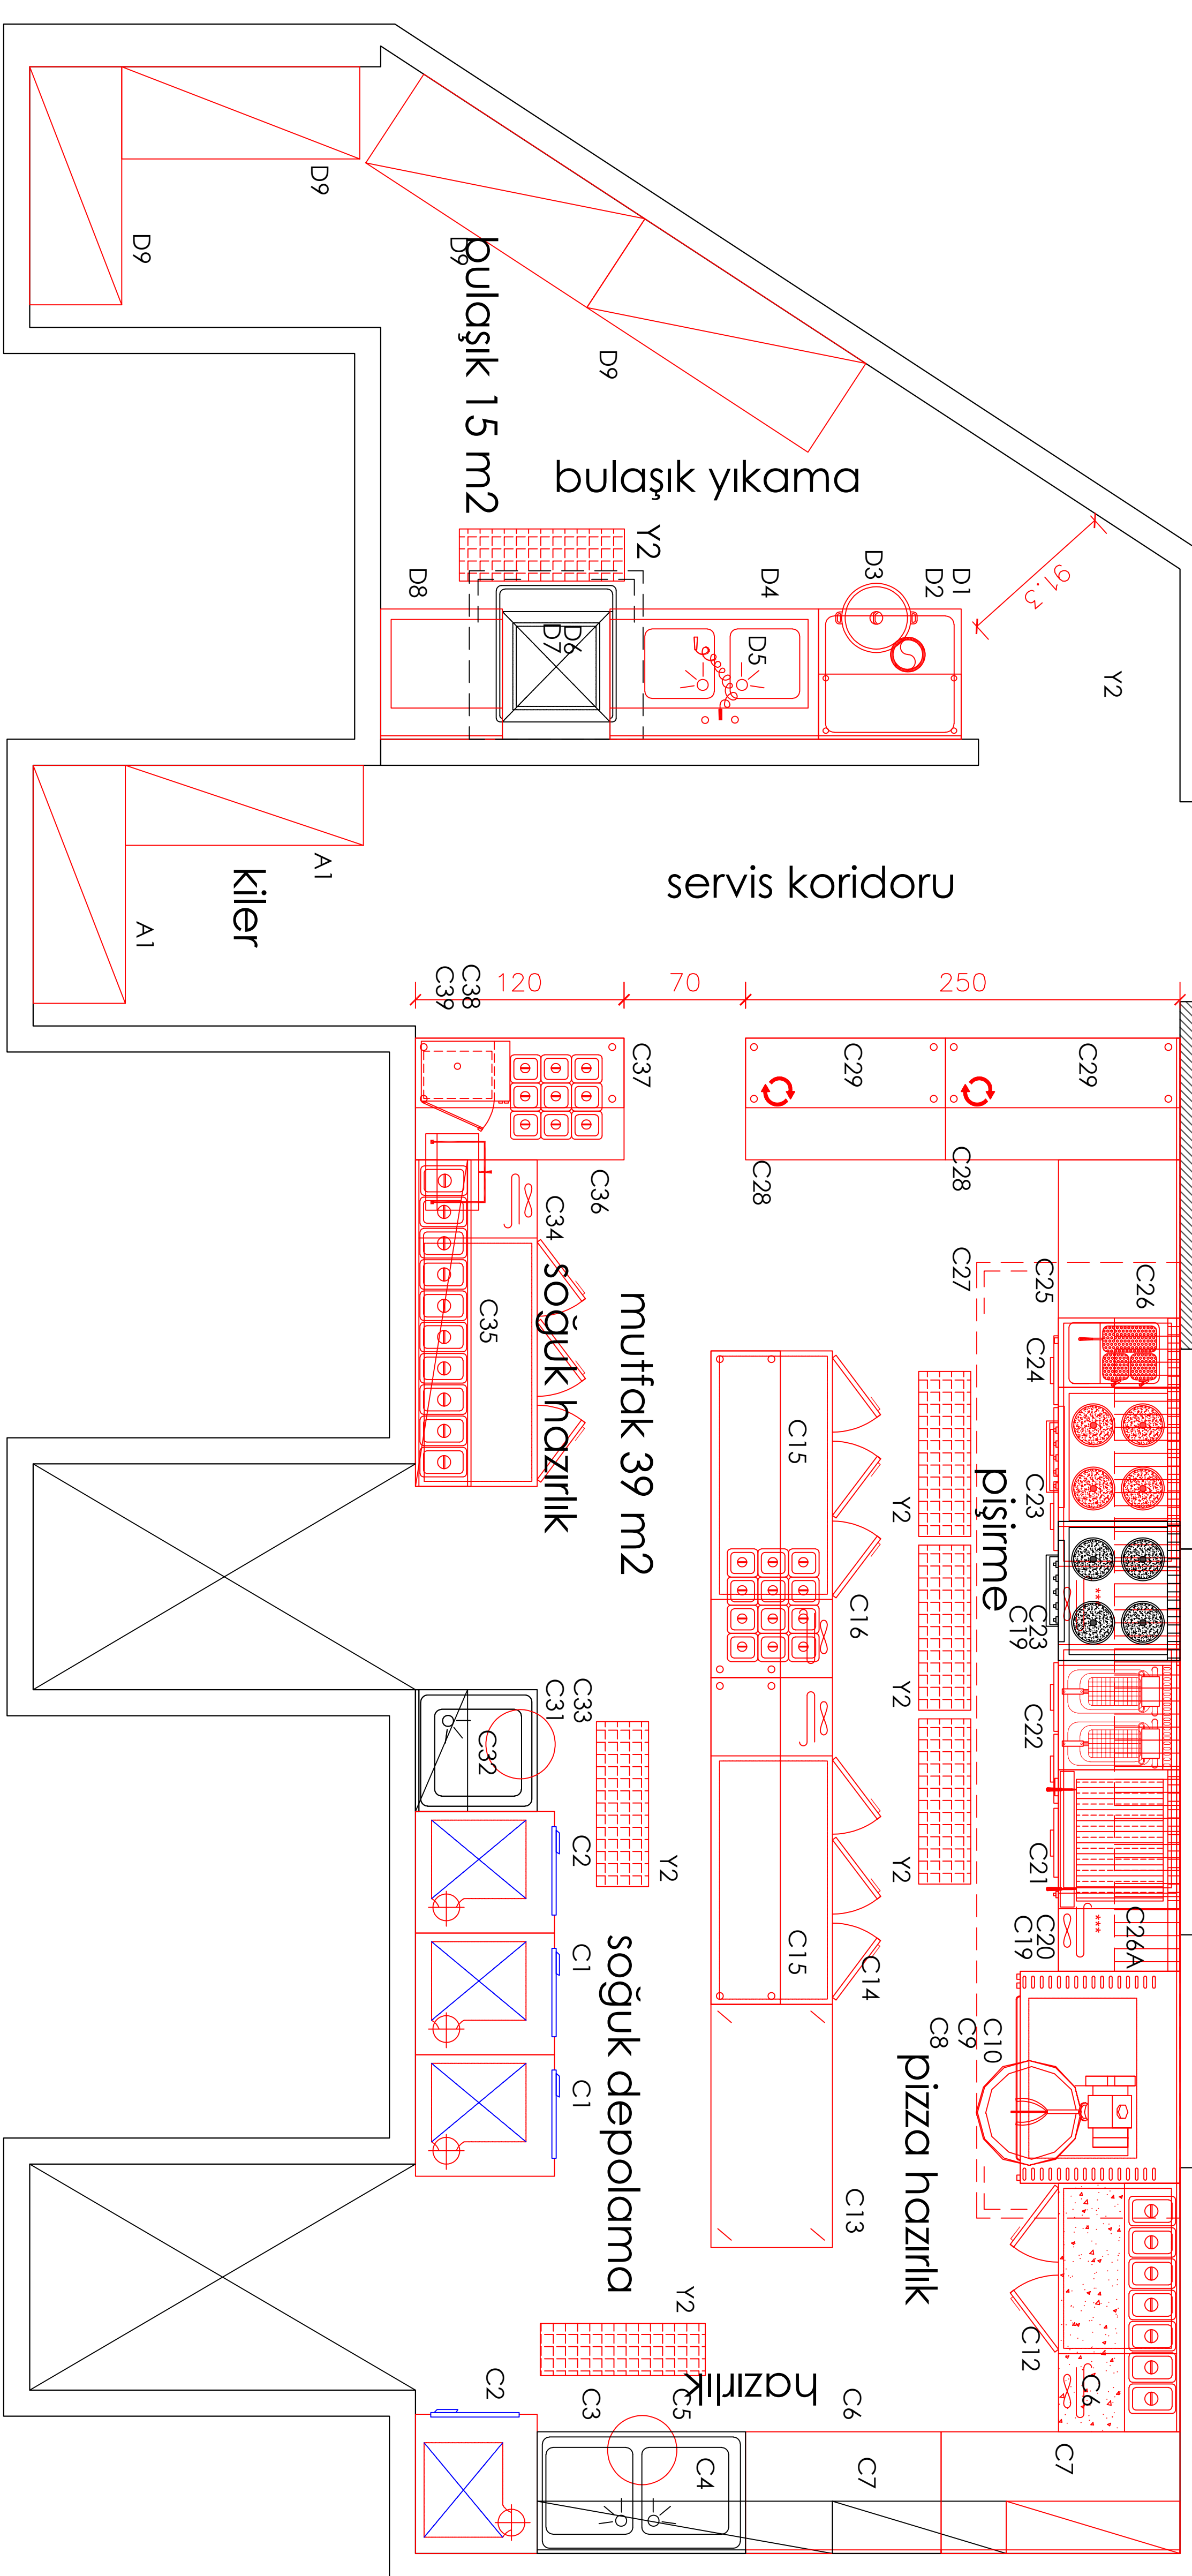
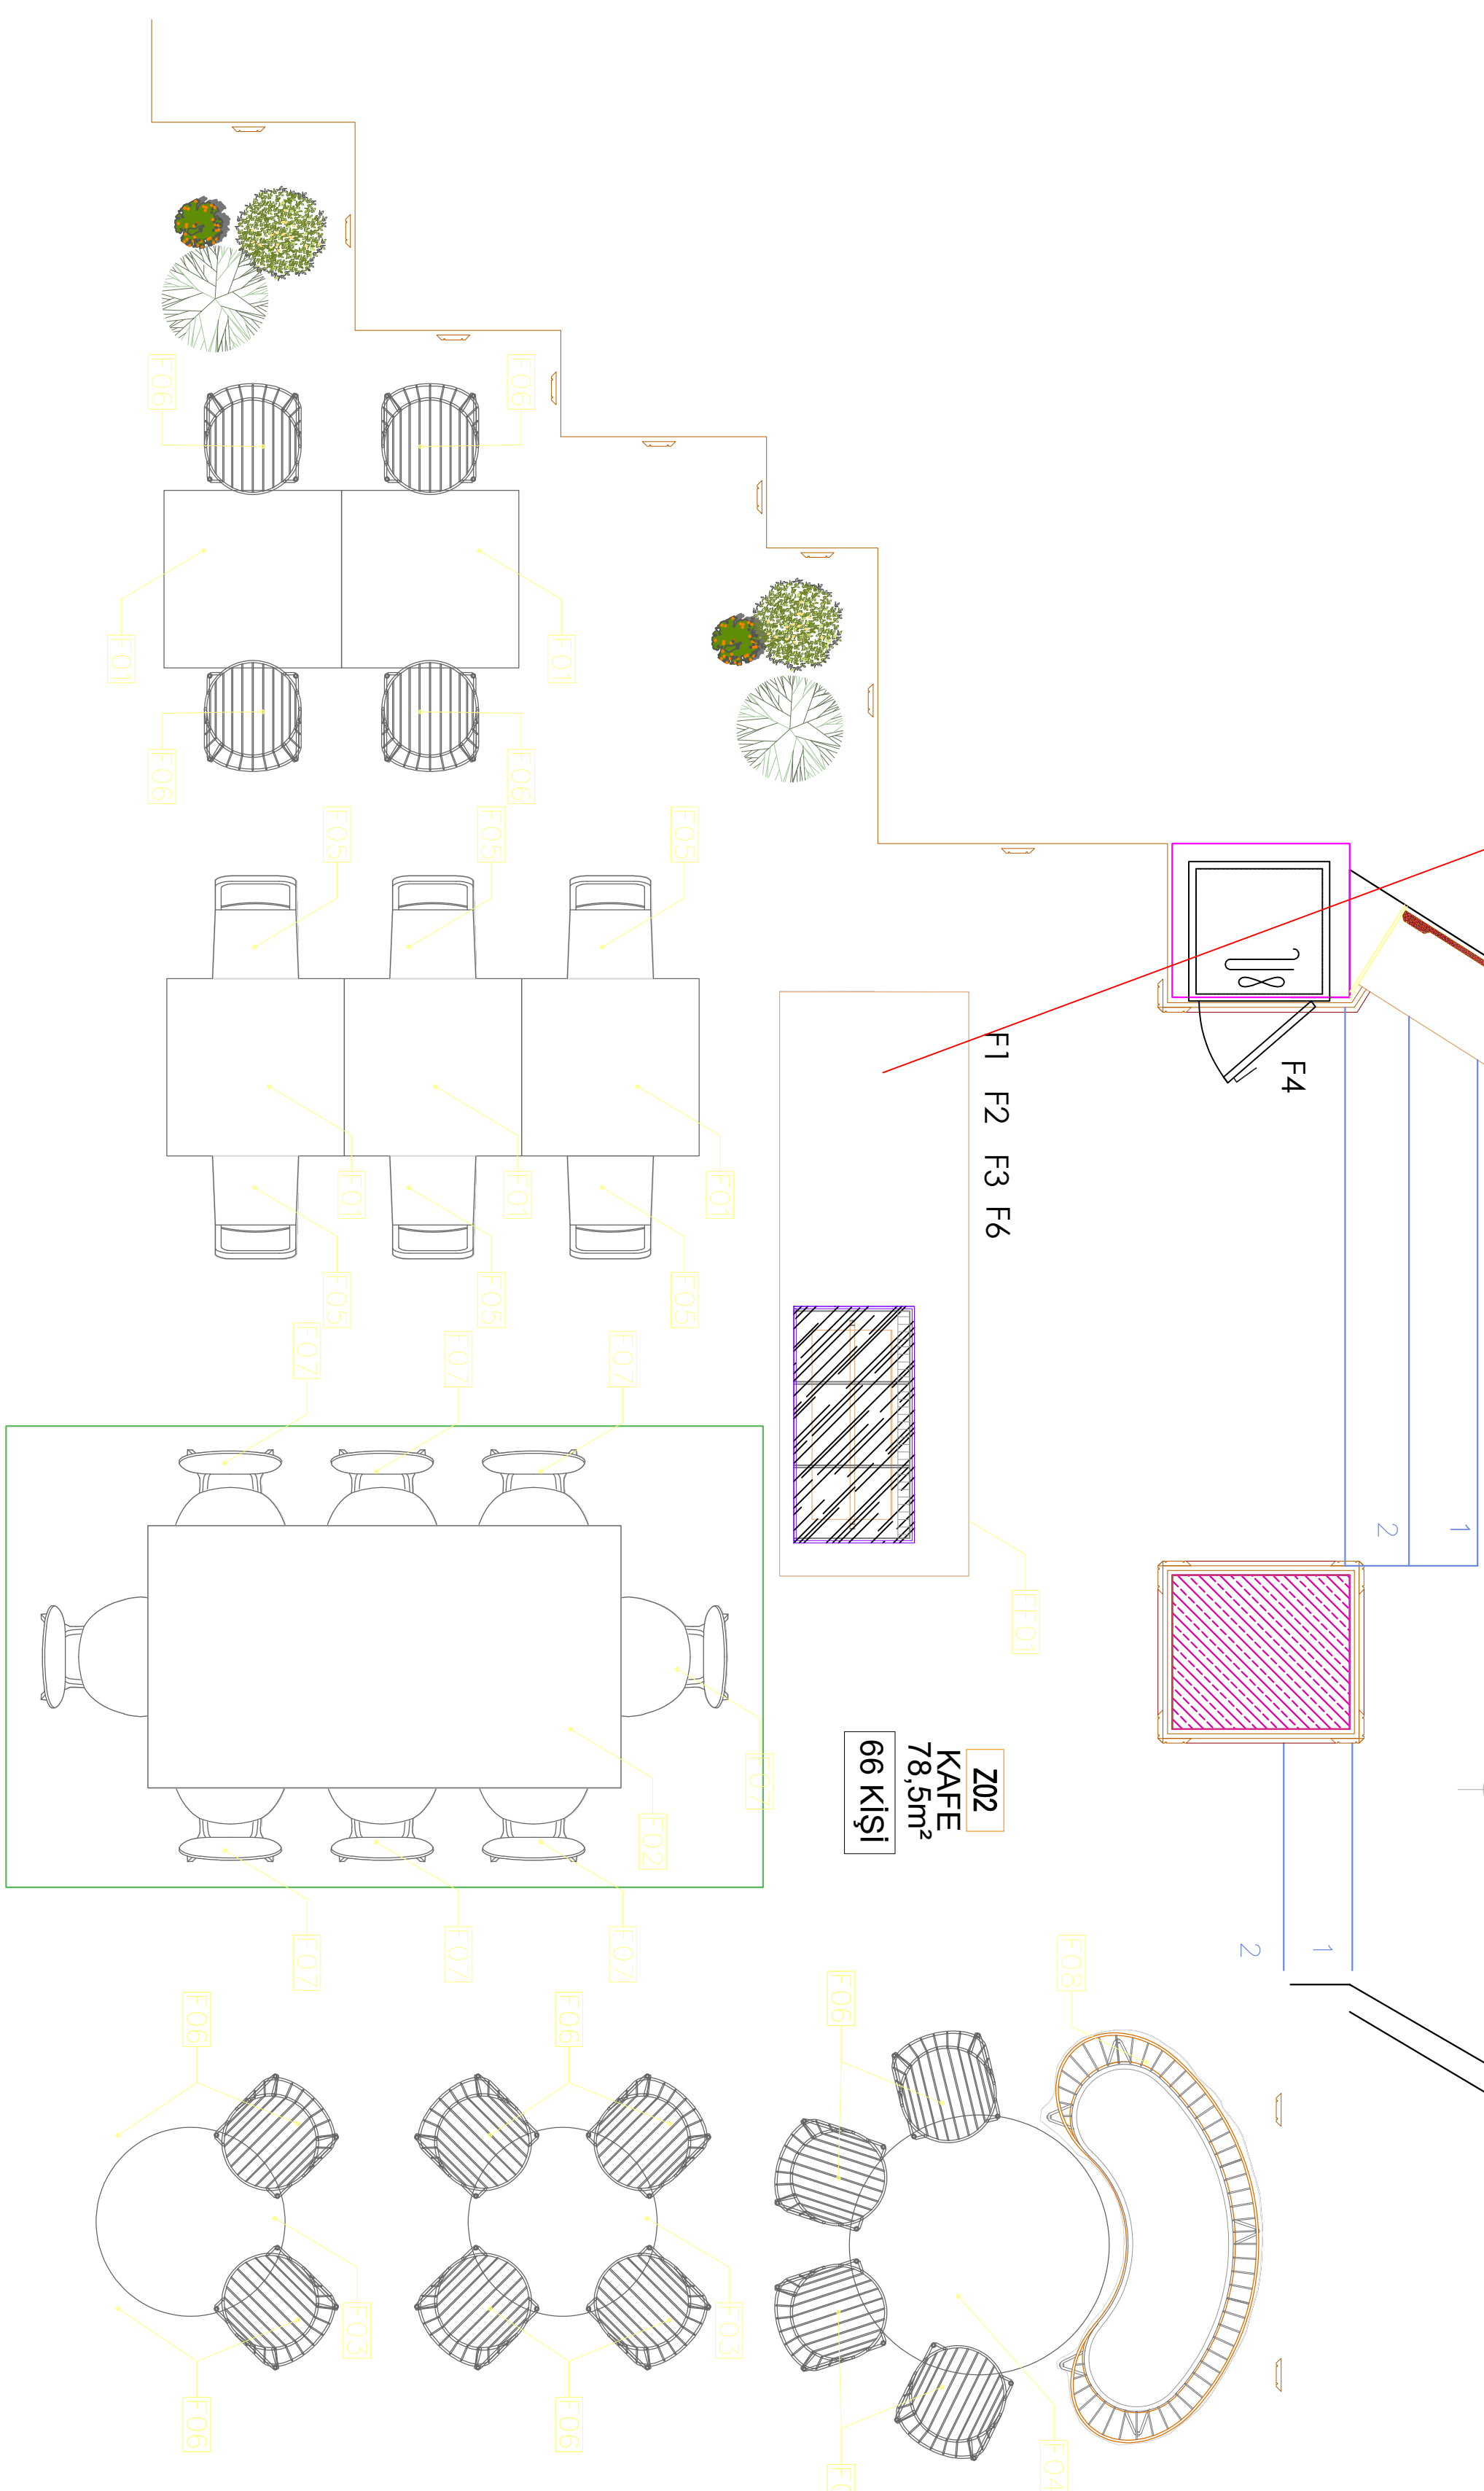
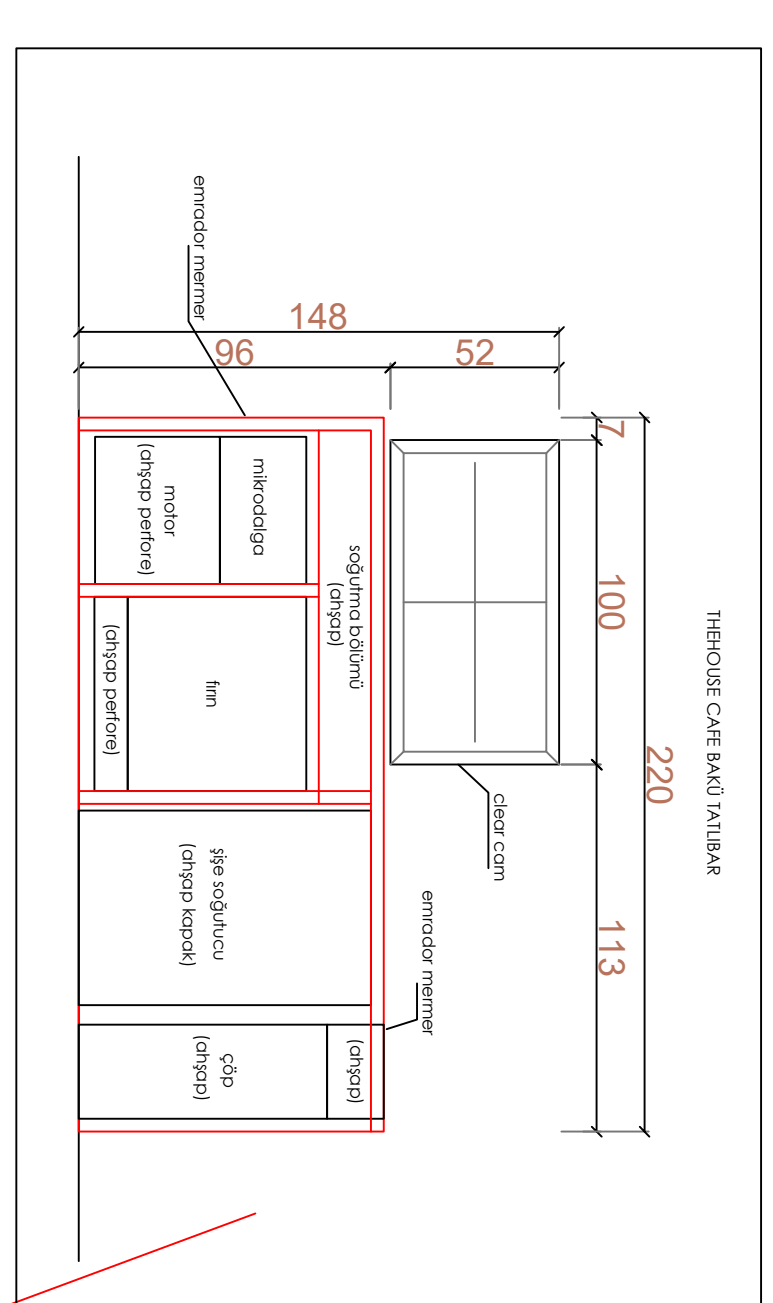


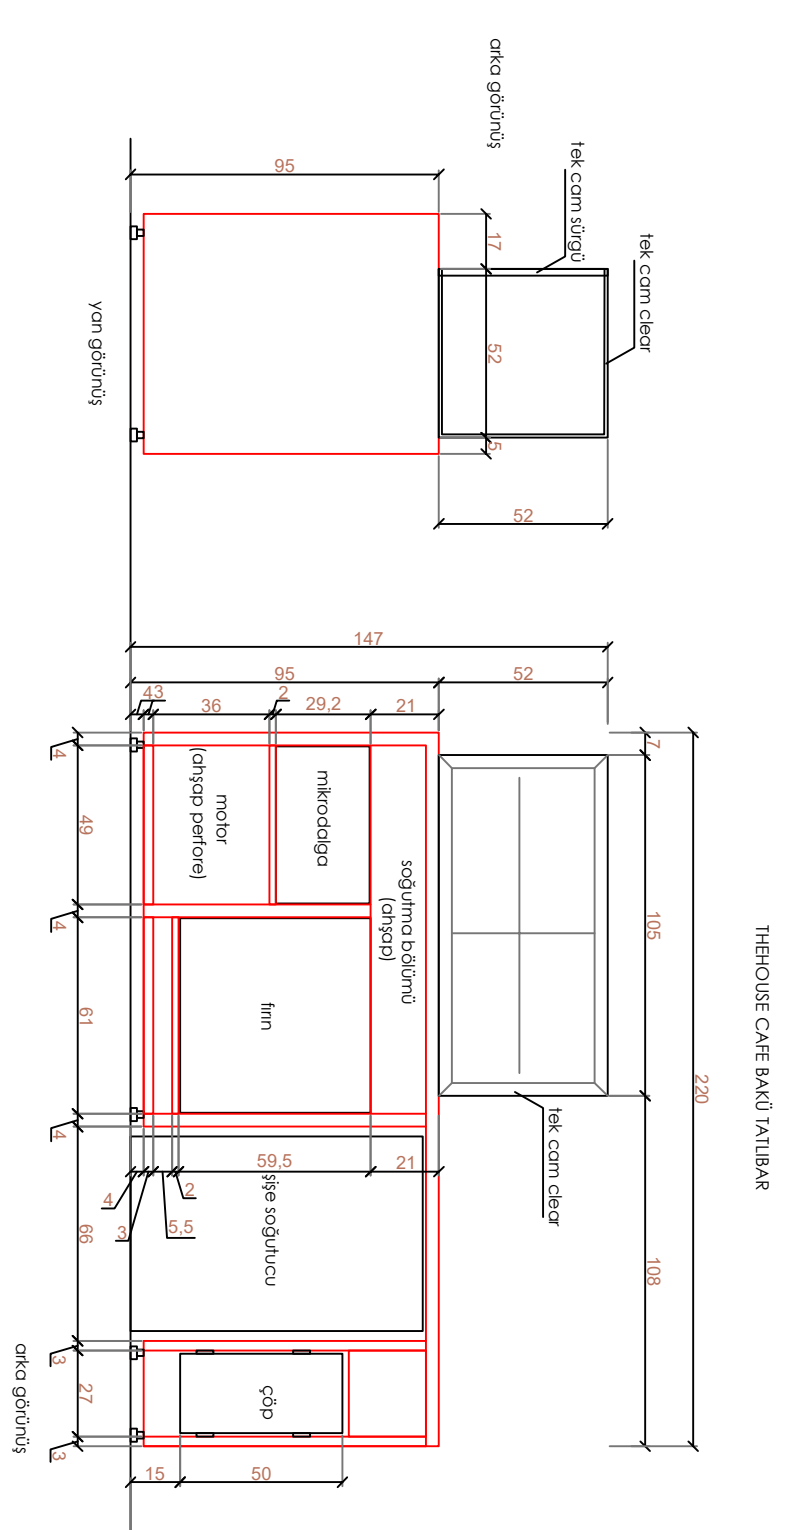

MUTFAK PLANI

YERLEŞİM PLANI

BAR PLANI

THEHOUSE CAFE BAKÜ BAR VE MUTFAK PROJESİ

DESIGNED BY/DIZAYIN EDEN	ADDEM AKPINAR	2017-044-2
DRAWN BY/ÇİZEN	ÇAĞLA YILDIRIM	
CHECKED BY/KONTROL EDEN	ADDEM AKPINAR	
DATE /TARİH	09.06.2017	
REVISION DATE	SCALE/ÖLÇEK	
REVISION NO	SCALE/ÖLÇEK	
00.00.0000	1/50	
THIS DRAWING REMAINS THE PROPERTY OF DORUK ENDÜSTRİYEL MUTFAK ŞİRKETİ AND MAY ONLY BE COPIED COMPLETELY OR PARTLY OR ISSUED TO THIRD PARTY WITH OUR PRIOR CONSENT.		
BU RESİM DORUK ENDÜSTRİYEL MUTFAK ŞİRKETİNİN MALİ OLUP YAZILI MÜSAADE OLUNMADIÇA KİMSİN VEYA TAMAMEN KOPYA EDİLMEMİZE VE ÖÇÜNCÜ SAHİBİ ARAYA VERİLMEMİZE.		
DORUK MİRKETZ MAH. DUMLUÖFİNAR CAD NO: 6/B KAĞITHANE/İSTANBUL p: 0212 909 4312 m: 0554 237 8532 w: info@skutuk.com.tr e: info@skutuk.com.tr		