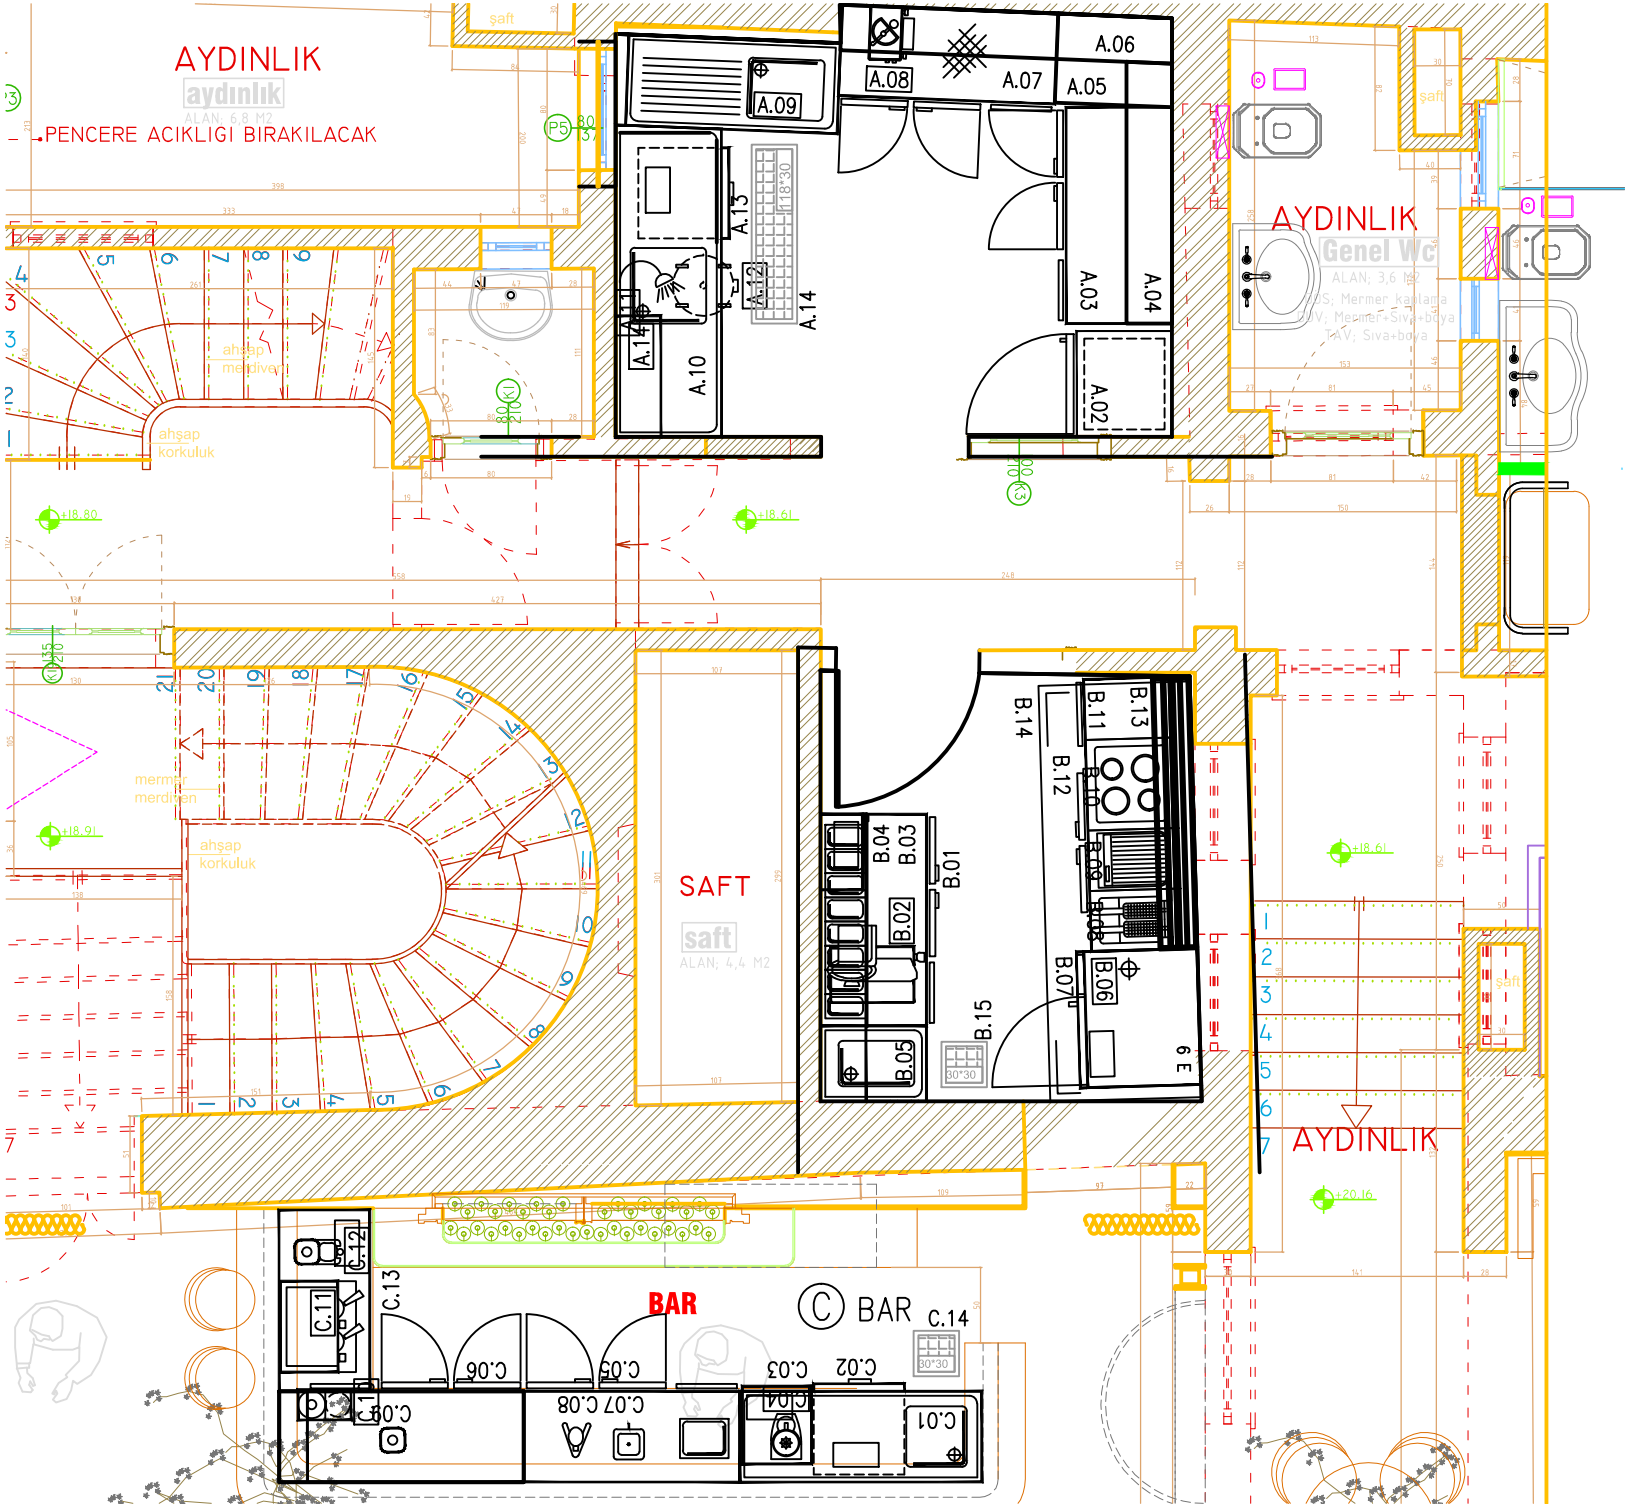
AYDINLIK
aydınlık
ALAN; 6,8 M2
PENCERE ACIKLIGI BIRAKILACAK
şaft
A.09
A.08
A.07
A.06
A.05
A.13
A.12
A.14
A.11
A.10
A.03
A.04
A.02
AYDINLIK
Genel Wc
ALAN; 3,6 M2
ahşap merdiven
ahşap korkuluk
+18.80
+18.61
mermer merdiven
ahşap korkuluk
+18.91
SAFT
saft
ALAN; 4,4 M2
B.14
B.11
B.13
B.12
B.10
B.09
B.08
B.04
B.03
B.01
B.02
B.07
B.06
B.05
B.15
30*30
AYDINLIK
+18.61
+20.16
C.12
C.11
C.13
BAR
BAR
C.14
C.06
C.05
C.03
C.02
C.04
C.07 C.08
C.09
C.01
30*30