


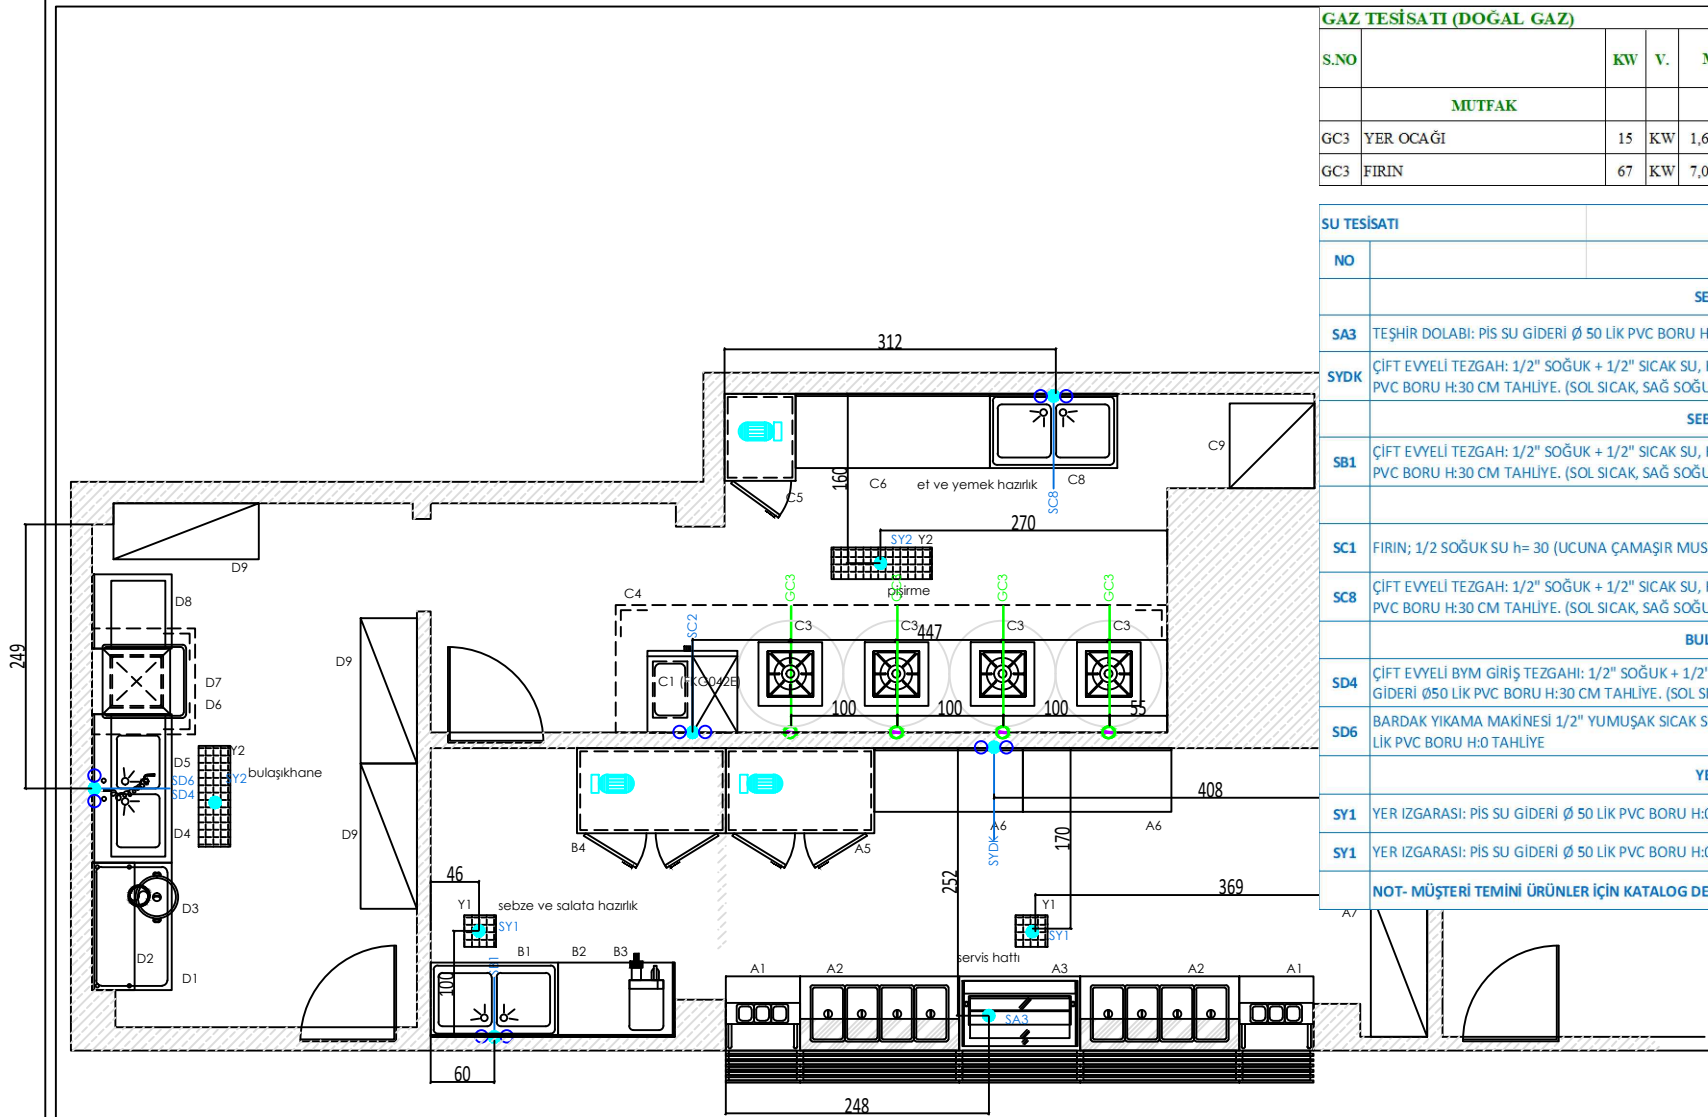

GAZ TESİSATI (DOĞAL GAZ)

S.NO		KW	V.	M ² /SA.	AÇIKLAMA	AD.	TOP LAM KW.
MUTFAK							
GC3	YER OCAĞI	15	KW	1,6	M ² /SA H: 130 CM KÜRESEL VANA (21mbar)	4	6,3
GC3	FIRIN	67	KW	7,0	M ² /SA H: 20 CM KÜRESEL VANA (21mbar)	1	7,0

SU TESİSATI

NO		ADET
SERVİS HATTI		
SA3	TEŞHİR DOLABI: PİS SU GİDERİ Ø 50 LİK PVC BORU H:0 ZEMİNDE TAHLİYE	1
SYDK	ÇİFT EYELİ TEZGAH: 1/2" SOĞUK + 1/2" SICAK SU, H:45 cm (UCUNA 3/8" ARA MUSLUK), PİS SU GİDERİ Ø50 LİK PVC BORU H:30 CM TAHLİYE. (SOL SICAK, SAĞ SOĞUK SU OLMALIDIR)	1
SEBZE HAZIRLIK		
SB1	ÇİFT EYELİ TEZGAH: 1/2" SOĞUK + 1/2" SICAK SU, H:45 cm (UCUNA 3/8" ARA MUSLUK), PİS SU GİDERİ Ø50 LİK PVC BORU H:30 CM TAHLİYE. (SOL SICAK, SAĞ SOĞUK SU OLMALIDIR)	1
PIŞIRME		
SC1	FIRIN: 1/2 SOĞUK SU h= 30 (UCUNA ÇAMAŞIR MUSLUĞU); PİS SU GİDERİ Ø15 cm	1
SC8	ÇİFT EYELİ TEZGAH: 1/2" SOĞUK + 1/2" SICAK SU, H:45 cm (UCUNA 3/8" ARA MUSLUK), PİS SU GİDERİ Ø50 LİK PVC BORU H:30 CM TAHLİYE. (SOL SICAK, SAĞ SOĞUK SU OLMALIDIR)	1
BULAŞIK YIKAMA		
SD4	ÇİFT EYELİ BYM GİRİŞ TEZGAHI: 1/2" SOĞUK + 1/2" SICAK SU, H:45 cm (UCUNA 3/8" ARA MUSLUK), PİS SU GİDERİ Ø50 LİK PVC BORU H:30 CM TAHLİYE. (SOL SICAK, SAĞ SOĞUK SU OLMALIDIR)	1
SD6	BARDAK YIKAMA MAKİNESİ 1/2" YUMUŞAK SICAK SU H:10 CM (UCUNA ÇAMAŞIR MUSLUĞU), PİS SU GİDERİ Ø 50 LİK PVC BORU H:0 TAHLİYE	
YER IZGARASI		
SY1	YER IZGARASI: PİS SU GİDERİ Ø 50 LİK PVC BORU H:0 ZEMİNDE TAHLİYE	2
SY1	YER IZGARASI: PİS SU GİDERİ Ø 50 LİK PVC BORU H:0 ZEMİNDE TAHLİYE	2
NOT- MÜŞTERİ TEMİNİ ÜRÜNLER İÇİN KATALOG DEĞERLERİNİ KONTROL EDİNİZ		

ÇAM KOLEJİ | KARTAL BAR VE MUTFAK PROJESİ

DESIGNED/ TASARIM	ADEM AKPINAR
DRAWN/ ÇİZEN	ADEM AKPINAR
CHECKED/ KONTROL	ADEM AKPINAR
DATE/ TARİH	1.5.2019

REV. DATE	REV. TARİHİ	SCALE	ÖLÇEK	1/50 (A3)
00.00.0000				



MALTEPE MAH. DAVUTPAŞA CAD. YILDIZ SOK. NO: 6/ A
DAVUTPAŞA/ ZEYİTBURNU/ İSTANBUL
p: 0212 909 4312
w: skturk.com.tr | e: info@skturk.com.tr

2019-078

THIS DRAWING REMAINS THE PROPERTY OF SKTÜRK ENDÜSTRİYEL MUTFAK SAN. VE TİC. LTD. ŞTİ. AND MAY ONLY BE COPIED COMPLETELY OR PARTLY OR ISSUED TO THIRD PARTY WITH OUR PRIOR CONSENT.
BU RESİM SKTÜRK ENDÜSTRİYEL MUTFAK SAN. VE TİC. LTD. ŞTİ.'NİN MALİ OLUP VAZİRLİĞİN OLMADIĞI KİSMEN VEYA TAMAMEN KOPYA EDİLEMEZ VE ÜÇÜNCÜ SAHİPLERİNE VERİLEMEZ.