


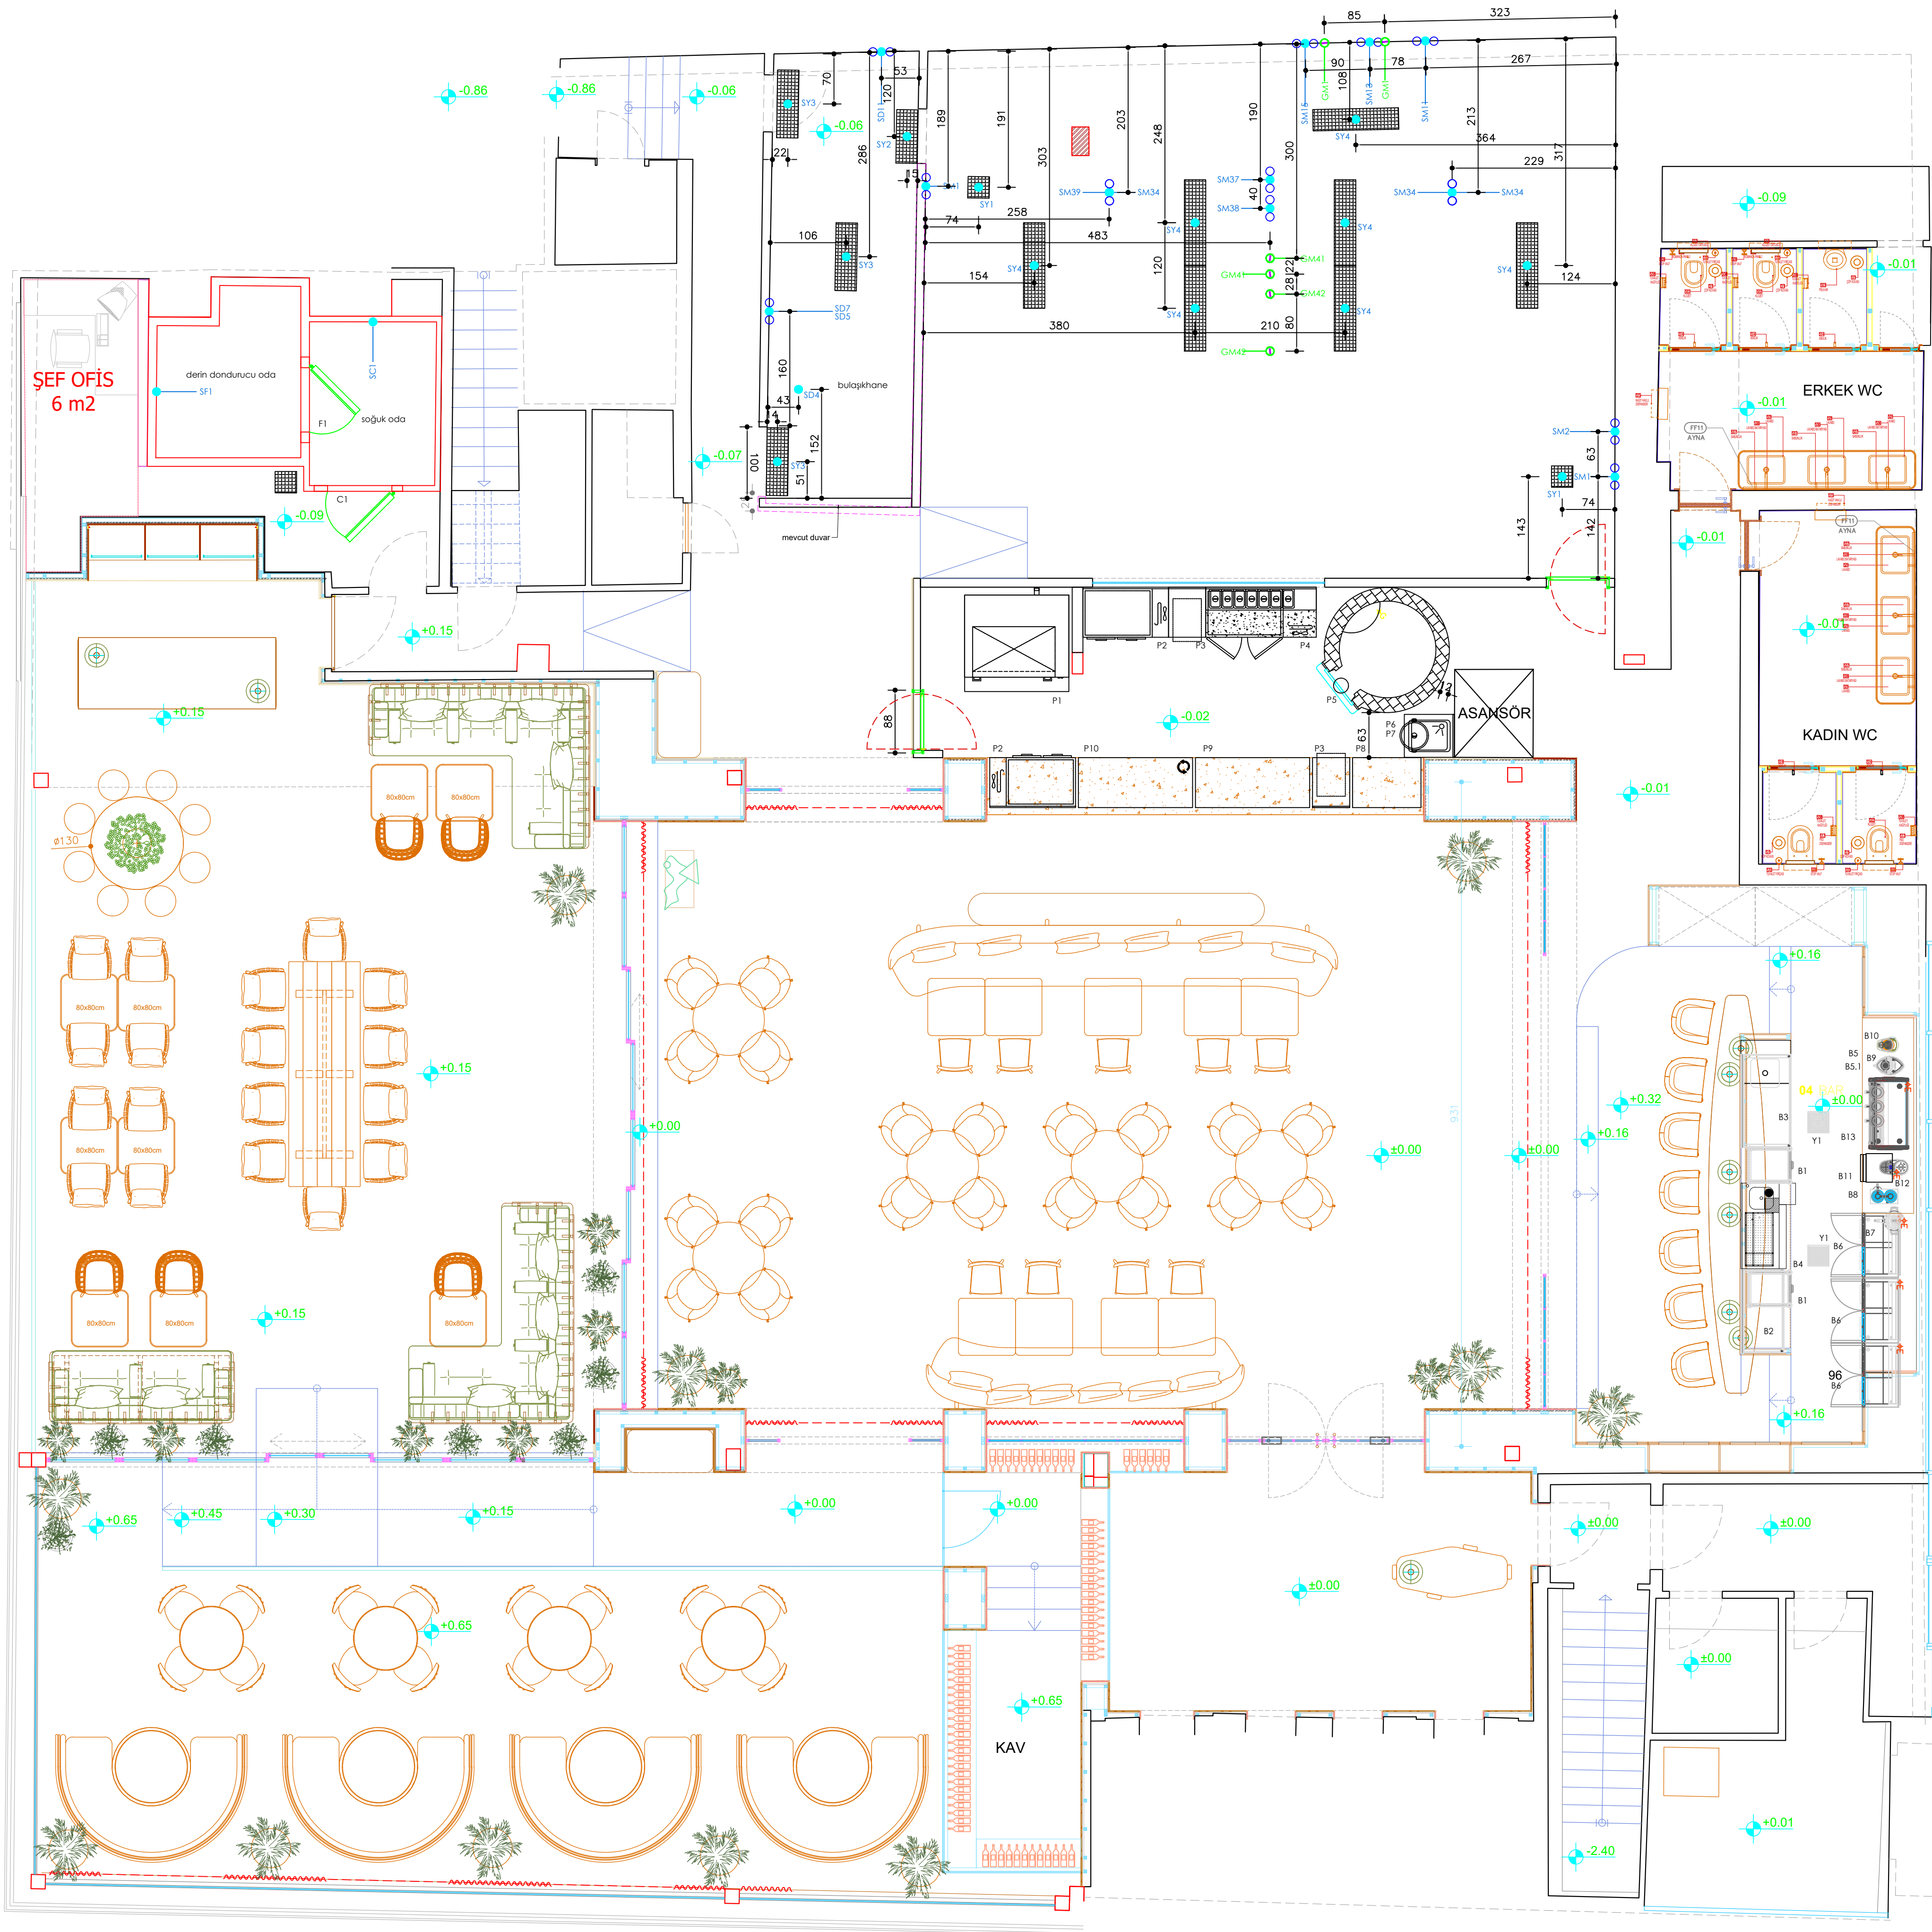

SU TESİSATI			
NO			ADET
HAZIRLIK			
SM1	DİZDEN KUMANDALI EL YIKAMA: 1/2" SOĞUK + 1/2" SICAK SU, H:45 cm (UCUNA 3/8" ARA MUSLUK), PİS SU GİDERİ Ø50 LİK PVC BORU H:30 CM TAHLİYE. (SOL SICAK, SAĞ SOĞUK SU OLMALIDIR)		2
SM2	BUZ MAKİNESİ ; 1/2" YUMUŞAK SOĞUK SU H:25 (ÇAMAŞIR MUSLUĞU) , PİS SU GİDERİ Ø 50 LİK PVC BORU H: 0 CM TAHLİYE		1
SM11	ELECTROLUX MULTISUM FIRIN: 3/4" SOĞUK SU GİRİŞİ (UCUNA 3/8" ARA MUSLUK) H: 60 CM. PİS SU GİDERİ Ø50 LİK PVC BORU H:30 CM TAHLİYE.		1
SM13	ZANUSSI FIRIN: 3/4" SOĞUK SU GİRİŞİ (UCUNA 3/8" ARA MUSLUK) H: 60 CM. PİS SU GİDERİ Ø50 LİK PVC BORU H:30 CM TAHLİYE.		1
SM15	ELECTROLUX FIRIN: 3/4" SOĞUK SU GİRİŞİ (UCUNA 3/8" ARA MUSLUK) H: 60 CM. PİS SU GİDERİ Ø50 LİK PVC BORU H:30 CM TAHLİYE.		1
SM29	TEK EYELİ TEZGAH: 1/2" SOĞUK + 1/2" SICAK SU, H:45 cm (UCUNA 3/8" ARA MUSLUK), PİS SU GİDERİ Ø50 LİK PVC BORU H:30 CM TAHLİYE. (SOL SICAK, SAĞ SOĞUK SU OLMALIDIR)		1
SM34	TEK EYELİ TEZGAH: 1/2" SOĞUK + 1/2" SICAK SU, H:45 cm (UCUNA 3/8" ARA MUSLUK), PİS SU GİDERİ Ø50 LİK PVC BORU H:30 CM TAHLİYE. (SOL SICAK, SAĞ SOĞUK SU OLMALIDIR)		5
S37	MAKARNA PİŞİRİCİ: 1/2" YUMUŞAK SICAK SU H:10 CM (UCUNA ÇAMAŞIR MUSLUĞU), PİS SU GİDERİ Ø 50 LİK PVC BORU H:0 TAHLİYE		1
S38	MAKARNA PİŞİRİCİ: 1/2" YUMUŞAK SICAK SU H:10 CM (UCUNA ÇAMAŞIR MUSLUĞU), PİS SU GİDERİ Ø 50 LİK PVC BORU H:0 TAHLİYE		1
SA1	ÇİFT EYELİ TEZGAH: 1/2" SOĞUK + 1/2" SICAK SU, H:45 cm (UCUNA 3/8" ARA MUSLUK), PİS SU GİDERİ Ø50 LİK PVC BORU H:30 CM TAHLİYE. (SOL SICAK, SAĞ SOĞUK SU OLMALIDIR)		1
KAZAN YIKAMA			
SB1	KAZAN YIKAMA EYİŞİ: 1/2" SOĞUK + 1/2" SICAK SU, H:30 cm (UCUNA 3/8" ARA MUSLUK), PİS SU GİDERİ Ø50 LİK PVC BORU H:15 CM TAHLİYE. (SOL SICAK, SAĞ SOĞUK SU OLMALIDIR)		1
BULAŞIK YIKAMA			
SD4	YER İZGARASI: PİS SU GİDERİ Ø 50 LİK PVC BORU H:0 ZEMİNDE TAHLİYE		1
SD5	ÇİFT EYELİ BYM GİRİŞ TEZGAHI: 1/2" SOĞUK + 1/2" SICAK SU, H:45 cm (UCUNA 3/8" ARA MUSLUK), PİS SU GİDERİ Ø50 LİK PVC BORU H:30 CM TAHLİYE. (SOL SICAK, SAĞ SOĞUK SU OLMALIDIR)		1
SD7	BULAŞIK YIKAMA MAKİNESİ 1/2" YUMUŞAK SICAK SU H:10 CM (UCUNA ÇAMAŞIR MUSLUĞU), PİS SU GİDERİ Ø 50 LİK PVC BORU H:0 TAHLİYE		1
YER İZGARASI			
SV1	YER İZGARASI: PİS SU GİDERİ Ø 50 LİK PVC BORU H:0 ZEMİNDE TAHLİYE		3
SV2	YER İZGARASI: PİS SU GİDERİ Ø 50 LİK PVC BORU H:0 ZEMİNDE TAHLİYE		1
SV3	YER İZGARASI: PİS SU GİDERİ Ø 50 LİK PVC BORU H:0 ZEMİNDE TAHLİYE		3
SV4	YER İZGARASI: PİS SU GİDERİ Ø 50 LİK PVC BORU H:0 ZEMİNDE TAHLİYE		7
NOT- MÜŞTERİ TEMİNİ ÜRÜNLER İÇİN KATALOG DEĞERLERİNİ KONTROL EDİNİZ			

GAZ TESİSATI (DOĞAL GAZ)						
S.NO		KW	V.	M ² /SA.	AÇIKLAMA	AD. TOP LAM KW.
MUTFAK						
GM13	ZANUSSI FIRIN		KW	0,0	M ² /SA. H: 130 CM KÜRESEL VANA (21mbar)	1 0,0
GM15	ELECTROLUX FIRIN	31	KW	3,2	M ² /SA. H: 65 CM KÜRESEL VANA (21mbar)	1 3,2
GM41	2'Lİ OCAK	13	KW	1,4	M ² /SA. H: 65 CM KÜRESEL VANA (21mbar)	2 2,7
GM42	6'Lİ OCAK	39	KW	4,1	M ² /SA. H: 65 CM KÜRESEL VANA (21mbar)	2 8,1

SIHHİ TESİSAT

MARCELLO MATTEO RESTURANT
BAR VE MUTFAK PROJESİ

DESIGNED/ TASARIM	
DRAWN/ ÇİZEN	ADEM AKPINAR
CHECKED/ KONTROL	ADEM AKPINAR
DATE/ TARİHİ	17.09.2022

Sktürk
ÇAĞLAYAN MAH. FEVZİ ÇAKMAK CAD. NO: 67/B
KAĞITHANE/ İSTANBUL
p: 0212 909 4312
w: skturk.com.tr | e: info@skturk.com.tr

00.00.0000
1/50 (A1)

2022-102-3