


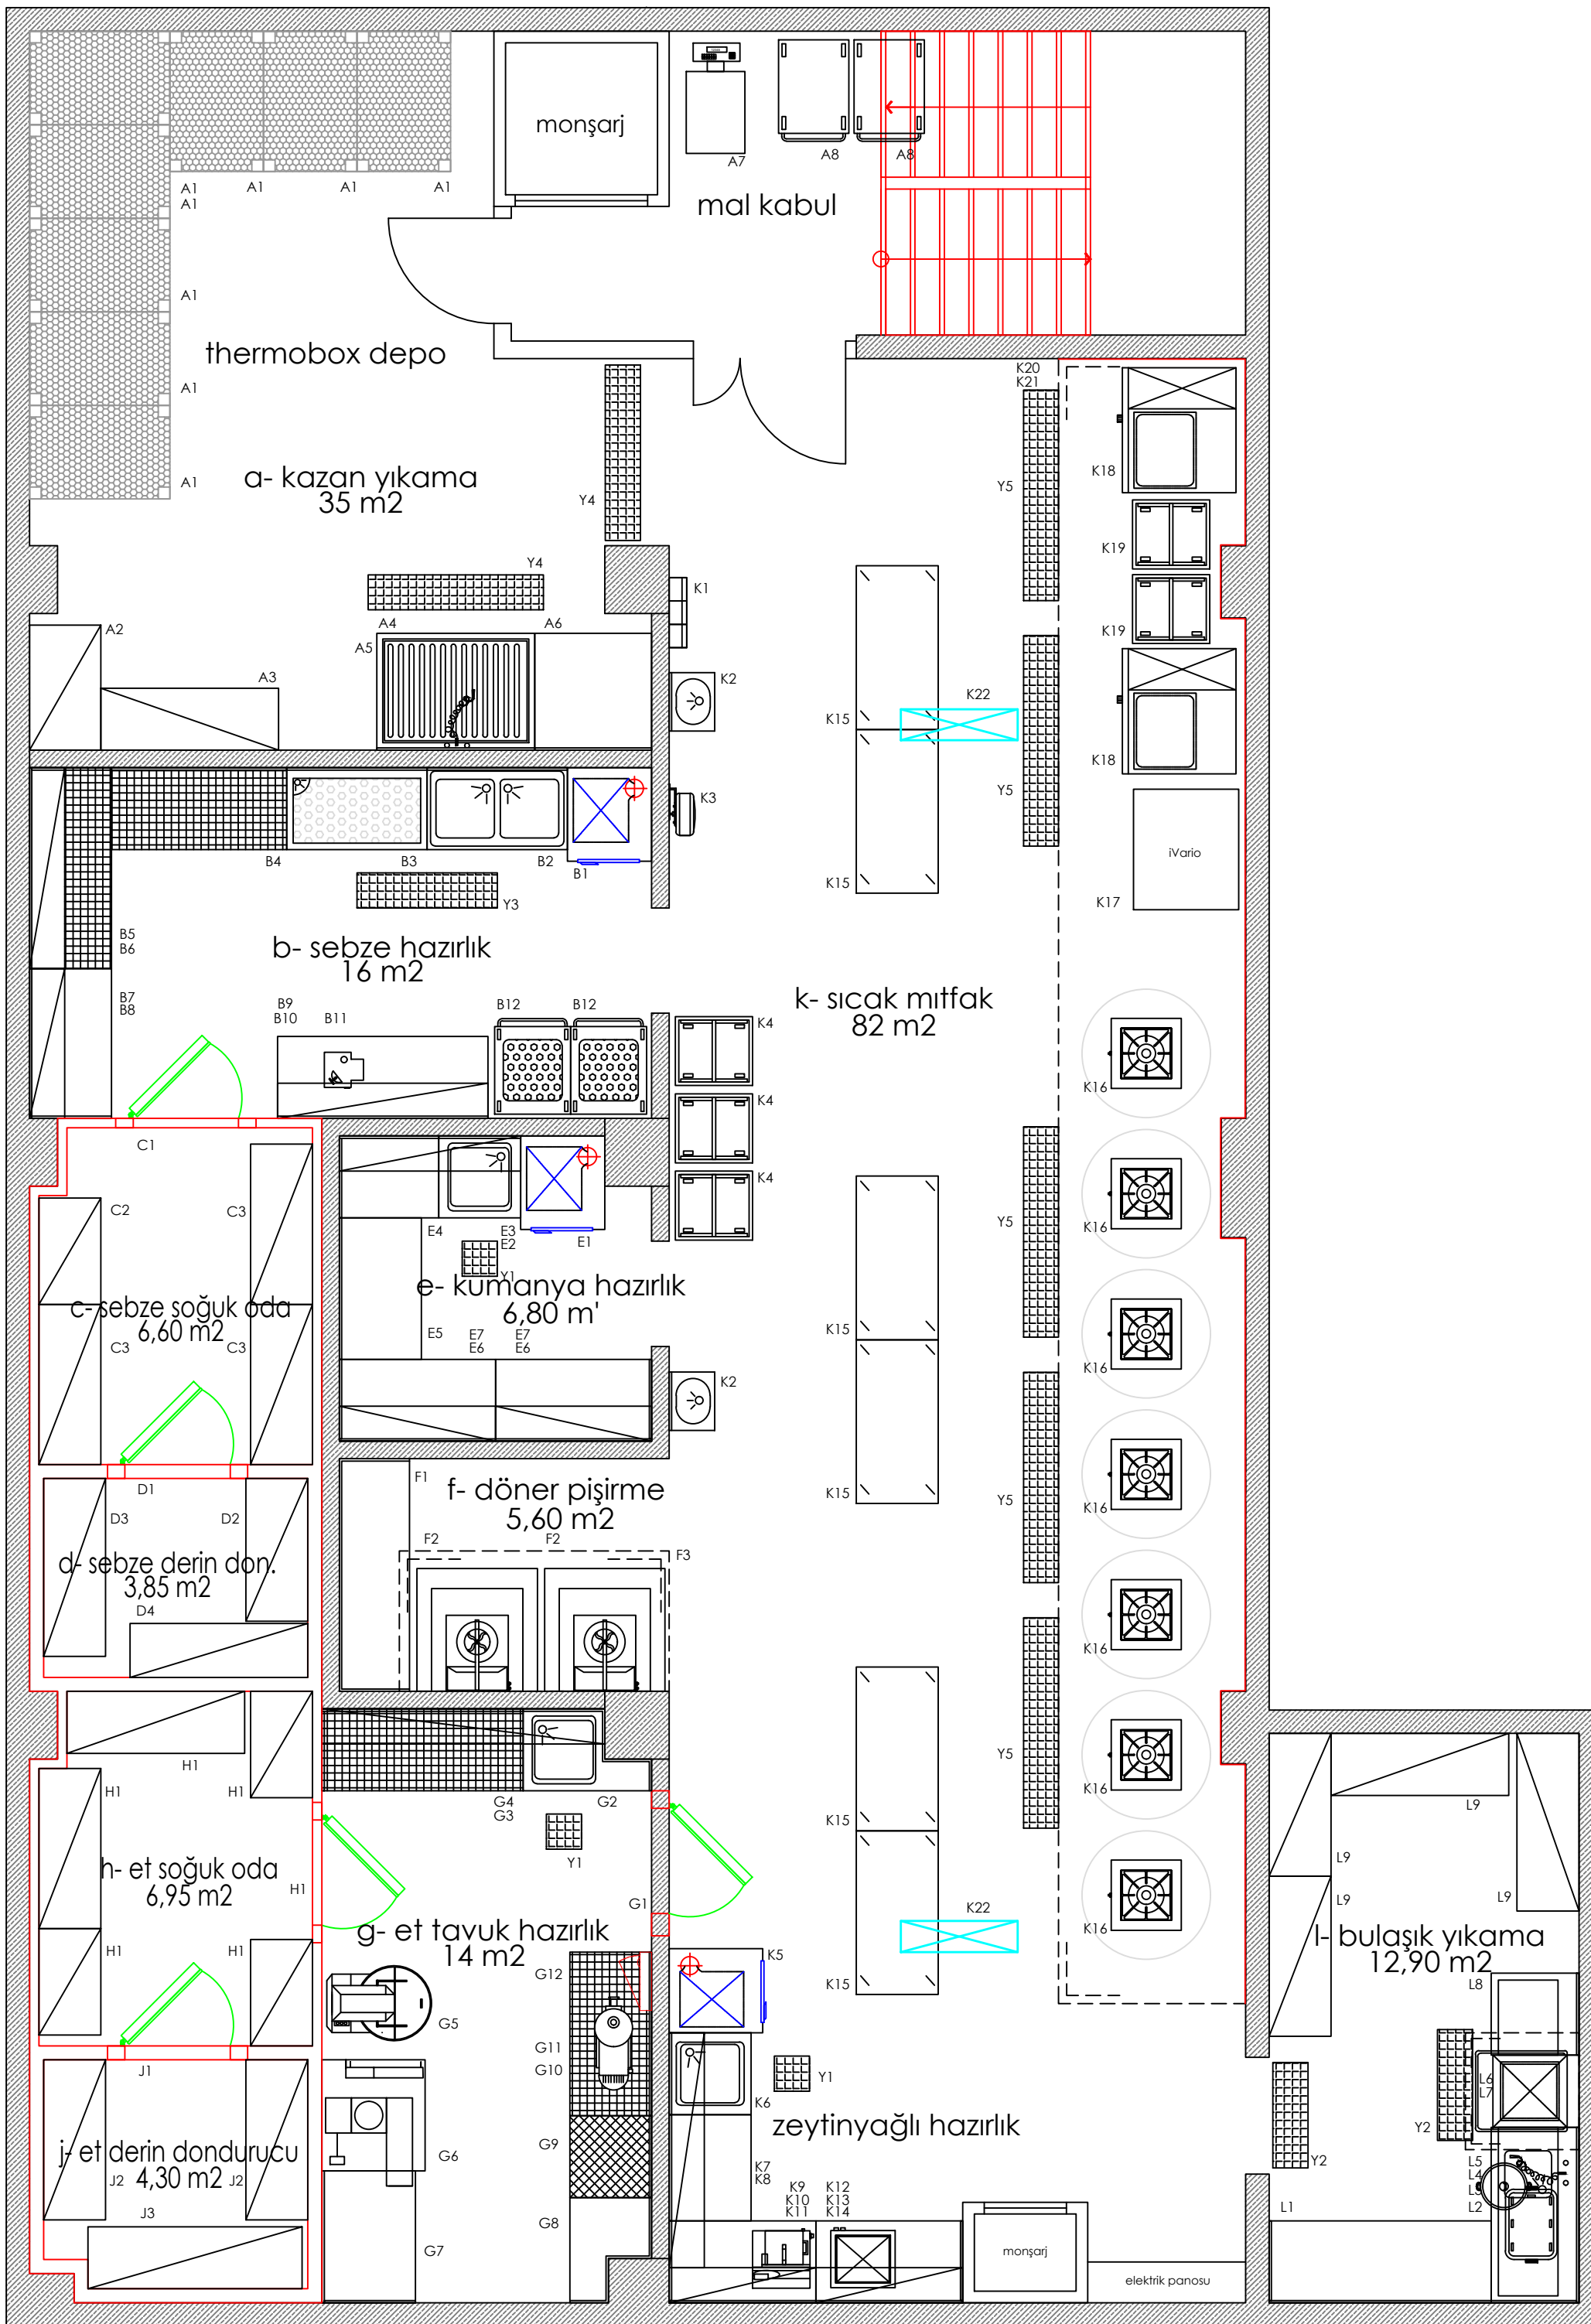

P.NO	ÜRÜN ADI	ÖLÇÜ	AD.
A- THERMOBOX & KAZAN YIKAMA			
A1	POLİETİLEN PALET	120*80*16	8
A2	İSTİF RAFI, 4 KATLI, DEMONTE	107*53*160	1
A3	İSTİF RAFI, 4 KATLI, DEMONTE	152*53*160	1
A4	KAZAN YIKAMA EVYESİ	135*100*57/9	1
A5	ÖN YIKAMA DUŞU, DUVARA MONTE	-	1
A6	ÇALIŞMA TEZGAHI	100*100*57/9	1
B- SEBZE HAZIRLIK			
B1	DEPO TİPİ BUZDOLABI, TEK KAPILI	68*85*209	1
B2	ÇİFT EVYELİ ÇALIŞMA TEZGAHI	120*70*85	1
B3	SEBZE YIKAMA EVYESİ	120*70*85	1
B4	POLİETİLEN TABLALI ÇALIŞMA TEZGAHI, TABAN RAFLI	150*70*85	1
B5	POLİETİLEN TABLALI ÇALIŞMA TEZGAHI, TABAN RAFLI	170*70*85	1
B6	DUVAR RAFI	170*30*4	1
B7	ÇALIŞMA TEZGAHI, TABAN RAFLI	126*70*85	1
B8	DUVAR RAFI	126*30*4	1
B9	ÇALIŞMA TEZGAHI, TABAN VE ARA RAFLI	180*70*85	1
B10	DUVAR RAFI	180*30*4	1
B11	SEBZE DOĞRAMA MAKİNASI	-	1
B12	SEBZE TAŞIMA ARABASI	70*70*85	2
C- SEBZE SOĞUK ODA			
C1	PANEL TİP SOĞUK ODA	250*310*240	1
C2	İSTİF RAFI, 4 KATLI, DEMONTE	91*53*160	1
C3	İSTİF RAFI, 4 KATLI, DEMONTE	137*53*160	3
D- SEBZE DERİN DONDURUCU ODA			
D1	PANEL TİP DERİN DONDURUCU ODA	250*195*240	1
D2	İSTİF RAFI, 4 KATLI, DEMONTE	122*53*160	1
D3	İSTİF RAFI, 4 KATLI, DEMONTE	152*53*160	1
D4	İSTİF RAFI, 4 KATLI, DEMONTE	152*46*160	1
E- KUMANYA HAZIRLIK			
E1	DEPO TİPİ BUZDOLABI, TEK KAPILI	68*85*209	1
E2	TEK EVYELİ ÇALIŞMA TEZGAHI	70*70*85	1
E3	DUVAR RAFI	155*30*4	1
E4	ÇALIŞMA TEZGAHI	85*70*85	1
E5	ÇALIŞMA TEZGAHI, TABAN VE ARA RAFLI	120*70*85	1
E6	ÇALIŞMA TEZGAHI, TABAN VE ARA RAFLI	134*70*85	2
E7	DUVAR RAFI	134*30*4	2
F- DÖNER PİŞİRME			
F1	ÇALIŞMA TEZGAHI, TABAN RAFLI	200*60*85	1
F2	DÖNER OCAĞI, GAZLI - ADG5D	103*105*209	2
F3	DAVLUMBAZ, DUVAR TİPİ, FİLTRELİ	230*120*50	1
G- ET TAVUK HAZIRLIK			
G1	ET TAVUK HAZIRLIK ODASI ORTAM SOĞUTMA	282*508*330	1
G2	TEK EVYELİ ÇALIŞMA TEZGAHI	110*70*85	1
G3	POLİETİLEN TABLALI ÇALIŞMA TEZGAHI, RAFLI, TEK ÇEKMECELİ	170*70*85	1
G4	DUVAR RAFI	240*30*4	1
G5	SİRAL HAMUR YOĞURMA MAKİNASI	50 KG	1
G6	KÖFTE ŞEKLİLENDİRME MAKİNASI	90*90*160	1
G7	HAREKETLİ ÇALIŞMA TEZGAHI, TABAN RAFLI	110*80*85	1
G8	ÇALIŞMA TEZGAHI, TABAN VE ARA RAFLI	90*70*85	1
G9	ET KÜTÜCÜ	70*70*85	1
G10	POLİETİLEN TABLALI ÇALIŞMA TEZGAHI, RAFLI, TEK ÇEKMECELİ	140*70*85	1
G11	ET KIYMA MAKİNASI	-	1
G12	BIÇAK STERİL DOLABI	10 BİÇAKLIK	1
H- ET SOĞUK ODA			
H1	PANEL TİP SOĞUK ODA	250*330*240	1
H2	İSTİF RAFI, 4 KATLI, DEMONTE	91*53*160	3
H2	İSTİF RAFI, 4 KATLI, DEMONTE	137*53*160	2
J- ET DERİN DONDURUCU ODA			
J1	PANEL TİP SOĞUK ODA	250*220*240	1
J2	İSTİF RAFI, 4 KATLI, DEMONTE	137*53*160	2
J3	İSTİF RAFI, 4 KATLI, DEMONTE	183*53*160	1
K- SICAK MUTFAK			
K1	BONE GALOŞLUK	70*60*20	1
K2	DİZDEN KUMANDALI EL YIKAMA LAVABOSU	-	2
K3	YER YIKAMA HORTUMU	10 MT	1
K4	TEPSİ TAŞIMA ARABASI, TEKLİ	GN 2/1	3
K5	DEPO TİPİ BUZDOLABI, TEK KAPILI	68*85*209	1
K6	TEK EVYELİ ÇALIŞMA TEZGAHI	70*70*85	1
K7	DUVAR RAFI	200*30*4	1
K8	ÇALIŞMA TEZGAHI, TABAN VE ARA RAFLI	90*70*85	1
K9	ÇALIŞMA TEZGAHI, TABAN VE ARA RAFLI	125*70*85	1
K10	GIDA DİLİMLEME MAKİNASI	Ø300	1
K11	DUVAR RAFI	125*30*4	1
K12	ÇALIŞMA TEZGAHI, TABAN VE ARA RAFLI	125*70*85	1
K13	DUVAR RAFI	125*30*4	1
K14	VAKUMLAMA MAKİNASI	-	1
K15	HAREKETLİ ÇALIŞMA TEZGAHI, TABAN RAFLI	140*70*85	6
K16	YER OCAĞI, GAZLI	70*70*50	7
K17	İVario ÇOK FONKSİYONLU PİŞİRİCİ	103*90*108	1
K18	YEMEKÇİLİK FIRINI, GAZLI	20 GN 2/1	2
K19	FIRIN ARABASI	20 GN 2/1	2
K20	DUVAR SACI	1700*190*	1
K21	DAVLUMBAZ, DUVAR TİPİ, FİLTRELİ	1410*160*50	1
K22	SİNEK ÖLDÜRÜCÜ, TAVANA MONTE	-	2
L- BULAŞIK YIKAMA			
L1	ÇALIŞMA TEZGAHI, TABAN RAFLI	190*70*85	1
L2	TEK EVYELİ BYM GİRİŞ TEZGAHI	150*75*85	1
L3	ÖN YIKAMA DUŞU, ARA MUSLUKLİ, TEZGAHA MONTE	-	1
L4	ÇÖP ARABASI	Ø40*50	1
L5	YAĞ TUTUCU	1 lt/sn	1
L6	BULAŞIK YIKAMA MAKİNASI, GİYOTİN TİPİ	1000 lt/s	1
L7	DAVLUMBAZ, DUVAR TİPİ	100*97*50	1
L8	BYM ÇIKIŞ TEZGAHI	70*75*85	1
L9	İSTİF RAFI, 4 KATLI, DEMONTE	152*53*160	4
Y- YER IZGARASI			
Y1	YER IZGARASI	30*30*14	3
Y2	YER IZGARASI	95*30*14	2
Y3	YER IZGARASI	120*30*14	1
Y4	YER IZGARASI	150*30*14	3
Y5	YER IZGARASI	185*30*14	5

AKADEMİ GURME | CATERING MUTFAĞI

BAR VE MUTFAK PROJESİ

DESIGNED/ TASARIM

ADAM AKPINAR

DRAWN/ ÇİZEN

ADAM AKPINAR

CHECKED/ KONTROL

ADAM AKPINAR

DATE/ TARİH

03.01.2022

REV. DATE

REV. TARİHİ

27.01.2023

SCALE

ÖLÇEK

1/50 (A2)

SKTürk

ÇAĞLAYAN MAH. FEVZİ ÇAKMAK CAD. NO: 67/B

KAĞITHANE/ İSTANBUL

p:0212 909 4312

w: skturk.com.tr | e: info@skturk.com.tr

2023-001-1

THIS DRAWING REMAINS THE PROPERTY OF SKTÜRK ENDÜSTRİYEL MUTFAK SAN. VE TİC. LTD. ŞTİ. AND MAY ONLY BE COPIED COMPLETELY OR PARTLY OR ISSUED TO THIRD PARTY WITH OUR PRIOR CONSENT. BU BİSMİ SKTÜRK ENDÜSTRİYEL MUTFAK SAN. VE TİC. LTD. ŞTİ. NİN MALİ OLUP YAZILI İZİN OLMAZDAN KAHRİMEN VEYA TAMAMEN KOPYA EDİLEMEZ VE ÜÇÜNCÜ ŞAHİTLERİNE VERİLEMEZ.