
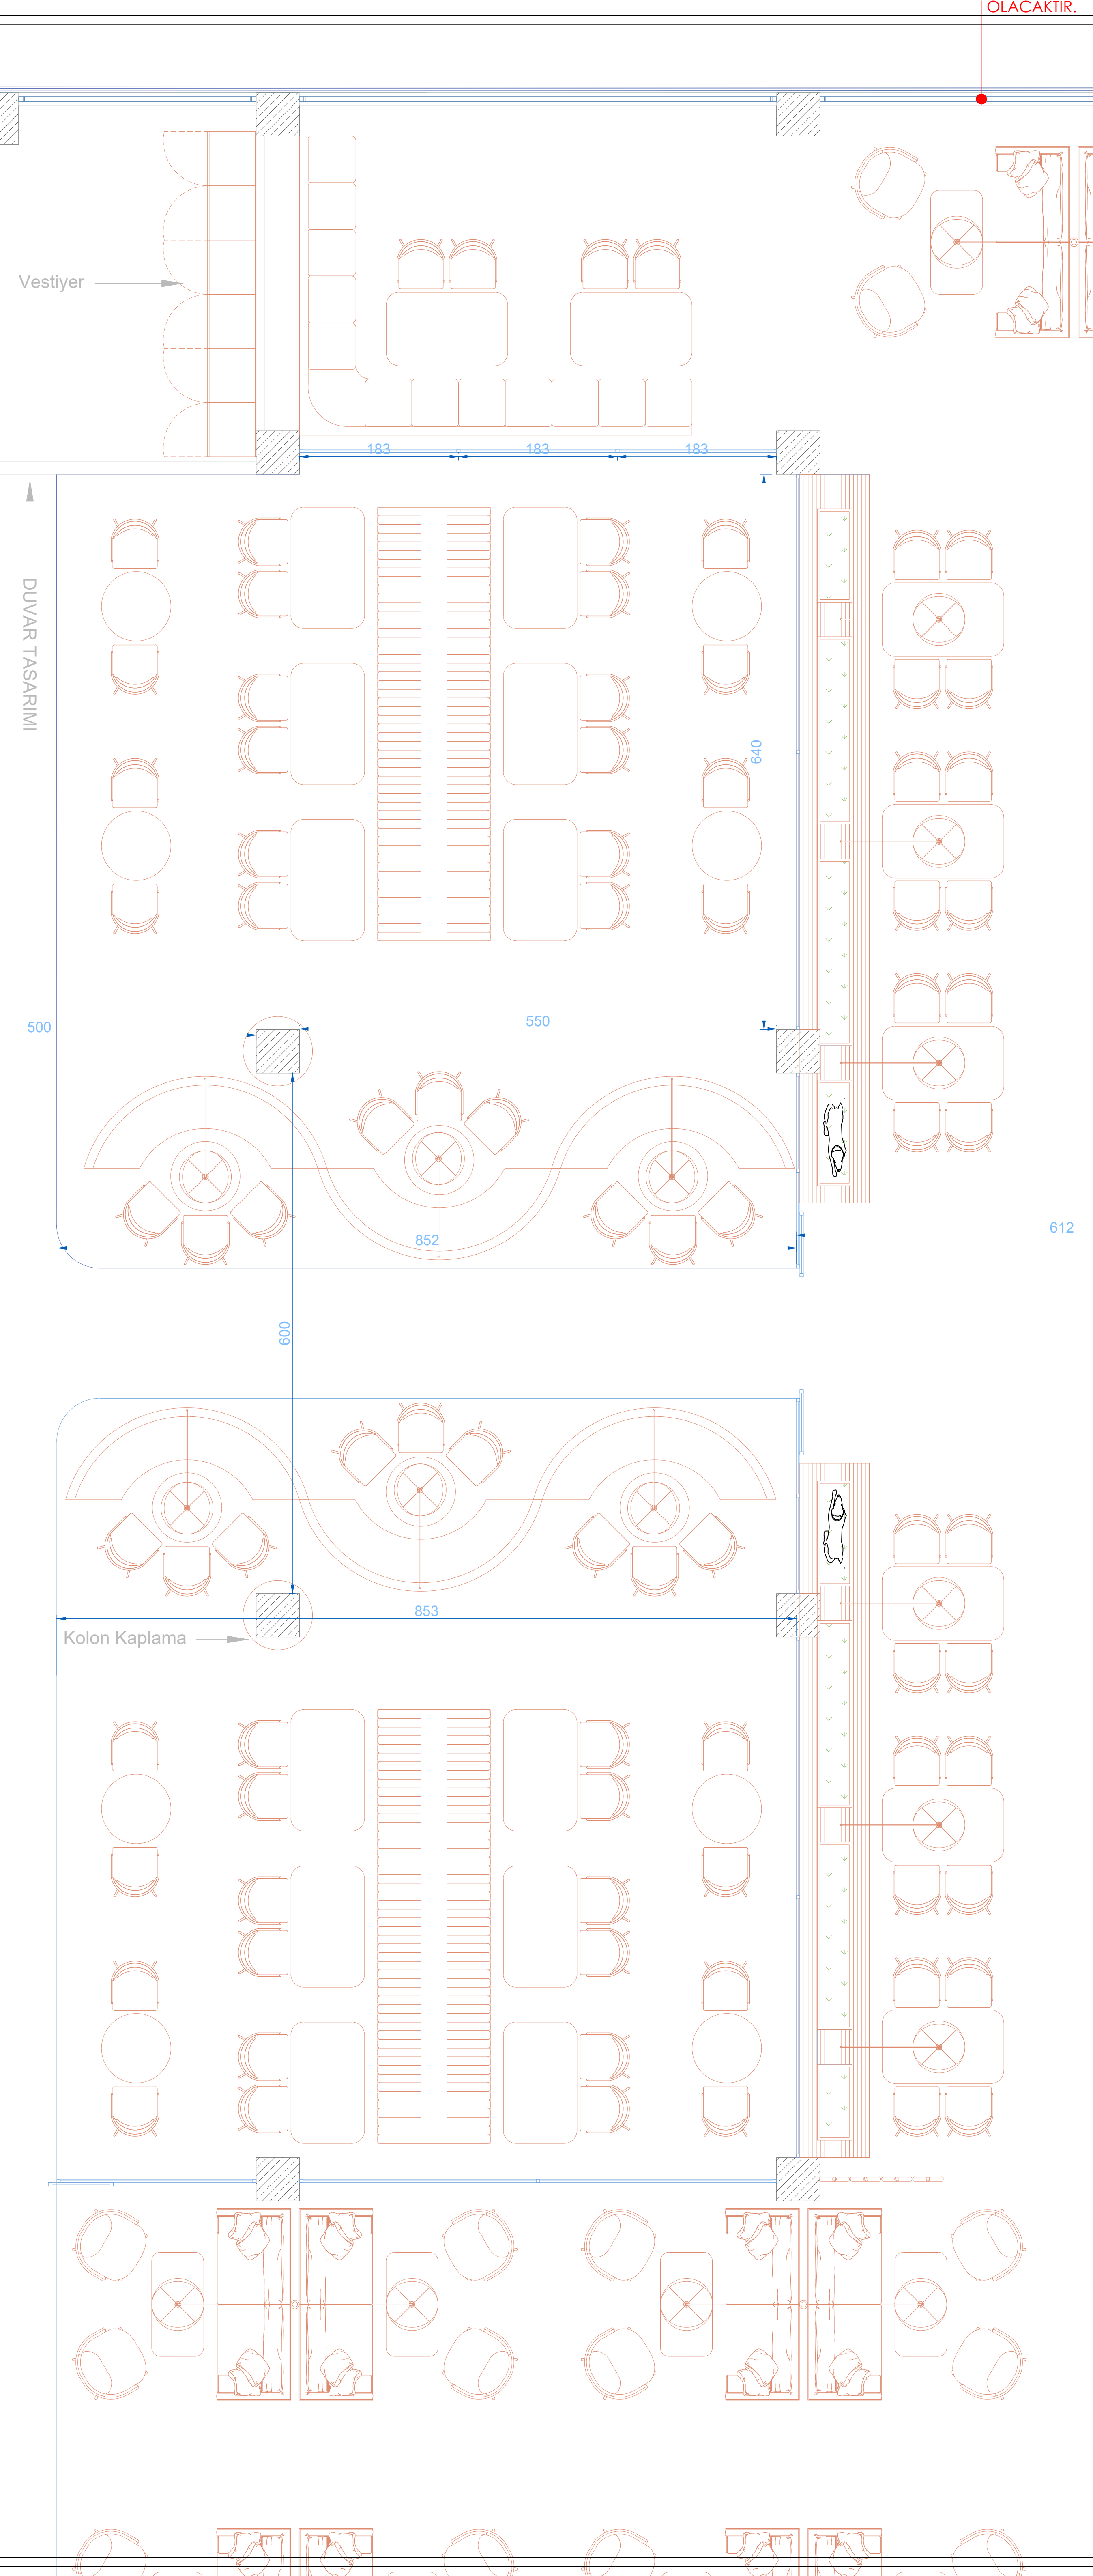


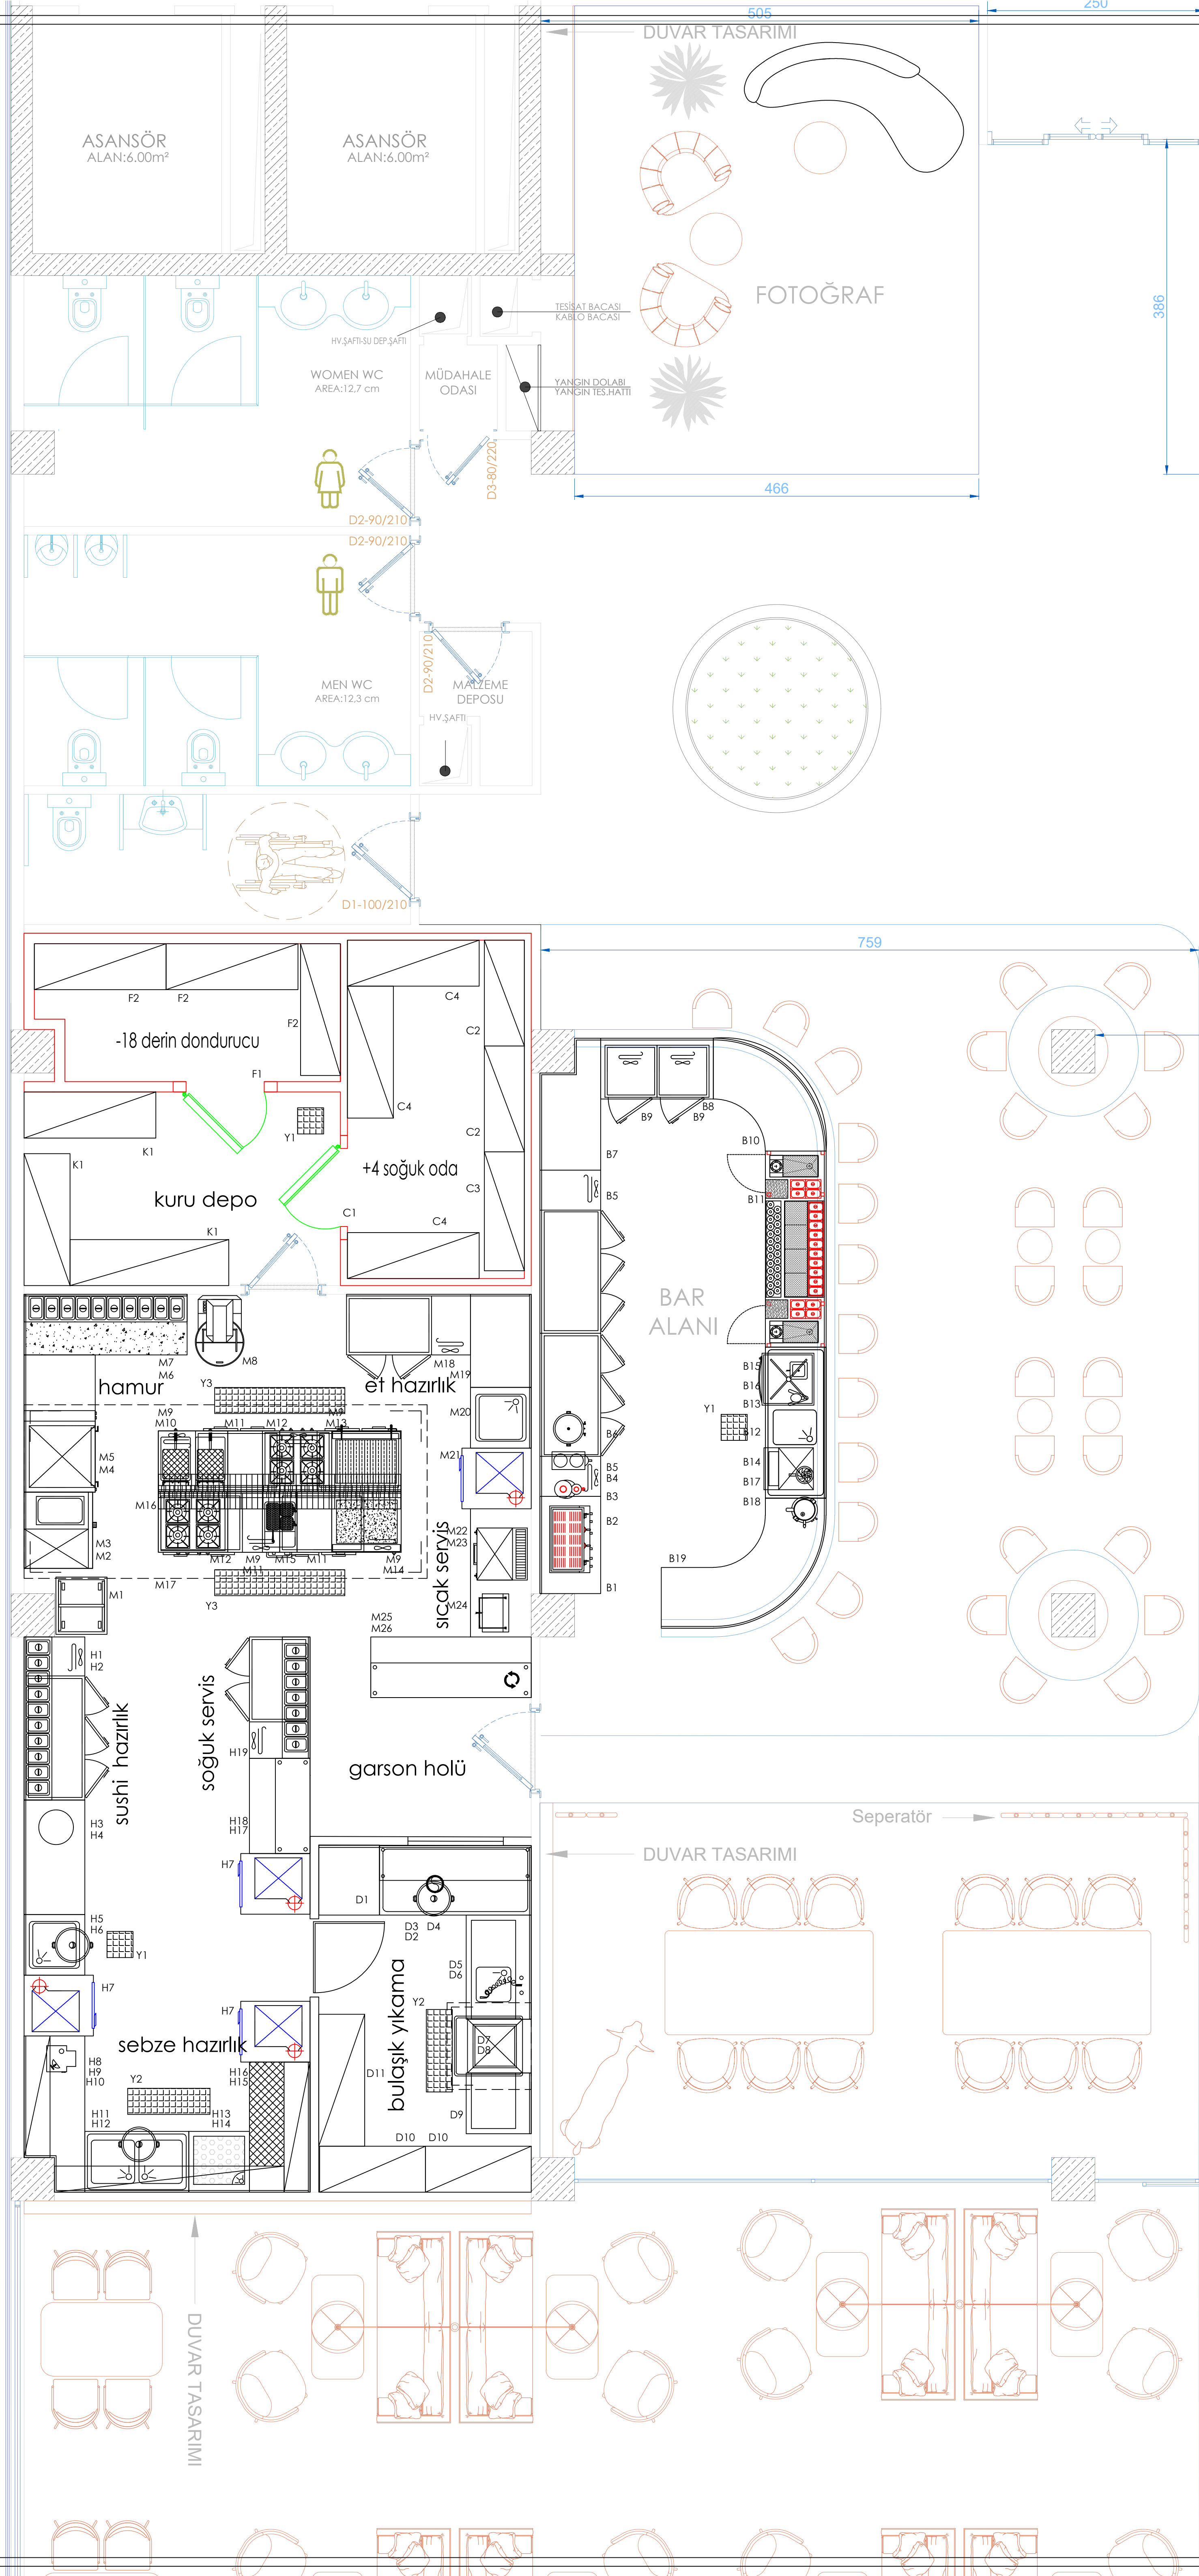

P.NO	ÜRÜN ADI	ÖLÇÜ	AD.
K- KURU DEPO			
K1	İSTİF RAFI		3
C- SOĞUK ODA			
C1	PANEL TİP SOĞUK ODA		1
C2	İSTİF RAFI, 4 KATLI, DEMONTE		2
C3	İSTİF RAFI, 4 KATLI, DEMONTE		1
C4	İSTİF RAFI, 4 KATLI, DEMONTE		3
F- DERİN DONDURUCU ODA			
F1	PANEL TİP. SOĞUK ODA		1
F2	İSTİF RAFI, 4 KATLI, DEMONTE		3
M- MUTFAK			
M1	TEPSİ TAŞIMA ARABASI		1
M2	FIRIN STANDI, TEPİSİ İSTİFLİ		1
M3	YEMEKÇİLİK FIRINI		1
M4	FIRIN STANDI		1
M5	PIZZA FIRINI, ÇİFT KATLI		1
M6	MERMER TABLALI ÇALIŞMA TEZGAHI		1
M7	DUVAR DOLABI, SÜRGÜ KAPILI		1
M8	SPIRAL MIKSER		1
M9	ÇİHAZALTI BUZDOLABI, ÇİFT SIRA ÇEKMECELİ		4
M10	FRİTÖZ, ÇİFT HAZNELİ, ELK., SETÜSTÜ		1
M11	NÖTR ARA TEZGAH, SETÜSTÜ		3
M12	DÖRT AÇIK ALEVİLİ OCAK, GAZLI, SETÜSTÜ		2
M13	DÖKÜM IZGARA, SETÜSTÜ, GAZLI		1
M14	PLATE IZGARA, SETÜSTÜ, GAZLI		1
M15	MAKARNA PIŞIRICI, ELK., SETÜSTÜ		1
M16	TAVA RAFI		1
M17	DAVLUMBAZ, ADA TİPİ, FİLTRELİ		1
M18	TEZGAH TİPİ BUZDOLABI, 2 KAPILI		1
M19	ÇALIŞMA TEZGAHI		1
M20	TEK EVYELİ ÇALIŞMA TEZGAHI		1
M21	DEPO TİPİ BUZDOLABI, TEK KAPILI		1
M22	ÇALIŞMA TEZGAHI, TABAN VE ARA RAFLI		1
M23	SALAMANDER, ASANSÖRLÜ, ELK.		1
M24	TOST MAKİNASI		1
M25	SICAK DOLAPLI SERVİS TEZGAHI		1
M26	SERVİS RAFI		1
H- HAZIRLIK			
H1	TEZGAH TİPİ BUZDOLABI, ÜÇ KAPILI		1
H2	SUSHI CASE		1
H3	ÇALIŞMA TEZGAHI, TABAN VE ARA RAFLI		1
H4	RICE COOKER		1
H5	TEK EVYELİ ÇALIŞMA TEZGAHI		1
H6	ÇÖP ARABASI		1
H7	DEPO TİPİ BUZDOLABI, TEK KAPILI		3
H8	ÇALIŞMA TEZGAHI, TABAN VE ARA RAFLI		1
H9	DUVAR RAFI		1
H10	SEBZE DOĞRAMA MAKİNASI		1
H11	ÇİFT EVYELİ ÇALIŞMA TEZGAHI		1
H12	ÇÖP ARABASI		1
H13	SEBZE YIKAMA EVYESİ		1
H14	DUVAR RAFI		1
H15	POLİETİLEN TABLALI ÇALIŞMA TEZGAHI		1
H16	DUVAR RAFI		1
D- BULAŞIK YIKAMA			
D1	ÇALIŞMA TEZGAHI, TABAN RAFLI		1
D2	BULAŞIK SIYIRMA TEZGAHI		1
D3	BASKET RAFI		1
D4	ÇÖP ARABASI		1
D5	TEK EVYELİ BYM GİRİŞ TEZGAHI		1
D6	ÖN YIKAMA DÜŞÜ		1
D7	BULAŞIK YIKAMA MAKİNASI, GİYOTİN TİP		1
D8	DAVLUMBAZ, DUVAR TİPİ		1
D9	BYM ÇIKIŞ TEZGAHI		1
D10	İSTİF RAFI, 4 KATLI, DEMONTE		2
D11	İSTİF RAFI, 4 KATLI, DEMONTE		1
B- BAR			
B1	KAHVE ÇEKMECELİ ÇALIŞMA TEZGAHI, DOLAPLI		1
B2	ESPRESSO KAHVE MAKİNASI		1
B3	KAHVE DEĞİRMENİ		1
B4	FİLTRE KAHVE MAKİNASI		1
B5	CAM KAPILI TEZGAH TİPİ BUZDOLABI, 3 KAPILI		2
B6	ÇAY OTOMATI		1
B7	ÇALIŞMA TEZGAHI, TABAN VE ARA RAFLI, DOLAPLI		1
B8	ÇALIŞMA TEZGAHI		1
B9	TEK KAPILI DERİN DONDURUCU		2
B10	ÇALIŞMA TEZGAHI, TABAN VE ARA RAFLI		1
B11	KOKTEYL İSTASYONU		1
B12	TEK EVYELİ ÇALIŞMA TEZGAHI		1
B13	BULAŞIK YIKAMA MAKİNASI, SETALTI		1
B14	BUZ MAKİNASI		1
B15	BAR BLENDER		1
B16	BAR MIKSER		1
B17	PORTAKAL SIKMA MAKİNASI		1
B18	KATI MEYVE SIKACAĞI		1
B19	ÇALIŞMA TEZGAHI, TABAN VE ARA RAFLI		1
Y- YER IZGARASI			
Y1	YER IZGARASI	30*30*14	3
Y2	YER IZGARASI	95*30*14	2
Y3	YER IZGARASI	150*30*14	2

TERAS RESTAURANT | KONGO
BAR VE MUTFAK PROJESİ

DESIGNED/ TASARIM	ADEM AKPINAR
DRAWN/ ÇİZEN	ADEM AKPINAR
CHECKED/ KONTROL	ADEM AKPINAR
DATE/ TARİH	20.11.2023

REVİZYON	00.00.0000	ÇİZİM	1/50 (A1)
----------	------------	-------	-----------

TERAS RESTAURANT | KONGO BAR VE MUTFAK PROJESİ
KAĞITHANE/ İSTANBUL
p: 0212 909 4312
w: skturk.com.tr | e: info@skturk.com.tr

TERAS RESTAURANT | KONGO
BAR VE MUTFAK PROJESİ

00.00.0000

1/50 (A1)

2023-064