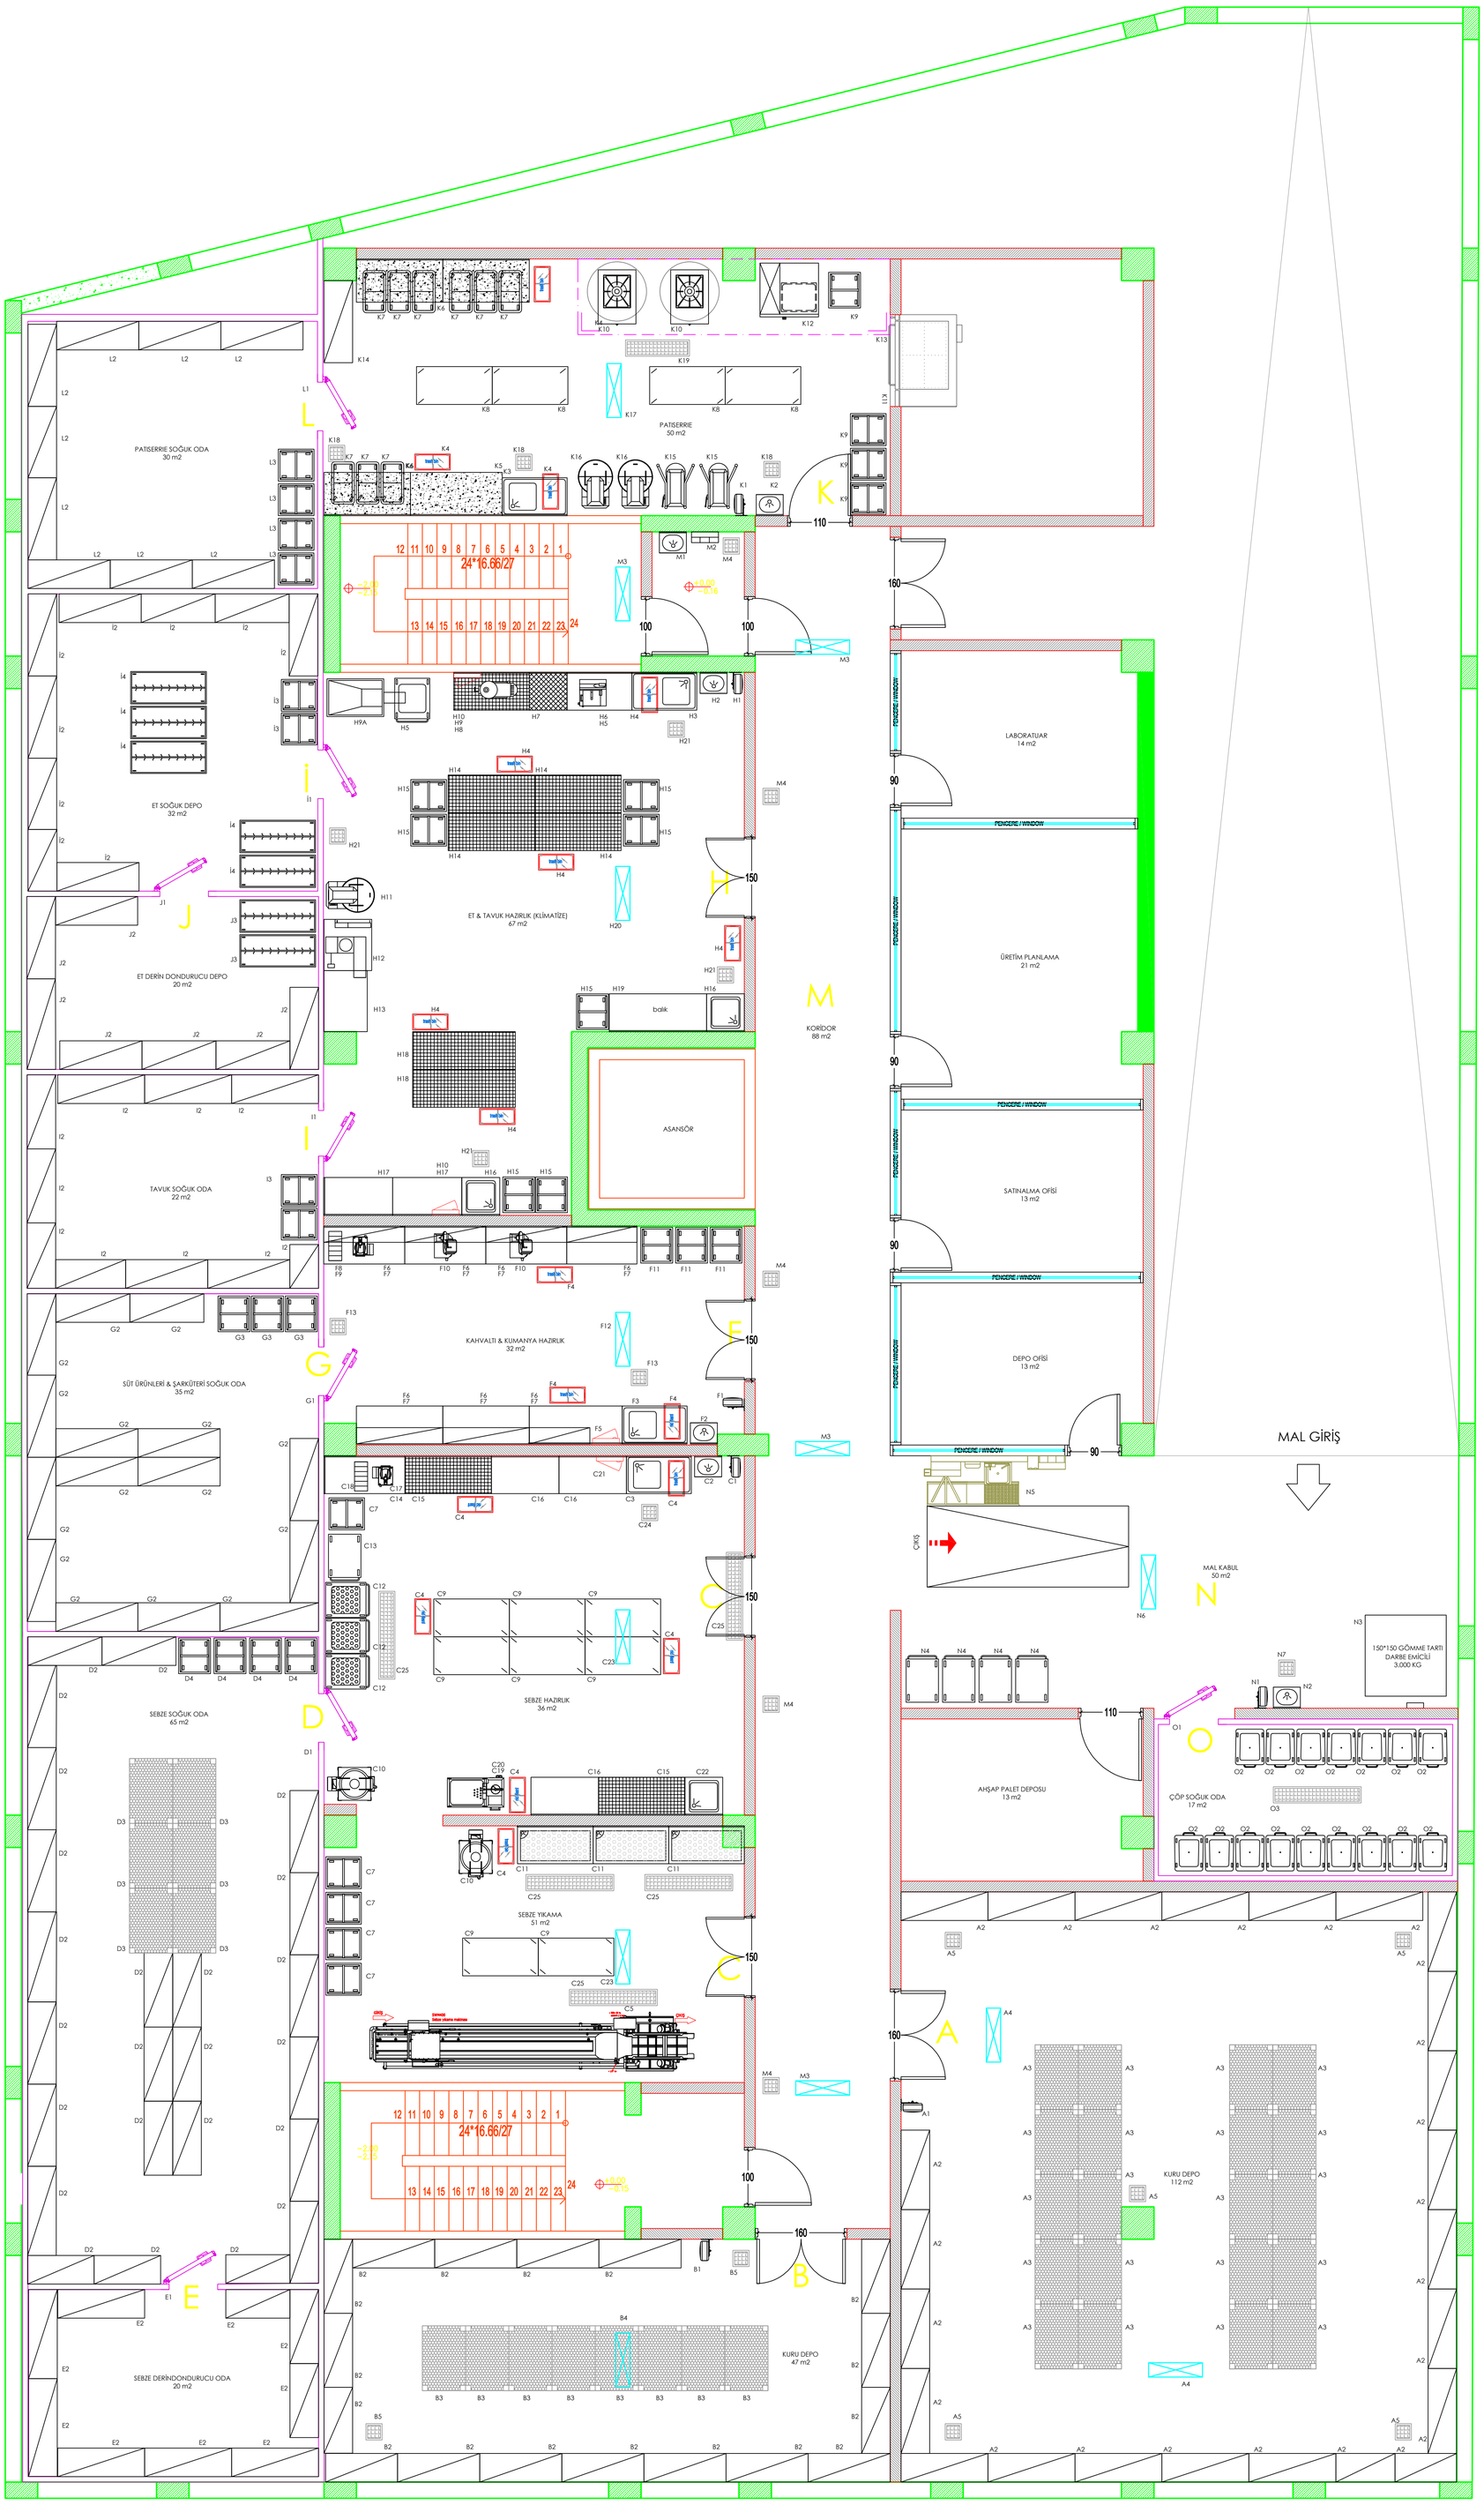

±0.00 KOTU BODRUM KAT PLANI (1/50)

P.NO	ÜRÜN ADI	ÖLÇÜ	AD.
A- KURU DEPO			
A1	YER YIKAMA HORTUMU	10 mt.	1
A2	İSTİF RAFI, 4 KATLI	152*53*213	24
A3	PALET	120*80*15	20
A4	SİNEK ÖLDÜRÜCÜ, PASLANMAZ	100 m2	1
A5	YER IZGARASI, İZOLASYONLU	30*30*15	1
B- KURU DEPO			
B1	YER YIKAMA HORTUMU	10 mt.	1
B2	İSTİF RAFI, 4 KATLI	152*53*213	17
B3	PALET	120*80*15	8
B4	SİNEK ÖLDÜRÜCÜ, PASLANMAZ	100 m2	1
B5	YER IZGARASI, İZOLASYONLU	30*30*15	2
C- SEBZE YIKAMA & HAZIRLIK			
C1	YER YIKAMA HORTUMU	10 mt.	2
C2	DİZDEN KUMANDALI EL YIKAMA LAVABOSU	-	2
C3	TEK EVYELİ ÇALIŞMA TEZGAHI	90*70*85	1
C4	ÇÖP KOVASI, ARABALI	100 lt.	7
C5	SEBZE YIKAMA MAKİNASI	390 cm	1
C6	ÇÖP ARABASI	400 lt.	2
C7	GASTRONOM TEPSİ TAŞIMA ARABASI, GN 2/1	44*63*172	5
C9	HAREKETLİ ÇALIŞMA TEZGAHI, TABAN VE ARA RAFLI	140*70*85	8
C10	SEBZE KURUTMA MAKİNASI	60 lt.	2
C11	SEBZE YIKAMA EVYESİ	140*70*85	3
C12	SEBZE BASMA ARABASI	70*65*70	3
C13	SERVİS ARABASI, TABAN VE ARA RAFLI	90*60*85	1
C14	ÇALIŞMA TEZGAHI, TABAN VE ARA RAFLI	140*70*85	1
C15	POLİETİLEN TABLALI ÇALIŞMA TEZ., TABAN RAFLI, TEK ÇEKMECELİ	160*70*85	1
C16	ÇALIŞMA TEZGAHI, TABAN VE ARA RAFLI	140*70*85	3
C17	SEBZE DOĞRAMA MAKİNASI	-	1
C18	CL50 DİSK SETİ	-	1
C19	SEBZE DOĞRAMA MAKİNASI, CL60 ÇALIŞMA İSTASYONU	-	1
C20	CL60 DİSK SETİ	-	1
C21	BIÇAK STERİLİZASYON DOLABI	10 BIÇAKLIK	1
C22	TEK EVYELİ ÇALIŞMA TEZGAHI	70*70*85	2
C23	SİNEK ÖLDÜRÜCÜ, PASLANMAZ	100 m2	1
C24	YER IZGARASI, İZOLASYONLU	30*30*15	1
C25	YER IZGARASI, İZOLASYONLU	165*30*15	6
D- SEBZE SOĞUK ODA			
D1	PANEL TİP SOĞUK ODA, ZEMİNSİZ	560*1225*270	1
D2	İSTİF RAFI, 4 KATLI	152*53*213	24
D3	PALET	120*80*15	6
D4	GASTRONOM TEPSİ TAŞIMA ARABASI, GN 2/1	44*63*172	4
E- SEBZE DERİN DONDURUCU ODA			
E1	PANEL TİP SOĞUK ODA, ZEMİNSİZ	560*365*270	1
E2	İSTİF RAFI, 4 KATLI	152*53*213	9
F- KAHVALTI & KUMANYA HAZIRLIK			
F1	YER YIKAMA HORTUMU	10 mt.	1
F2	DİZDEN KUMANDALI EL YIKAMA LAVABOSU	-	1
F3	TEK EVYELİ ÇALIŞMA TEZGAHI	90*70*85	1
F4	ÇÖP KOVASI, ARABALI	100 lt.	3
F5	ÇALIŞMA TEZGAHI, TABAN VE ARA RAFLI	160*70*85	7
F6	DUVAR RAFI	160*30*4	7
F7	SİNEK ÖLDÜRÜCÜ, PASLANMAZ	100 m2	1
F8	SEBZE DOĞRAMA MAKİNASI	-	1
F9	CL50 DİSK SETİ	-	1
F10	GIDA DİLİMLEME MAKİNASI	Q300	2
F11	GASTRONOM TEPSİ TAŞIMA ARABASI, GN 2/1	44*63*172	2
F12	SİNEK ÖLDÜRÜCÜ, PASLANMAZ	100 m2	1
F13	YER IZGARASI, İZOLASYONLU	30*30*15	2
G- SÜT ÜRÜNLERİ & ŞARKÜTERİ SOĞUK ODA			
G1	PANEL TİP SOĞUK ODA, ZEMİNSİZ	560*645*270	1
G2	İSTİF RAFI, 4 KATLI	152*53*213	15
G3	GASTRONOM TEPSİ TAŞIMA ARABASI, GN 2/1	44*63*12	3
H- ET & TAVUK HAZIRLIK			
H1	YER YIKAMA HORTUMU	10 mt.	1
H2	DİZDEN KUMANDALI EL YIKAMA LAVABOSU	-	1
H3	TEK EVYELİ ÇALIŞMA TEZGAHI	60*90*85	1
H4	ÇÖP KOVASI, ARABALI	100 lt.	6
H5	ÇALIŞMA TEZGAHI, TABAN VE ARA RAFLI	180*70*85	2
H6	GIDA DİLİMLEME MAKİNASI	Q300	1
H7	ET KÜTÜĞÜ, POLİETİLEN, KIRMIZI	70*70*85	1
H8	POLİETİLEN TAB. ÇAL. TEZ., TABAN RAF, TEK ÇEK. KIRMIZI	140*70*85	1
H9	ET KIYMA MAKİNASI, SOĞUTMALI	NO: 32	1
H10	BIÇAK STERİLİZASYON DOLABI	10 BIÇAKLIK	2
H11	SPİRAL HAMUR YOĞURMA MAKİNASI	60 lt.	1
H12	KÖFTE ŞEKİLLENDİRME MAKİNASI	-	1
H13	ÇALIŞMA TEZGAHI, TABAN VE ARA RAFLI	100*70*85	1
H14	POLİETİLEN TABLALI ÇALIŞMA TEZ., TABAN RAFLI, KIRMIZI	160*70*85	4
H15	GASTRONOM TEPSİ TAŞIMA ARABASI, GN 2/1	44*63*172	7
H16	TEK EVYELİ ÇALIŞMA TEZGAHI	70*70*85	2
H17	ÇALIŞMA TEZGAHI, TABAN VE ARA RAFLI	130*70*85	2
H18	POLİETİLEN TABLALI ÇALIŞMA TEZ., TABAN RAFLI, SARI	160*70*85	2
H19	ÇALIŞMA TEZGAHI, TABAN VE ARA RAFLI	180*70*85	1
H20	SİNEK ÖLDÜRÜCÜ, PASLANMAZ	100 m2	1
H21	YER IZGARASI, İZOLASYONLU	30*30*15	4
I- TAVUK SOĞUK ODA			
I1	PANEL TİP SOĞUK ODA, ZEMİNSİZ	560*420*270	1
I2	İSTİF RAFI, 4 KATLI	152*53*213	10
I3	GASTRONOM TEPSİ TAŞIMA ARABASI, GN 2/1	44*63*172	2
İ- ET SOĞUK ODA			
İ1	PANEL TİP SOĞUK ODA, ZEMİNSİZ	560*560*270	1
İ2	İSTİF RAFI, 4 KATLI	152*53*213	9
İ3	GASTRONOM TEPSİ TAŞIMA ARABASI, GN 2/1	44*63*172	2
İ4	ET ASKI ARABASI	140*60*160	5
J- ET DERİN DONDURUCU ODA			
J1	PANEL TİP DERİN DONDURUCU ODA, ZEMİNSİZ	560*340*270	1
J2	İSTİF RAFI, 4 KATLI	152*53*213	7
J3	ET ASKI ARABASI	140*60*160	2
K- PATISERRIE			
K1	YER YIKAMA HORTUMU	10 mt.	1
K2	DİZDEN KUMANDALI EL YIKAMA LAVABOSU	-	1
K3	TEK EVYELİ ÇALIŞMA TEZGAHI	90*70*85	1
K4	ÇÖP KOVASI, ARABALI	100 lt.	3
K5	MERMER TABLALI ÇALIŞMA TEZGAHI, ARA RAFLI	190*80*85	3
K6	MERMER TABLALI ÇALIŞMA TEZGAHI	190*80*85	1
K7	UN-ŞEKER ARABASI	103 lt.	9
K8	HAREKETLİ ÇALIŞMA TEZGAHI, TABAN VE ARA RAFLI	140*70*85	4
K9	PATISERRIE TEPSİ TAŞIMA ARABASI, 40*60	59*66*170	3
K10	YER OCAĞI	125*80*50	2
K11	TAŞ TABANLI FIRIN, MAYALA DOLAPLI, 3 KATLI	156*131*205	1
K12	FIRIN, GAZLI- MEVCUT	20 GN 2/1	1
K13	DAVLUMBAZ, DUVAR TİPİ, FİLTRELİ	670*140*50	1
K14	İSTİF RAFI, 4 KATLI	152*53*213	1
K15	PLANET MİKSER	60 lt.	2
K16	SPİRAL HAMUR YOĞURMA MAKİNASI	60 lt.	2
K17	SİNEK ÖLDÜRÜCÜ, PASLANMAZ	100 m2	1
K18	YER IZGARASI, İZOLASYONLU	30*30*15	3
K19	YER IZGARASI, İZOLASYONLU	165*30*15	1
L- PATISERRIE SOĞUK ODA			
L1	PANEL TİP SOĞUK ODA, ZEMİNSİZ	560*520*270	1
L2	İSTİF RAFI, 4 KATLI	152*53*213	9
L3	GASTRONOM TEPSİ TAŞIMA ARABASI, GN 2/1	44*63*172	4
M- KORİDOR			
M1	DİZDEN KUMANDALI EL YIKAMA LAVABOSU	-	1
M2	BONE GALOŞLUK	-	1
M3	SİNEK ÖLDÜRÜCÜ, PASLANMAZ	100 m	4
M4	YER IZGARASI, İZOLASYONLU	30*30*15	6
M5	HİJYEN BARİYERİ	-	1
N- MAL KABÜL			
N1	DİZDEN KUMANDALI EL YIKAMA LAVABOSU	-	1
N2	YER YIKAMA HORTUMU	-	1
N3	TARTI, GÖMME TİP, DARBE EMİCİLİ, 3 TON KAPASİTELİ	150*150	1
N4	KASA TAŞIMA ARABASI	60*90*85	4
N5	HİJYEN BARİYERİ		1
N6	SİNEK ÖLDÜRÜCÜ, PASLANMAZ	100 m2	1
N7	YER IZGARASI, İZOLASYONLU	30*30*15	1
ÇÖP SOĞUK ODASI			
N1	PANEL TİP SOĞUK ODA, ZEMİNSİZ	560*300*270	1
N2	ÇÖP ARABASI	400 lt	16
N3	YER IZGARASI, İZOLASYONLU	30*30*15	1

FABRİKA AKADEMİ
BODRUM KAT | HAZIRLIK VE DEPOLAMA

DESIGNED/ TASARIM	ADEM AKPINAR
DRAWN/ ÇİZEN	ADEM AKPINAR
CHECKED/ KONTROL	ADEM AKPINAR
DATE/ TARİH	02.01.2026
REV. DATE / REV. TARİHİ	23.03.2026 / 26.01.2026
SCALE / ÖLÇEK	1/50 (A0)

Sktürk
ÇAĞLAYAN MAH. FEVZİ ÇAKMAK CAD. NO: 67/B
KAĞITHANE/ İSTANBUL
p:0212 909 4312
w: skturk.com.tr | e: info@skturk.com.tr

2026-080-5

THIS DRAWING REMAINS THE PROPERTY OF SKTÜRK ENDÜSTRİYEL MUTFAK SAN. VE TİC. LTD. ŞTİ. AND MAY ONLY BE COPIED COMPLETELY OR PARTLY OR ISSUED TO THIRD PARTY WITH OUR PRIOR CONSENT.
BU RESİM SKTÜRK ENDÜSTRİYEL MUTFAK SAN. VE TİC. LTD. ŞTİ'NİN MALI OLUP YAZILI İZİN OLMADIKÇA KISMEN VEYA TAMAMEN KOPYA EDİLEMEZ VE ÜÇÜNCÜ ŞAHISLARA VERİLEMEZ.