


FELAH SOKAK

ARAÇ GİRİŞİ

BİNA GİRİŞİ

ARAÇ ÇIKIŞI

MAL GİRİŞİ

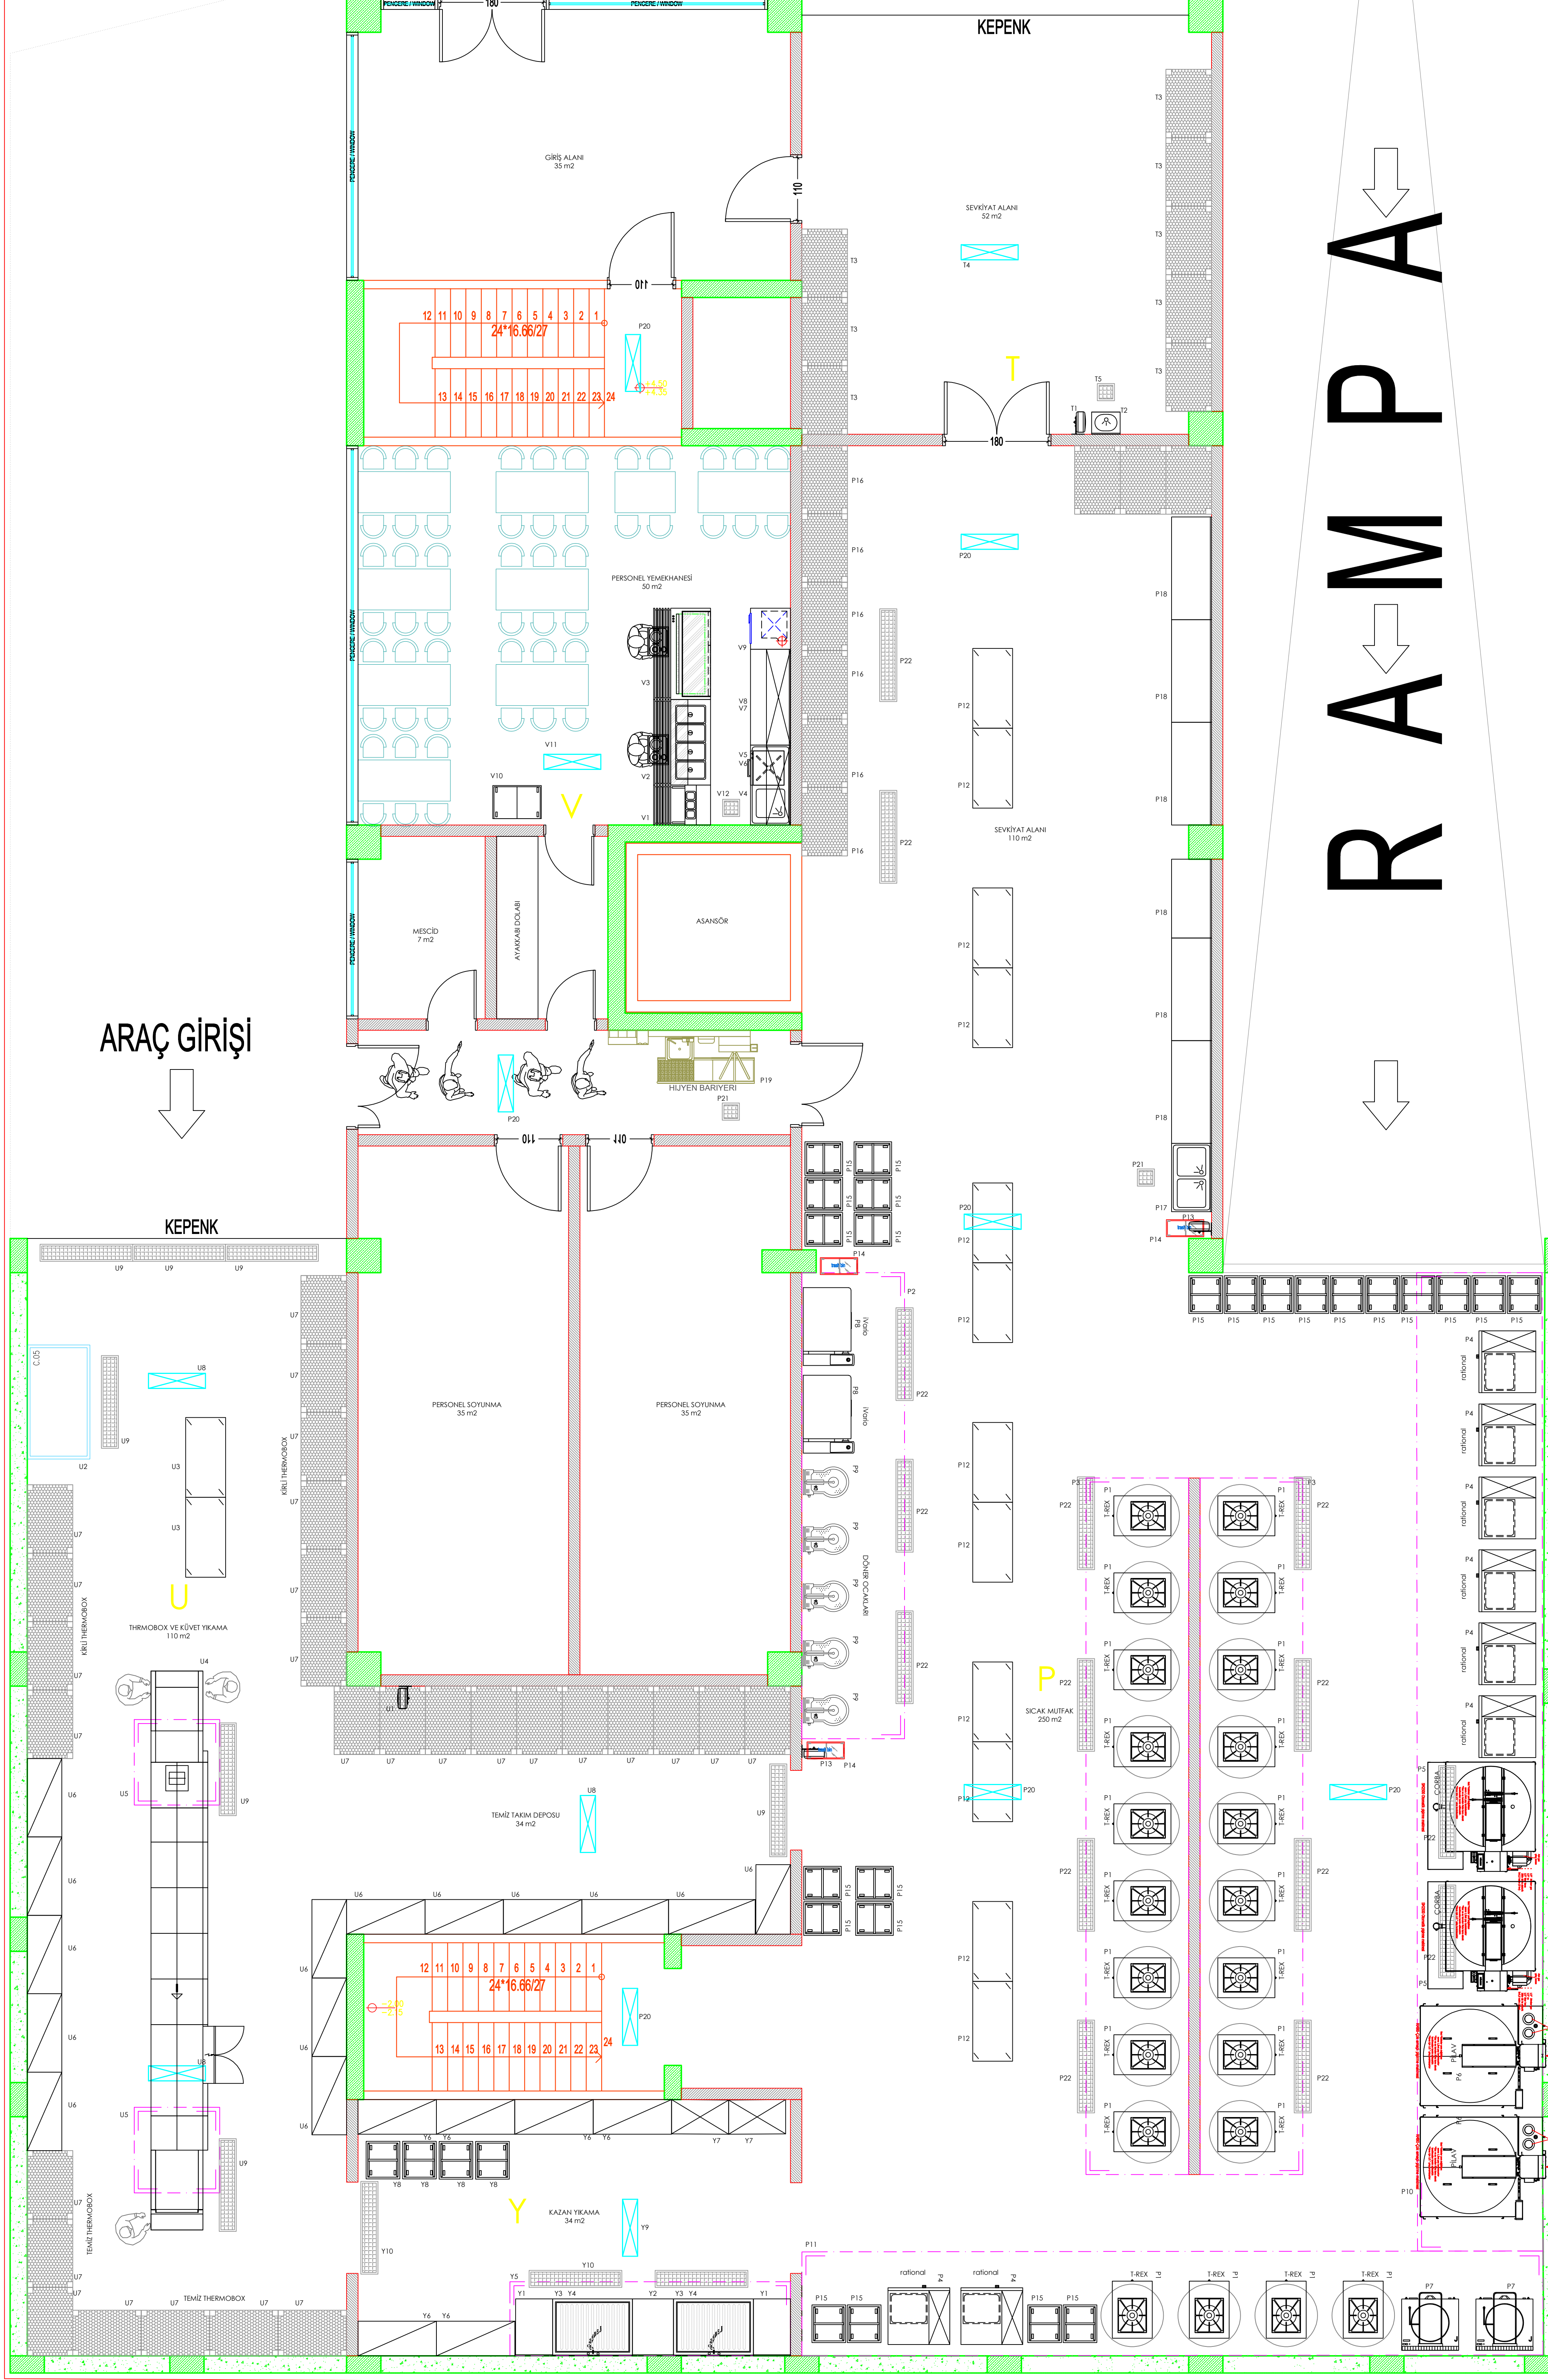

P.NO	BİRİM ADI	ÖLÇÜ	AD.
P- Sıcak Mutfak			
P1	YER OCAĞI	125*80*50	20
P2	DAVULBAZ, DUVAR TİPİ, FİLTRELİ	100*180*50	1
P3	DAVULBAZ, DUVAR TİPİ, FİLTRELİ	130*180*50	2
P4	RATİONAL YEMEK FIRINI, GAZLI	20 GN2/1	8
P5	CORBA PİŞİRME MAKİNASI	190*190*160	2
P6	PLAT PİŞİRME MAKİNASI	170*130*130	2
P7	KATNATMA KAZANI	400*1	2
P8	VARIO	-	2
P9	DOĞRUK OCAĞI, GAZLI, ARABALI	-	5
P10	DAVULBAZ, DUVAR TİPİ, FİLTRELİ	1720*220*50	1
P11	DAVULBAZ, DUVAR TİPİ, FİLTRELİ	1300*180*50	1
P12	HAREKETLİ ÇALIŞMA TEZGAHI, TABAN VE ARA RAFLI	140*70*85	12
P13	ÇÖP KOVASI, ARABALI	100*1	3
P14	YER YIKAMA HORTUMU	10 m	2
P15	GASTRONOM TEPSİ TAŞIMA ARABASI, GN 2/1	44*63*172	15
P16	PALET	120*80*15	6
P17	ÇİFT EVVELİ ÇALIŞMA TEZGAHI	70*70*85	1
P18	ÇALIŞMA TEZGAHI, TABAN VE ARA RAFLI	180*70*85	2
P19	HÜYEN BARIYERİ	-	1
P20	SİNEK ÖLDÜRÜCÜ, PASLANMAZ	100 m2	5
P21	YER İZGARASI, İZOLASYONLU	165*30*15	20
T- SEVKİYAT ALANI			
T1	YER YIKAMA HORTUMU	10 m	1
T2	DİZDEN KUMANDALI EL YIKAMA LAVABOSU	-	1
T3	PALET	120*80*15	8
T4	SİNEK ÖLDÜRÜCÜ, PASLANMAZ	100 m2	1
T5	YER İZGARASI, İZOLASYONLU	30*30*15	1
U- BULAŞIK YIKAMA & TEMİZ TAKIM ALANI			
U1	YER YIKAMA HORTUMU	10 m	1
U2	SU KAZANI, İSTİMALİ	180*80*85	1
U3	HAREKETLİ ÇALIŞMA TEZGAHI, TABAN VE ARA RAFLI	140*70*85	1
U4	BULAŞIK YIKAMA MAKİNASI, KONVEYÖRLÜ	980 cm	1
U5	DAVULBAZ, ORTA TİP	120*120*50	2
U6	İTİP RAFLI 4 KATLI	152*53*213	14
U7	PALET	120*80*15	27
U8	SİNEK ÖLDÜRÜCÜ, PASLANMAZ	100 m2	3
U9	YER İZGARASI, İZOLASYONLU	165*30*15	7
Y- KAZAN YIKAMA			
Y1	ÇALIŞMA TEZGAHI	65*80*57/9	2
Y2	ÇALIŞMA TEZGAHI	130*80*57/9	1
Y3	KAZAN YIKAMA EVİTESİ	140*80*57/9	2
Y4	ÖN YIKAMA DÜZÜ, DUVARA MONTE	-	2
Y5	DAVULBAZ, DUVAR TİPİ	500*130*50	1
Y6	İTİP RAFLI 4 KATLI	152*53*213	6
Y7	KİPÇE AKRI DOLABI	120*60*160	2
Y8	GASTRONOM TEPSİ TAŞIMA ARABASI, GN 2/1	44*63*172	4
Y9	SİNEK ÖLDÜRÜCÜ, PASLANMAZ	100 m2	1
Y10	YER İZGARASI, İZOLASYONLU	165*30*15	4
V- PERSONEL YEMEKHANESİ			
V1	KÜVER UNİTESİ, KAYIRMA STANDLI, MOBİLYALI	70*70*85/160	1
V2	BAHAMİRE 4 GN 1/1 KAYIRMA ST. MOBİLYALI	150*70*85/160	1
V3	KULE TİPİ SOĞUK DOLAP, KAYIRMA ST. MOBİLYALI	140*70*160	1
V4	TEK EVVELİ ÇALIŞMA TEZGAHI, DOLAPLI	140*70*85	1
V5	BULAŞIK YIKAMA MAKİNASI, SETLİ	500*160	1
V6	ÇALIŞMA TEZGAHI, TABAN VE ARA RAFLI DOLAPLI	160*70*85	1
V7	İKİ TİP BUZDOLABI, TEK KAPLI	70*70*205	1
V8	TEPSİ TOPLAMA ARABASI, 37*53	15*15	1
V9	SİNEK ÖLDÜRÜCÜ, PASLANMAZ	100 m2	1
V10	YER İZGARASI, İZOLASYONLU	30*30*15	1

+4.50 KOTU ZEMİN KAT PLANI (1/50)