
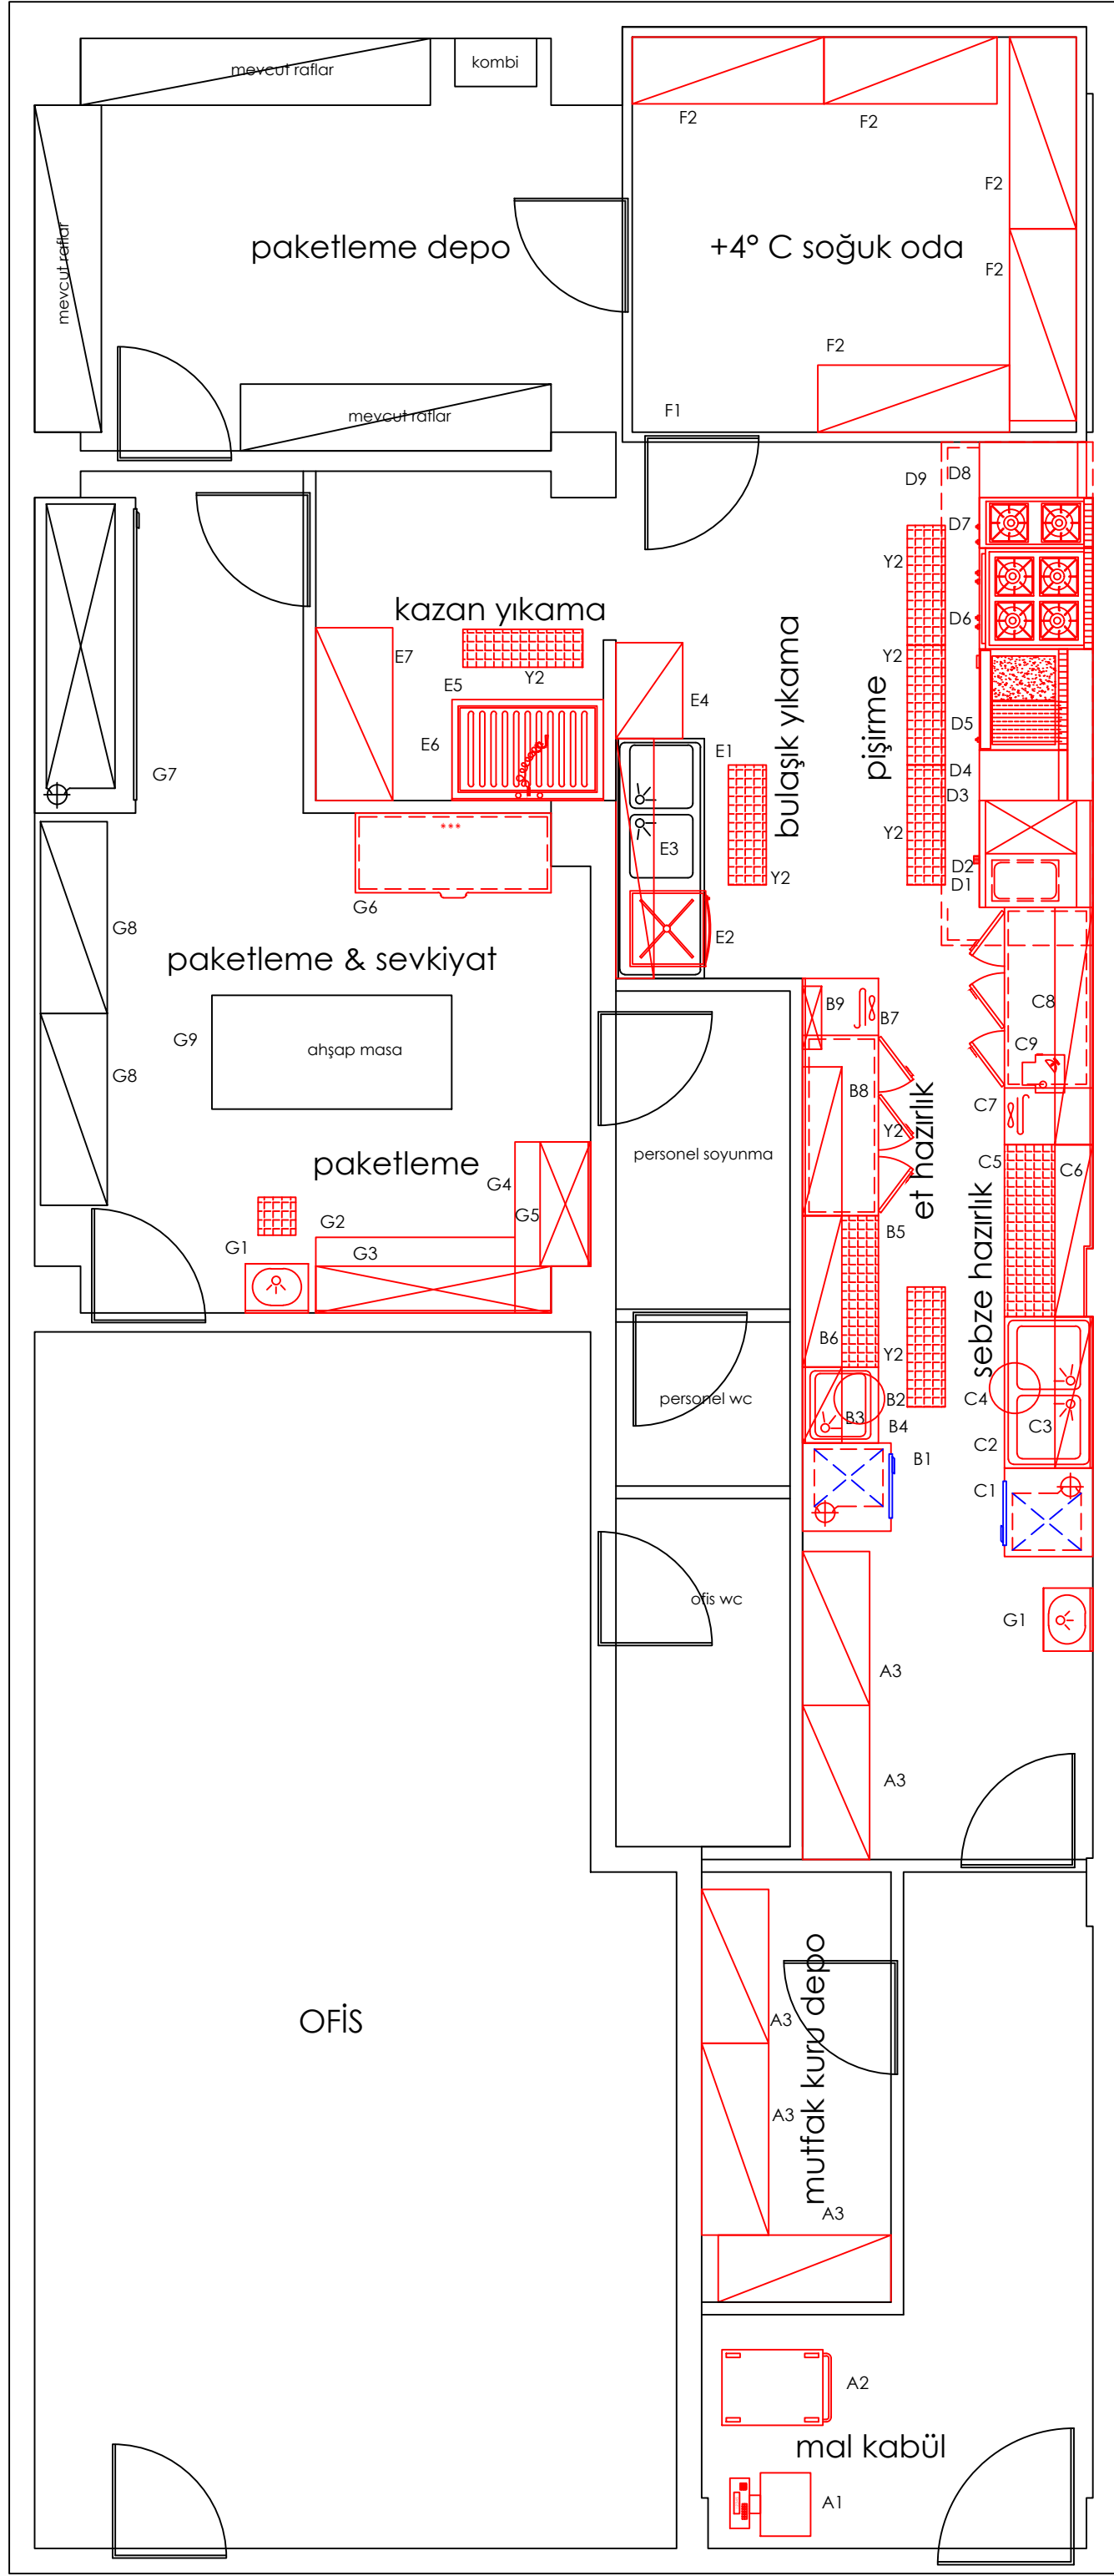


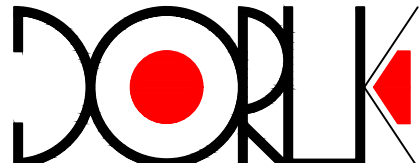

POZ.	MARKA	ÜRÜN AÇIKLAMASI	ÖLÇÜ/KAPASİTE	ADET
A- MAL KABÜL & KURU DEPO				
A1		TARTI	300 kg	1
A2		SERVİS ARABASI	85*60*85	1
A3		İSTİF RAFI, DEMONTE, 4 KATLI	152*53*160	5
B- ET HAZIRLIK				
B1		DEPO TİPİ BUZDOLABI, TEK KAPILI	70*70*205	1
B2		TEK EVYELİ ÇALIŞMA TEZGAHI	60*60*85	1
B3		DUVAR RAFI	60*30*4	1
B4		ÇÖP ARABASI	40*50	1
B5		POLİETİLEN TABLALI ÇALIŞMA TEZGAHI, TABAN RAFLI, ÇEKMECELİ	120*60*85	1
B6		DUVAR RAFI	120*30*4	1
B7		TEZGAH TİPİ BUZDOLABI, 3 KAPILI	186*60*85	1
B8		DUVAR RAFI	120*30*4	1
B9		BIÇAK STERİL DOLABI	10 BIÇAKLIK	1
C- SEBZE HAZIRLIK				
C1		DEPO TİPİ BUZDOLABI, TEK KAPILI	70*70*205	1
C2		ÇİFT EVYELİ ÇALIŞMA TEZGAHI	120*60*85	1
C3		DUVAR RAFI	120*30*4	1
C4		ÇÖP ARABASI	40*50	1
C5		POLİETİLEN TABLALI ÇALIŞMA TEZGAHI, TABAN RAFLI, ÇEKMECELİ	120*60*85	1
C6		DUVAR RAFI	120*30*4	1
C7		TEZGAH TİPİ BUZDOLABI, 3 KAPILI	186*60*85	1
C8		DUVAR RAFI	186*30*4	1
C9		SEBZE DOĞRAMA MAKİNASI	CL 50	1
D- PİŞİRME				
D1		FIRIN TEZGAHI, TEPŞİ RAYLI	100*90*85	1
D2		YEMEK FIRINI, GAZLI	10 GN 1/1	1
D3		ÇİHAZALTI ÇALIŞMA TEZGAHI, TABAN RAFLI	120*70*55	1
D4		NÖTR ARA TEZGAH, SETÜSTÜ	40*70*30	1
D5		IZGARA, GAZLI, SETÜSTÜ	80*70*30	1
D6		4 AÇIK ALEVLİ OCAK, GAZLI, DOLAPLI	80*90*85	1
D7		2 AÇIK ALEVLİ OCAK, GAZLI, DOLAPLI	40*90*85	1
D8		NÖTR ARA TEZGAH, DOLAPLI	40*90*85	1
D9		DAVLUMBAZ, DUVAR TİPİ, FİLTRELİ	400*117*50	1
E- BULAŞIK VE KAZAN YIKAMA				
E1		ÇİFT EVYELİ ÇALIŞMA TEZGAHI	190*70*85	1
E2		BULAŞIK YIKAMA MAKİNASI, SETALTI	500 TB/S	1
E3		DUVAR RAFI	190*30*4	1
E4		İSTİF RAFI, DEMONTE, 4 KATLI	76*53*160	1
E5		KAZAN YIKAMA EVYESİ	120*80*57/91	1
E6		ÖN YIKAMA DUŞU	duvara monte	1
E7		İSTİF RAFI, DEMONTE, 4 KATLI	122*61*160	1
F- SOĞUK ODA				
F1		PANEL TİP SOĞUK ODA	370*330*240	1
F2		İSTİF RAFI, DEMONTE, 4 KATLI	152*53*160	5
G- PAKETLEME & SEVKİYAT				
G1		DİZDEN KUMANDALI EL YIKAMA LAVABOSU	40*30*40	2
G2		ÇALIŞMA TEZGAHI, TABAN VE ARA RAFLI	180*60*85	1
G3		DUVAR DOLABI	190*40*60	1
G4		ÇALIŞMA TEZGAHI, TABAN VE ARA RAFLI	150*60*85	1
G5		DUVAR DOLABI	100*40*60	1
G6		BLOK KAPAKLI DERİN DONDURUCU	500 lt.	1
G7		SOĞUK DOLAP, CAMLI, SÜRGÜLÜ	-	1
G8		İSTİF RAFI, DEMONTE, 4 KATLI	-	2
G9		ÇALIŞMA TEZGAHI, AHŞAP	-	1

BROSSLIFE BAR VE MUTFAK PROJESİ				
DESIGNED BY/DİZAYN EDEN		ADEM AKPINAR		2017-109
DRAWN BY/ÇİZEN		ÇAĞLA KAYIKÇI		
CHECKED BY /KONTROL EDEN		ADEM AKPINAR		
DATE /TARİH		15.06.2017		
REVISION DATE REVİZYON TARİHİ		SCALE/ÖLÇEK	MERKEZ MAH. DUMLUPINAR CAD NO: 6/B KAĞITHANE/ İSTANBUL p: 0212 909 4312 m: 0554 237 8532 w: info@skturk.com.tr e: info@skturk.com.tr	
00.00.0000		1/50		
THIS DRAWING REMAINS THE PROPERTY OF DORUK ENDÜSTRİYEL MUTFAK ŞİRKETİ AND MAY ONLY BE COPIED COMPLETELY OR PARTY OR ISSUED TO THIRD PARTY WITH OUR PRIOR CONSENT.				
BU RESİM DORUK ENDÜSTRİYEL MUTFAK ŞİRKETİ'NİN MALI OLUP YAZILI MÜSAADE OLMADIĞKA KISMEN VEYA TAMAMEN KOPYA EDİLEMEZ VE ÜÇÜNCÜ SAHİSLARA VERİLEMEZ.				