


GLORIA JEANS COFFEES

SHEET NAME PAFTA ADI	MUTFAK PLANI
SHEET NO PAFTA NUMARASI	UBN_GJC_P9_SUP_01
PROJECT NAME PROJE ADI	YENİHAVALIMANI
SCALE ÖLÇEK	1/50
DESIGNED BY TASARLAYAN	UBAN MİMARLIK
DRAWN BY ÇİZEN	BANU ORUÇ
CHECKED by KONTROL	TUBA ORUÇ
DATE TARİH	14.11.2018

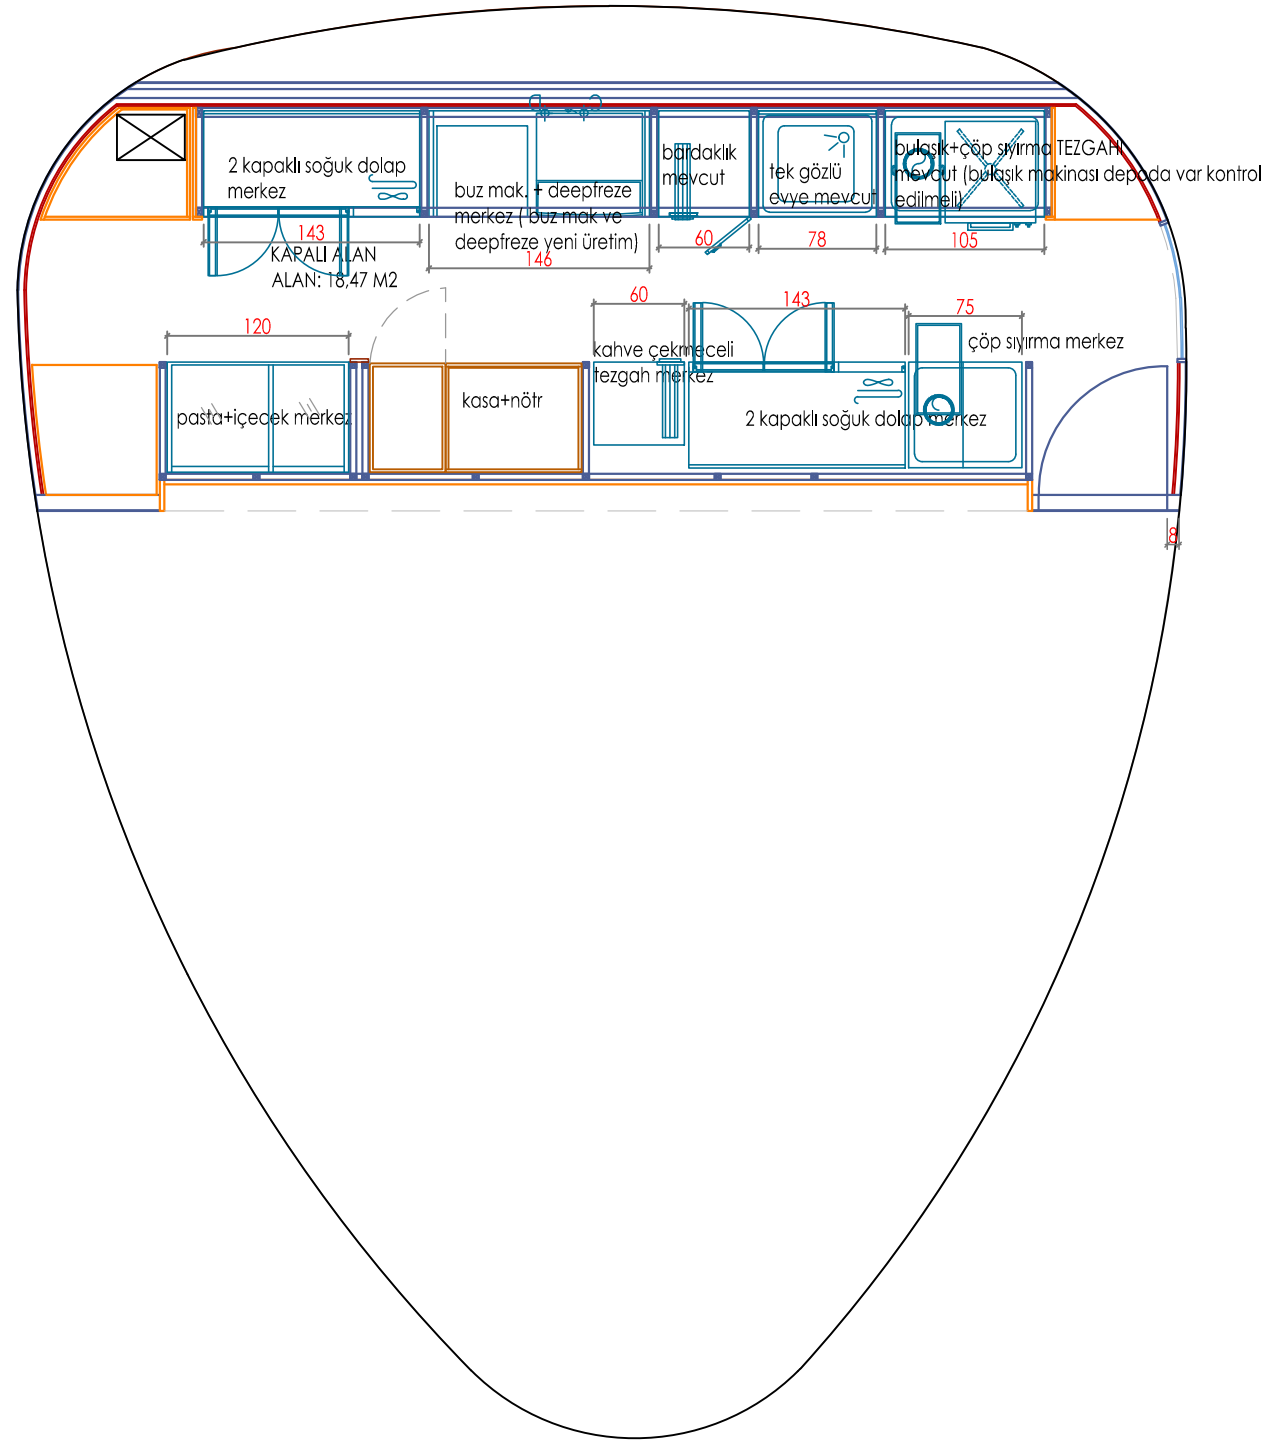

DATE	DESCRIPTION	BY

- No changes can be made in the project and application without permission from the project group.
- Report all errors and omissions to the Architect
- Dimensions to be checked on site before fabrication
- All dimensions are in centimeters