


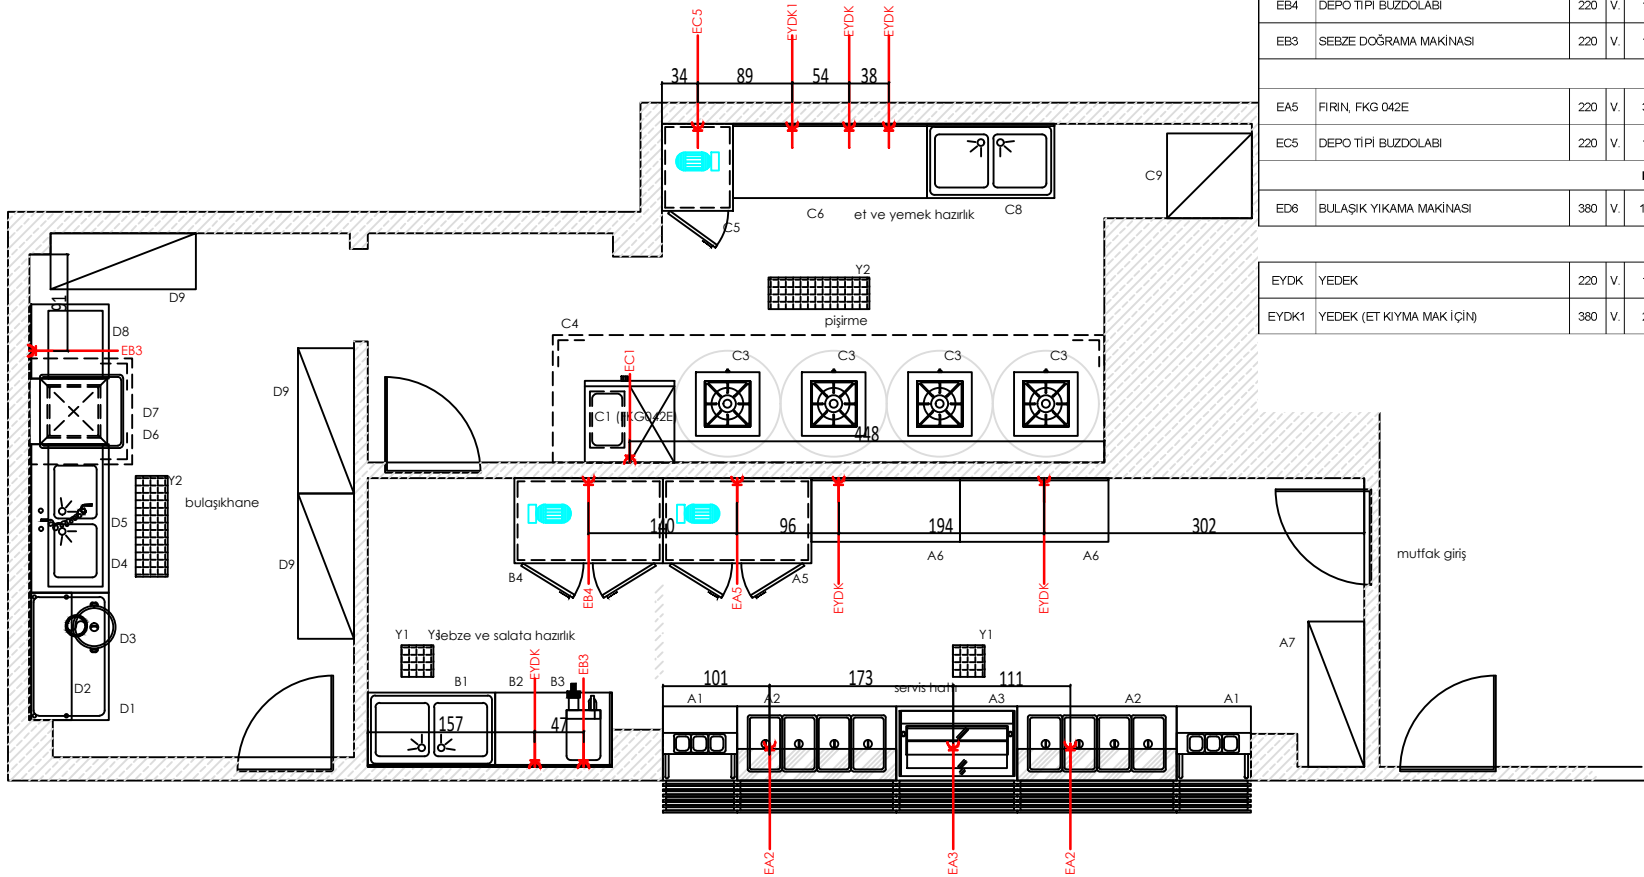

ELEKTRİK TESİSATI								
S.NO	ÜRÜN	220 / 380	V.	KW.	AÇIKLAMA	AD.	TOPLAM KW.	
BAINMAIRIE HATTI								
EA2	BAINMARIE	220	V.	1,0	KW	H: 10 CM 2 MT. KABLO UCU TOPRAKLI PRİZ BIRAKINIZ	2	2
EA3	KULE TİP SOĞUK DOLAP	220	V.	1,0	KW	H: 10 CM 2 MT. KABLO UCU TOPRAKLI PRİZ BIRAKINIZ	1	1
EA5	DEPO TİPİ BUZDOLABI	220	V.	1,0	KW	H: 190 CM TOPRAKLI PRİZ BIRAKINIZ	1	1
SEBZE HAZIRLIK								
EB3	SEBZE DOĞRAMA MAKİNASI	220	V.	1,0	KW	H: 100 CM TOPRAKLI PRİZ BIRAKINIZ	1	1
EB4	DEPO TİPİ BUZDOLABI	220	V.	1,0	KW	H: 190 CM TOPRAKLI PRİZ BIRAKINIZ	1	1
EB3	SEBZE DOĞRAMA MAKİNASI	220	V.	1,0	KW	H: 100 CM TOPRAKLI PRİZ BIRAKINIZ	1	1
PIŞIRME								
EA5	FIRIN, FKG 042E	220	V.	3,0	KW	H= 110 cm TOPRAKLI PRİZ BIRAKINIZ	1	3
EC5	DEPO TİPİ BUZDOLABI	220	V.	1,0	KW	H: 190 CM TOPRAKLI PRİZ BIRAKINIZ	1	1
BULAŞIKHANE								
ED6	BULAŞIK YIKAMA MAKİNASI	380	V.	10,0	KW	H: 45 CM 2 MT. KABLO UCU BIRAKINIZ	1	10
EYDK	YEDEK	220	V.	1,0	KW	H: 100 CM TOPRAKLI PRİZ BIRAKINIZ	5	5
EYDK1	YEDEK (ET KIYMA MAK İÇİN)	380	V.	2,0	KW	H: 100 CM 2 MT KABLO UCU BIRAKINIZ	1	2

ÇAM KOLEJİ KARTAL									
BAR VE MUTFAK PROJESİ									
DESIGNED/ TASARIM				ADEM AKPINAR			 MALTEPE MAH. DAVUTPAŞA CAD. YILDIZ SOK. NO: 6/ A DAVUTPAŞA/ ZEYİTBURNU/ İSTANBUL p: 0212 909 4312 w: skturk.com.tr e: info@skturk.com.tr		
DRAWN/ ÇİZEN				ADEM AKPINAR					
CHECKED/ KONTROL				ADEM AKPINAR					
DATE/ TARİH				2.7.2019					
REV. DATE		REV. TARİHİ		00.00.0000		SCALE		1/50 (A3)	
THIS DRAWING REMAINS THE PROPERTY OF SKTÜRK ENDÜSTRİYEL MUTFAK SAN. VE TİC. LTD. ŞTİ. AND MAY ONLY BE COPIED COMPLETELY OR PARTLY OR ISSUED TO THIRD PARTY WITH OUR PRIOR CONSENT. BU RESİM SKTÜRK ENDÜSTRİYEL MUTFAK SAN. VE TİC. LTD. ŞTİ.'NİN MALİ OLUP VAZİRLİĞİN OLMAĞI KİMLERİN KOPYA YAPMAMASINI VE ÜÇÜNCÜ SAHİPLERİNE VERİLMESİNİ İSTİYORUZ.									
2019-078									

2019-078