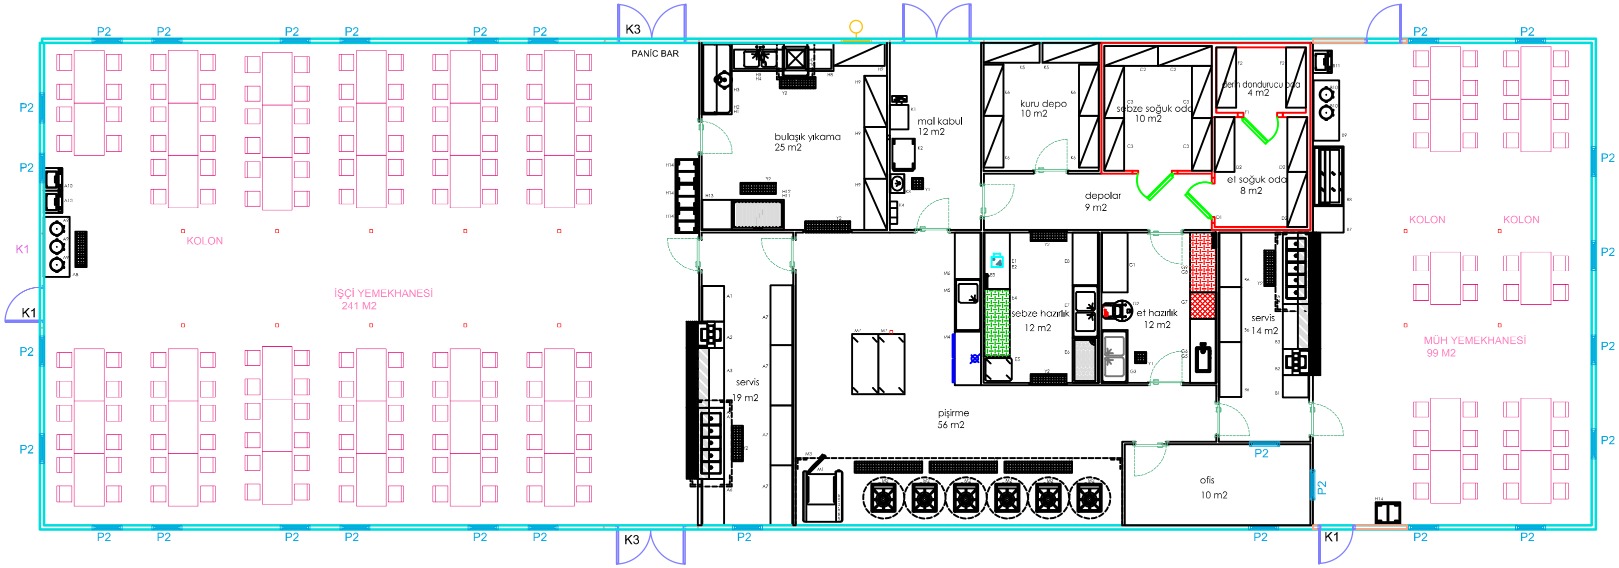

P.NO	ÜRÜN ADI	ÖLÇÜ	AD.
İŞÇİ YEMEKHANESİ			
K- KİLER + SARF DEPO + PERSONEL GİRİŞ			
K1	TARTI	300 kg	1
K2	SERVİS ARABASI, 2 KATLI	90*60*90	1
K3	DİZDEN KUMANDALI EL YIKAMA LAVABOSU	-	1
K4	BONE GALOŞLUK	-	1
K5	İSTİF RAFI, 4 KATLI	150*55*160	2
K6	İSTİF RAFI, 4 KATLI	140*55*160	4
C- SEBZE SOĞUK ODA			
C1	PANEL TİP SOĞUK ODA	-	1
C2	İSTİF RAFI, 4 KATLI	140*55*160	2
C3	İSTİF RAFI, 4 KATLI	140*55*160	4
D- ET SOĞUK ODA			
D1	PANEL TİP SOĞUK ODA	-	1
D2	İSTİF RAFI, 4 KATLI	140*55*160	3
F- ET DERİN DONDURUCU ODA			
F1	PANEL TİP DERİNDONDURUCU ODA	-	1
F2	İSTİF RAFI, 4 KATLI	160*55*160	2
G- ET HAZIRLIK			
G1	ÇALIŞMA TEZGAHI, TABAN RAFLI	160*70*85	1
G2	KÖFTE (HAMUR) YOĞURMA MAKİNASI	35 KG/sefer	1
G3	ÇİFT EVYELİ ÇALIŞMA TEZGAHI	140*70*85	1
G4	ÇALIŞMA TEZGAHI, TABAN RAFLI	60*70*85	1
G5	ÇALIŞMA TEZGAHI, TABAN RAFLI, ÇEKMECELİ	170*70*85	1
G6	ET KIYMA MAKİNASI	no: 32	1
G7	ET KÜTÜĞÜ	70*70*85	1
G8	POLİETİLEN TABLALI ÇALIŞMA TEZGAHI, TABAN RAFLI	160*70*85	1
G9	BIÇAK STERİL DOLABI	10 BIÇAKLIK	1
E- SEBZE HAZIRLIK			
E1	ÇALIŞMA TEZGAHI, TABAN RAFLI	150*70*85	1
E2	SEBZE DOĞRAMA MAKİNASI	200 kg/s	1
E3	BIÇAK STERİL DOLABI	10 BIÇAKLIK	1
E4	POLİETİLEN TABLALI ÇALIŞMA TEZGAHI, TABAN RAFLI, ÇEKMECELİ	180*70*85	1
E5	SEBZE BASMA-TAŞIMA ARABASI	60*50*70	1
E6	SEBZE BASMA-YIKAMA TEZGAHI	120*70*85	1
E7	ÇİFT EVYELİ ÇALIŞMA TEZGAHI	140*70*85	1
E8	ÇALIŞMA TEZGAHI, TABAN RAFLI	140*70*85	1
M- SICAK MUTFAK			
M1	KONVEKSİYONLU FIRIN, GAZLI	20 gn 2/1	1
M2	YER OCAĞI	60*80*50	6
M3	DAVLUMBAZ, DUVAR TİPİ, FİLTRELİ	870*150*50	1
M4	DEPO TİPİ BUZDOLABI, İKİ KAPILI	140*85*205	1
M5	TEK EVYELİ ÇALIŞMA TEZGAHI	140*70*85	1
M6	ÇALIŞMA TEZGAHI, TABAN VE ARA RAFLI	120*80*85	1
M7	HAREKETLİ ÇALIŞMA TEZGAHI, TABAN RAFLI	140*70*85	2
A- İŞÇİ SERVİS HATTI			
A1	ÇALIŞMA TEZGAHI, TABAN VE ARA RAFLI	95*60*85	1
A2	KUVER ÜNİTESİ	70*70*85/135	1
A3	NÖTR SERVİS TEZGAHI, SERVİS RAFLI	180*70*85/135	1
A4	SICAK YEMEK SERVİS ÜNİTESİ	190*70*85/135	1
A5	DAVLUMBAZ, ORTA TİP	260*110*50	1
A6	ÇALIŞMA TEZGAHI, TABAN VE ARA RAFLI	125*60*85	1
A7	ÇALIŞMA TEZGAHI, TABAN VE ARA RAFLI, DOLAPLI	190*60*85	4
A8	ÇALIŞMA TEZGAHI, TABAN VE ARA RAFLI	160*70*85	1
A9	ÇAY OYOMATI	50 lt.	3
A10	SU SEBİLİ	80 lt.	2
B- MÜHENDİS SERVİS HATTI			
B1	ÇALIŞMA TEZGAHI, TABAN VE ARA RAFLI	60*60*85	11
B2	KUVER ÜNİTESİ	70*70*85/135	1
B3	NÖTR SERVİS TEZGAHI, SERVİS RAFLI	120*70*85/135	4
B4	SICAK YEMEK SERVİS ÜNİTESİ	190*70*85/135	1
B5	DAVLUMBAZ, ORTA TİP	260*110*50	1
B6	ÇALIŞMA TEZGAHI, TABAN VE ARA RAFLI, DOLAPLI	160*60*85	3
B7	ÇALIŞMA TEZGAHI, TABAN VE ARA RAFLI	110*80*85	1
B8	SALATBAR, DUVAR TİPİ, DEPOSUZ	160*70*160	1
B9	ÇALIŞMA TEZGAHI, TABAN VE ARA RAFLI, DOLAPLI	160*70*85	1
B10	ÇAY OYOMATI	50 lt.	2
B11	SU SEBİLİ	80 lt.	2
P- BULAŞIKHANE			
P1	SIYIRMA TEZGAHI	190*80*85	1
P2	BASKET RAFI	190*40*60	1
P3	ÇÖP ARABASI	70*60*50	1
P4	ÇİFT EVYELİ BYM GİRİŞ TEZGAHI	160*75*85	1
P5	ÖN YIKAMA DUŞU	-	1
P6	BULAŞIK YIKAMA MAKİNASI, GİYOTİN TİP	1000 TB/S	1
P7	DAVLUMBAZ, DUVAR TİPİ	100*97*50	1
P8	BYM ÇIKIŞ TEZGAHI	70*75*85	1
P9	İSTİF RAFI, 4 KATLI	150*60*160	4
P10	KAZAN YIKAMA EVYESİ	150*80*[illegible]	1
P11	ÖN YIKAMA DUŞU, DUVARA MONTE	-	1
P12	ÇALIŞMA TEZGAHI	80*80*57/91	1
P13	TEPSİ TOPLAMA ARABASI, ÇİFTLİ	37*53 15 KATLI	4
Y- YER IZGARASI			
Y1	YER IZGARASI	30*30*14	2
Y2	YER IZGARASI	120*30*14	7
Y3	YER IZGARASI	186*30*14	3

TAŞYAPI | BURSA | İŞÇİ YEMEKHANESİ

BAR VE MUTFAK PROJESİ

DESIGNED/ TASARIM	ADEM AKPINAR
DRAWN/ ÇİZEN	ADEM AKPINAR
CHECKED/ KONTROL	ADEM AKPINAR
DATE/ TARİH	3.2.2021
REV. DATE REV. TARİHİ	00.00.0000
SCALE ÖLÇEK	1/50 (A0)

Sktürk
MALTEPE MAH. DAVUTPAŞA CAD. YILDIZ SOK. NO: 6/ A
DAVUTPAŞA/ ZEYTİNBURNU/ İSTANBUL
p: 0212 909 4312
w: skturk.com.tr | e: info@skturk.com.tr

2020-107-2

[illegible]