


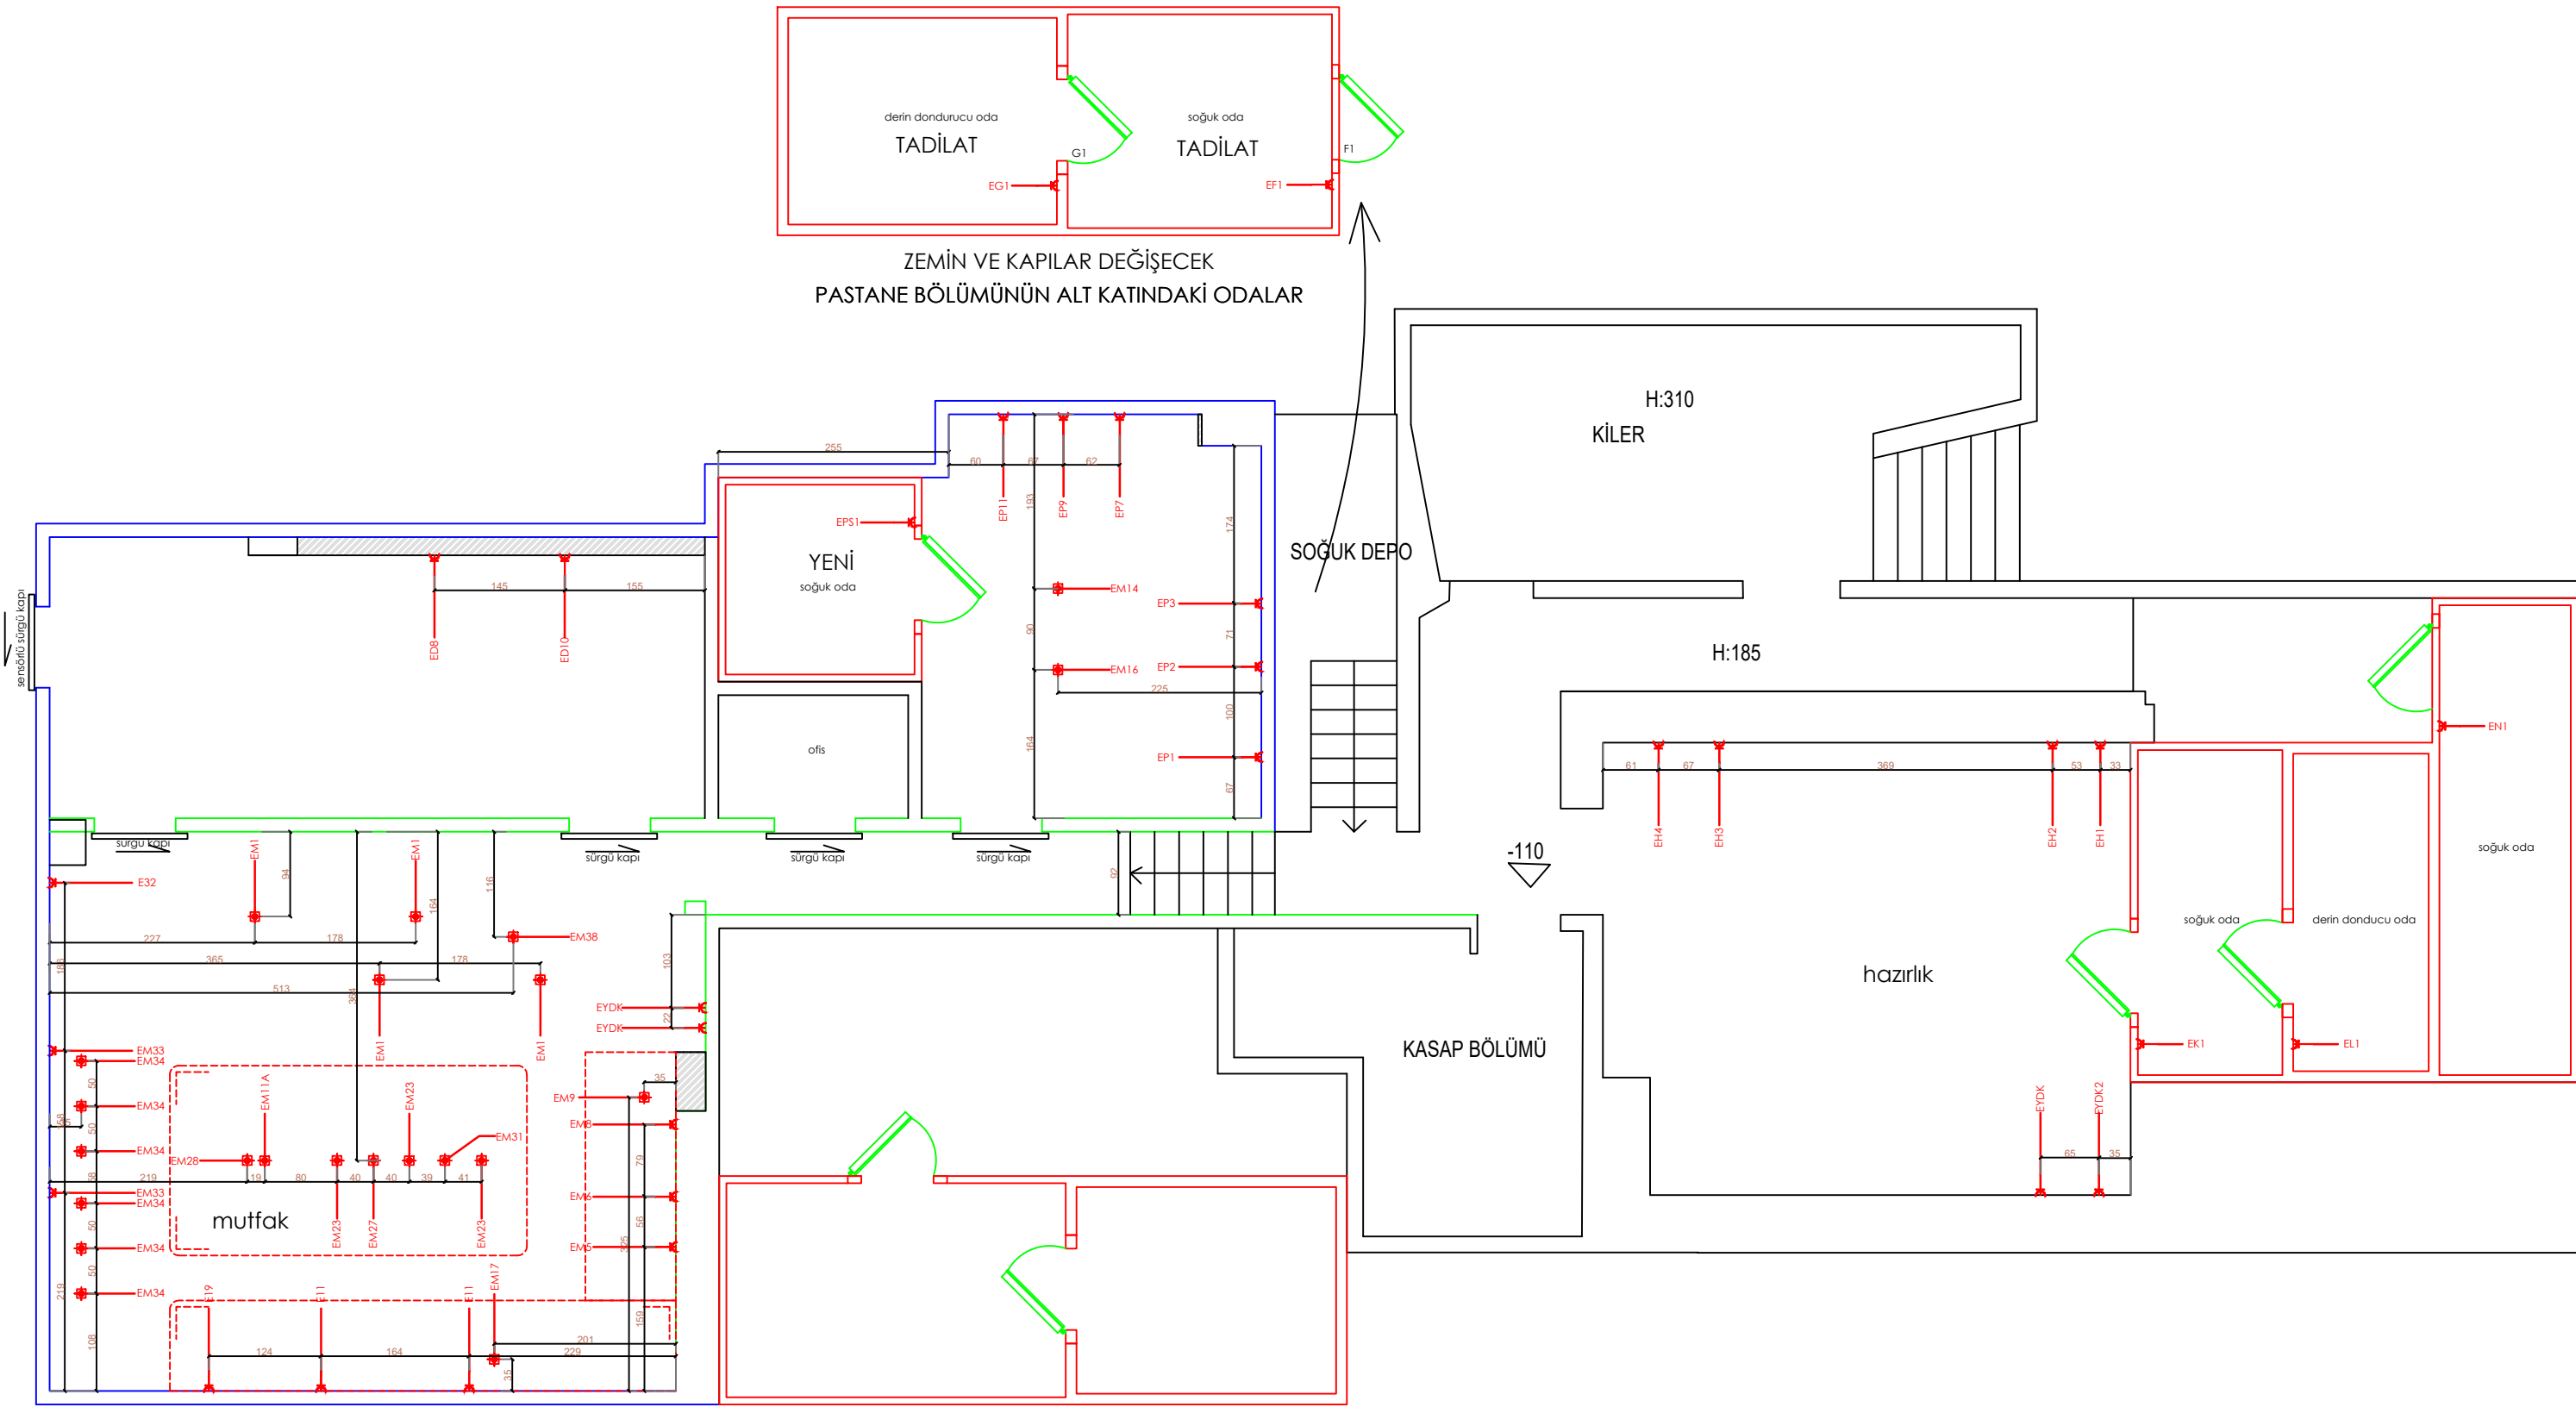

röleveden sonraki giriş kat komple revizyon

ELEKTRİK TEŞVİATİ								
S.NO	ÜRÜN	220 / 380	V	KW.	AÇIKLAMA	AD.	TOPLAM KW.	
M- MUTFAK								
EM1	MAKE-UP BUZDOLABI	220	V	1,0	KW	H: 45 CM TOPRAKLI PRİZ BİRAKINIZ.	4	4
EM5	CHAZALTI DERİN DONDURUCU	220	V	1,0	KW	H: 45 CM TOPRAKLI PRİZ BİRAKINIZ.	1	1
EM6	FRTÖZ	380	V	17,4	KW	H: 65 CM 2 MT. KABLO UCU BİRAKINIZ.	1	17,4
EM8	FRTÖZ	380	V	17,4	KW	H: 65 CM 2 MT. KABLO UCU BİRAKINIZ.	1	17,4
EM9	DAVLUMBAZ AYDINLATMASI	220	V	1,0	KW	TAVANDAN 2 MT KABLO UCU BİRAKINIZ.	1	1
EM11	CHAZALTI BUZDOLABI	220	V	1,0	KW	H: 45 CM TOPRAKLI PRİZ BİRAKINIZ.	2	2
EM11A	CHAZALTI BUZDOLABI	220	V	1,0	KW	H: 10 CM 1 MT. KABLO UCU'NA TOPRAKLI PRİZ BİRAKINIZ.	1	1
EM17	DAVLUMBAZ AYDINLATMASI	220	V	1,0	KW	TAVANDAN 2 MT KABLO UCU BİRAKINIZ.	1	1
EM10	YEMEK FIRINI - GAZLI	220	V	1,0	KW	H: 45 CM TOPRAKLI PRİZ BİRAKINIZ.	1	1
EM20	DAVLUMBAZ AYDINLATMASI	220	V	1,0	KW	TAVANDAN 2 MT KABLO UCU BİRAKINIZ.	1	1
EM23	CHAZALTI BUZDOLABI	220	V	1,0	KW	H: 10 CM 1 MT. KABLO UCU'NA TOPRAKLI PRİZ BİRAKINIZ.	3	3
EM27	MAKARNA PİSİRCİ	380	V	6,0	KW	H: 10 KABLO UCU'NA CM 2 MT. KABLO UCU BİRAKINIZ.	1	6
EM28	SALAMANDER	380	V	4,0	KW	H: 10 KABLO UCU'NA CM 2 MT. KABLO UCU BİRAKINIZ.	1	4
EM31	DAVLUMBAZ AYDINLATMASI	220	V	1,0	KW	TAVANDAN 2 MT KABLO UCU BİRAKINIZ.	1	1
EM32	TEZGAH TIRI BUZDOLABI	220	V	1,0	KW	H: 45 CM TOPRAKLI PRİZ BİRAKINIZ.	1	1
EM33	SICAK TABAK DOLABI	220	V	3,0	KW	H: 45 CM TOPRAKLI PRİZ BİRAKINIZ.	2	6
EM34	INFRARED ISITICI	220	V	1,0	KW	TAVANDAN 2 MT KABLO UCU BİRAKINIZ.	6	6
EM38	SİNEK ÖLDÜRÜCÜ	220	V	1,0	KW	TAVANDAN 2 MT KABLO UCU BİRAKINIZ.	1	1
BULAKSHANE								
ED8	KONVEYÖRLÜ BULAKŞI YIKAMA MAKİNASI	380	V	24,0	KW	H: 45 CM 2 MT. KABLO UCU BİRAKINIZ.	1	24
ED10	BARDAK YIKAMA MAKİNASI - YEDEK	380	V	6,0	KW	H: 45 CM 2 MT. KABLO UCU BİRAKINIZ.	1	6
PASTANE								
EP1	DEPO TIRI BUZDOLABI	220	V	1,0	KW	H: 180 CM TOPRAKLI PRİZ BİRAKINIZ.	1	1
EP2	HAMUR YOĞURMA MAK.	380	V	1,5	KW	H: 45 CM 2 MT. KABLO UCU BİRAKINIZ.	1	1,5
EP3	MAKE-UP BUZDOLABI	220	V	1,0	KW	H: 45 CM TOPRAKLI PRİZ BİRAKINIZ.	1	1
EP7	KITCHEN AID MİKSER	220	V	1,0	KW	H: 110 CM TOPRAKLI PRİZ BİRAKINIZ.	1	1
EP9	ELEKTRİKLI OCAK	380	V	6,0	KW	H: 65 CM 2 MT. KABLO UCU BİRAKINIZ.	1	6
EP11	YEMEK FIRINI - GAZLI	220	V	1,0	KW	H: 45 CM TOPRAKLI PRİZ BİRAKINIZ.	1	1
EP14	TEZGAH TIRI BUZDOLABI	220	V	1,0	KW	H: 10 CM 1 MT. KABLO UCU'NA TOPRAKLI PRİZ BİRAKINIZ.	1	1
EP15	BLOK KAPAKLI DERİN DONDURUCU	220	V	1,0	KW	H: 10 CM 1 MT. KABLO UCU'NA TOPRAKLI PRİZ BİRAKINIZ.	1	1
PASTANIE SOĞUK ODA								
PS1	SOĞUK ODA	380	V	4,0	KW	MOTORLUN ÇEKİLECEĞİ YERE 3 METRE KABLO UCU BİRAKINIZ.	1	4
PASTANIE ALTI SOĞUK ODA								
F1	SOĞUK ODA	380	V	4,0	KW	MOTORLUN ÇEKİLECEĞİ YERE 3 METRE KABLO UCU BİRAKINIZ.	1	4
PASTANIE ALTI DERİN DONDURUCU								
G1	DERİN DONDURUCU ODA	380	V	4,0	KW	MOTORLUN ÇEKİLECEĞİ YERE 3 METRE KABLO UCU BİRAKINIZ.	1	4
HAZIRLIK								
EH1	DEPO TIRI BUZDOLABI	220	V	1,0	KW	H: 180 CM TOPRAKLI PRİZ BİRAKINIZ.	1	1
EH2	MAKE-UP BUZDOLABI	220	V	1,0	KW	H: 45 CM TOPRAKLI PRİZ BİRAKINIZ.	1	1
EH3	QIDA DÜZLEME MAKİNASI	220	V	1,0	KW	H: 110 CM TOPRAKLI PRİZ BİRAKINIZ.	1	1
EH4	SERBEZ DOĞRAMA MAKİNASI	220	V	1,0	KW	H: 110 CM TOPRAKLI PRİZ BİRAKINIZ.	1	1
HAZIRLIK SOĞUK ODA								
K1	SOĞUK ODA	380	V	4,0	KW	MOTORLUN ÇEKİLECEĞİ YERE 3 METRE KABLO UCU BİRAKINIZ.	1	4
HAZIRLIK DERİN DONDURUCU ODA								
L1	DERİN DONDURUCU ODA	380	V	4,0	KW	MOTORLUN ÇEKİLECEĞİ YERE 3 METRE KABLO UCU BİRAKINIZ.	1	4
SOĞUK ODA								
N1	SOĞUK ODA	380	V	4,0	KW	MOTORLUN ÇEKİLECEĞİ YERE 3 METRE KABLO UCU BİRAKINIZ.	1	4
YEDEK								
EYD1	YEDEK	220	V	1,0	KW	H: 110 CM TOPRAKLI PRİZ BİRAKINIZ.	4	4
EYD2	YEDEK	220	V	1,0	KW	H: 180 CM TOPRAKLI PRİZ BİRAKINIZ.	2	2
NOT: MEVCUT ÜRÜNLER KATALOG DEĞERLERİ MUTLAKA KONTROL EDİLMELİDİR								

ELEKTRİK

NO:81 HOTEL BAR VE MUTFAK PROJESİ			
DESIGNED TASARIM	ADEM AKPINAR	 ÇAĞLAYAN MAH. FEVZİ ÇAKMAK CAD. NO: 67/B KAĞITHANE/ İSTANBUL p:0212 909 4312 w: skturk.com.tr e: info@skturk.com.tr	2022-009-7
DRAWN ÇİZİM	ADEM AKPINAR		
CHECKED KONTROL			
DATE/ TARİH	4.2.2022		
REVİZYON	08.03.2023 27.03.2023 11.03.2022	SCALE	1/50 (A1)
THIS DRAWING REMAINS THE PROPERTY OF SKTURK ENGINEERING MUTFAK SAN. VE TIC. LTD. ŞTİ. AND MAY ONLY BE CORRECTED COMPLETELY OR PARTLY OR LOANED TO THIRD PARTY WITHOUT PRIOR CONSENT. BU ÇİZİM MUTFAK ENGINEERING MUTFAK SAN. VE TIC. LTD. ŞTİ. MİLMALLIĞI ÜP KAPALI TUTULMUŞTUR. KİMYENİ VEYA TAVANININ KOPYA YAPILMASI VE ÜÇÜNCÜ ŞAHİSLARA VERİLMESİ YASAKTIR.			