


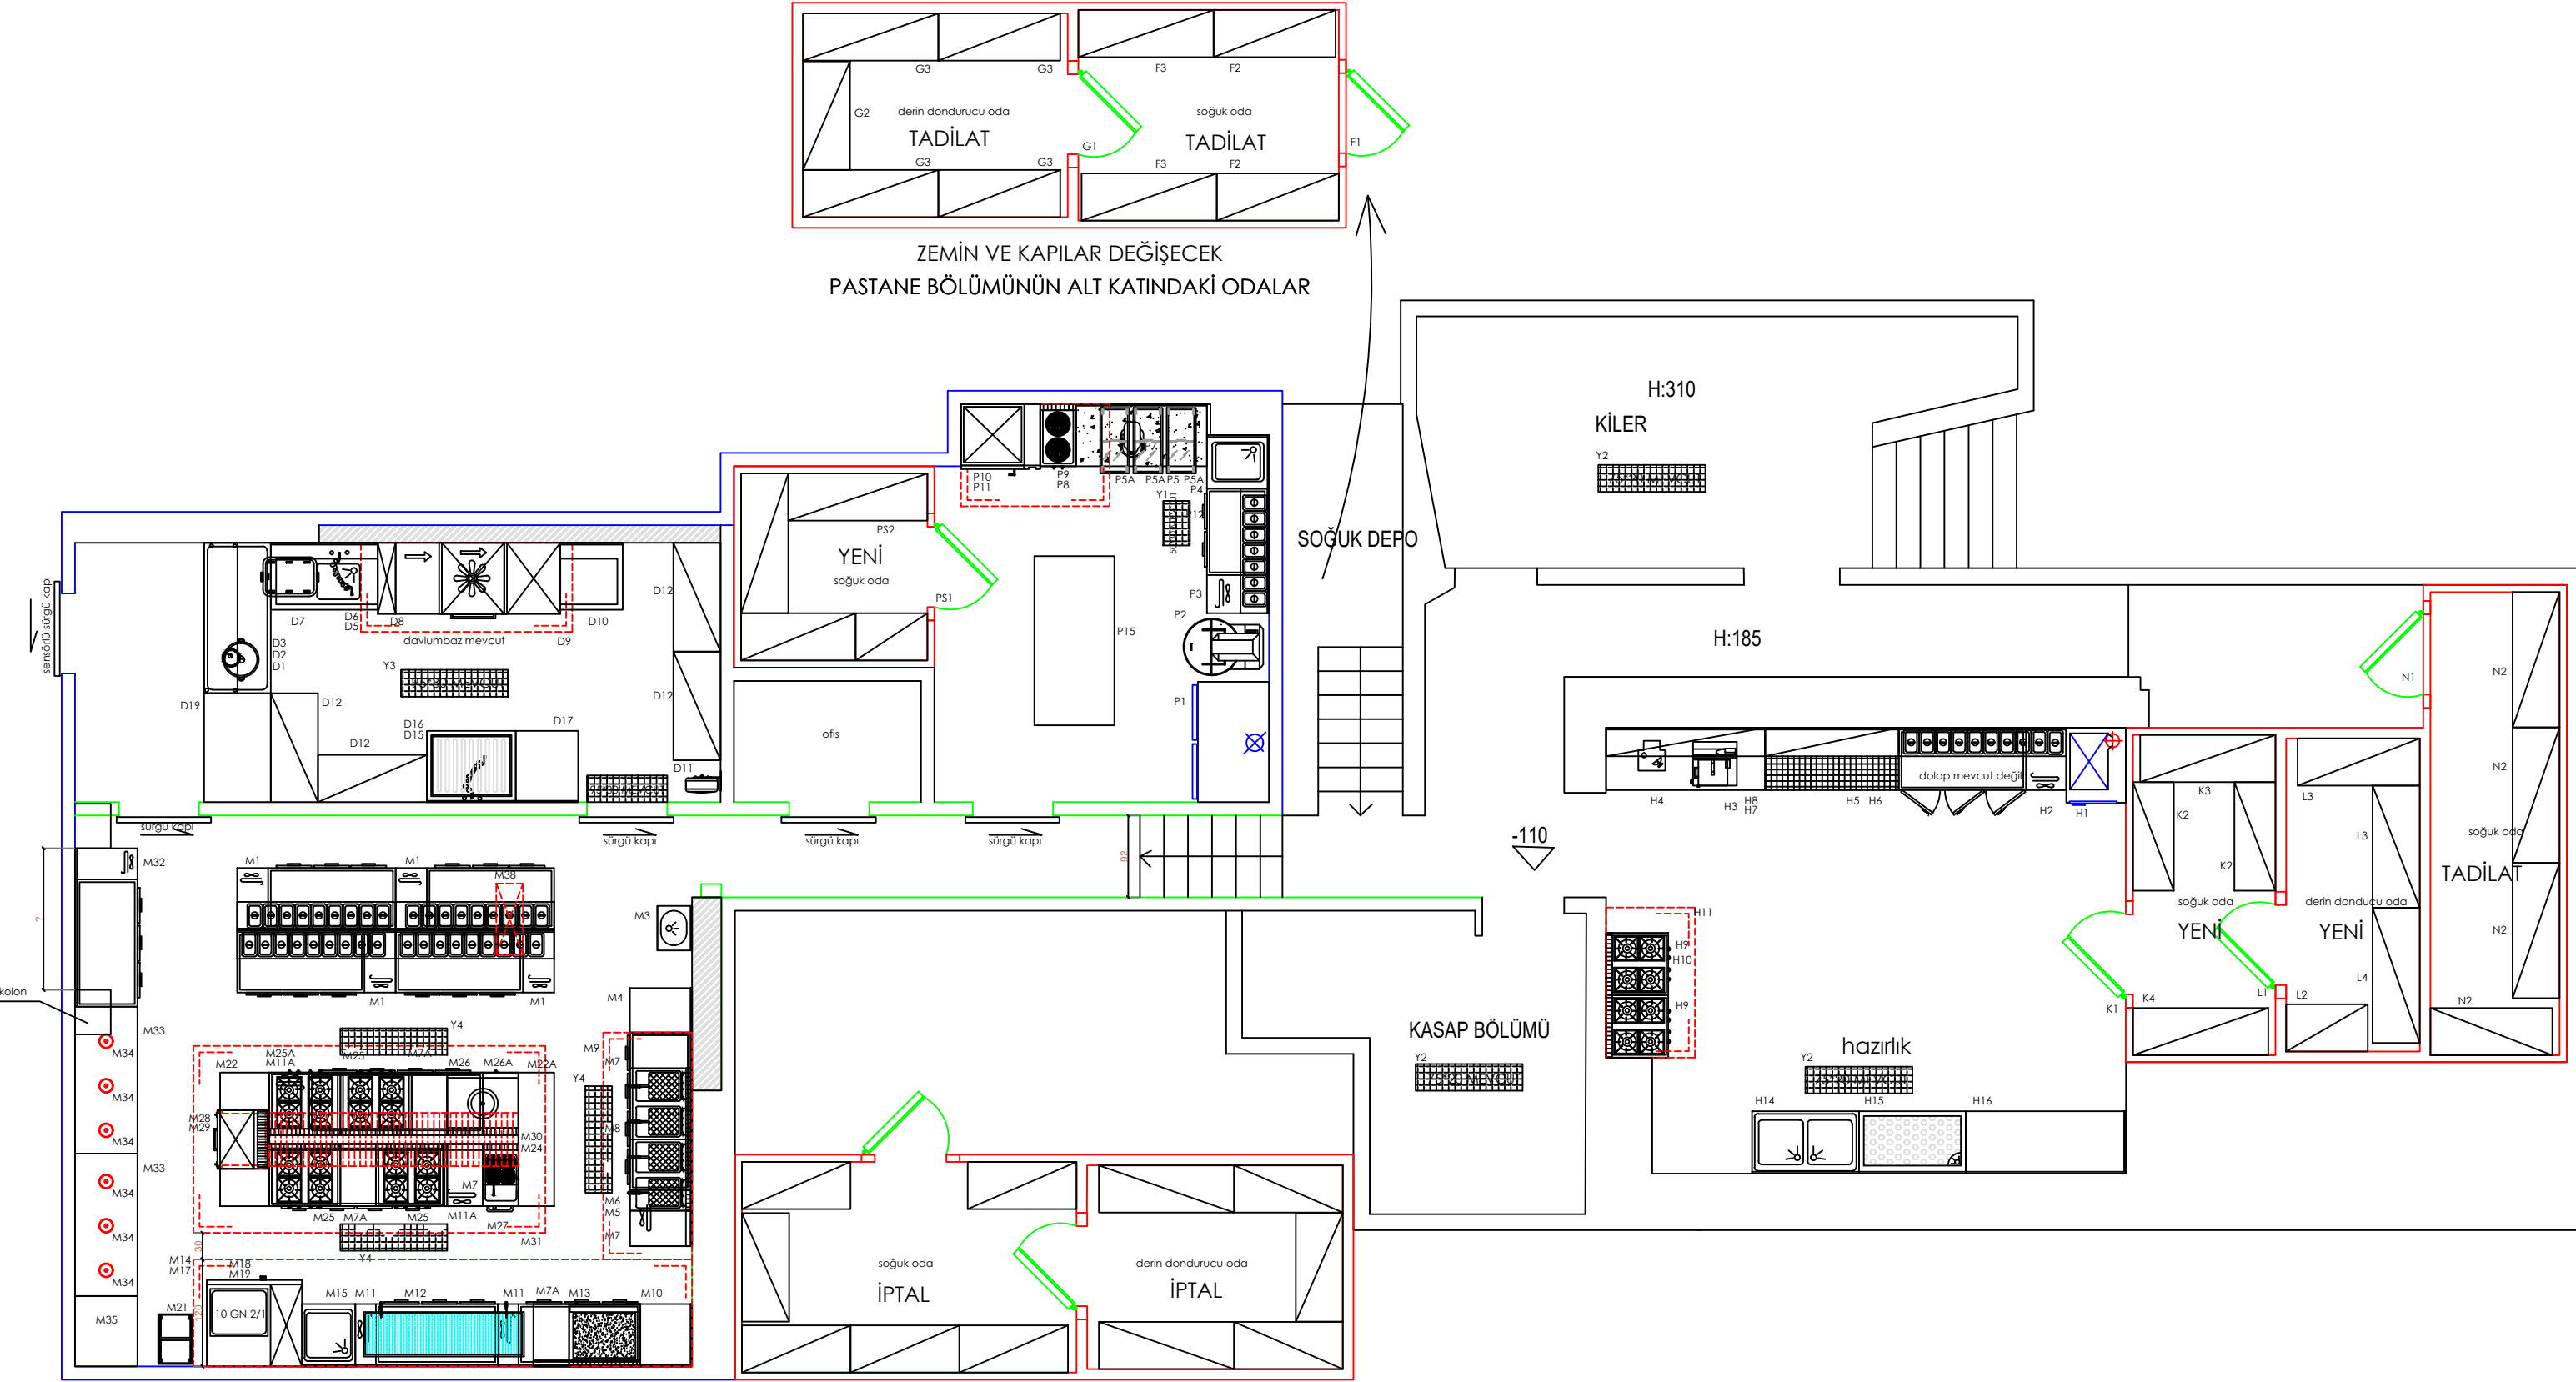

röleveden sonraki giriş kat komple revizyon

P.NO	ÜRÜN ADI	ÖLÇÜ	AD.
M- MUTFAK			
M1	MAKE-UP BUZDOLABI - MEVCUT	178*70*85/135	4
M3	TEK EYVELİ ÇALIŞMA TEZGAHI	60*70*85	1
M4	ÇALIŞMA TEZGAHI, TABAN VE ARA RAFLI	150*70*85	1
M5	CHAZALTI DERİN DONDURUCU, TEK SIRA ÇEKMECELİ	240*70*60	1
M6	FRİTÖZ, ÇİFT HAZNELİ, ELK., SETÜSTÜ - MEVCUT	80*73*25	1
M7	NÖTR ARA TEZGAH, SETÜSTÜ	40*73*25	3
M7A	NÖTR ARA TEZGAH, ÇEKMECELİ, SETÜSTÜ	40*73*25	3
M8	FRİTÖZ, ÇİFT HAZNELİ, ELK., SETÜSTÜ - MEVCUT ÖZTİ	80*73*25	1
M9	DAVLUMBAZ, DUVAR TIPI, FİLTRELİ - MEVCUT	310*100*50	1
M10	ÇALIŞMA TEZGAHI, TABAN RAFLI	115*70*85	1
M11	CHAZALTI BUZDOLABI, ÇİFT SIRA ÇEKMECELİ - MEVCUT	160*70*60	2
M11A	CHAZALTI BUZDOLABI, ÇİFT SIRA ÇEKMECELİ	240*70*60	2
M12	POWER GRILL, GAZLI, SETÜSTÜ	80*73*25	2
M13	PLATE IZGARA, GAZLI, SETÜSTÜ	80*73*25	1
M14	DUVAR KAPLAMA SACI	850 cm	1
M15	TEK EYVELİ ÇALIŞMA TEZGAHI	60*70*85	1
M17	DAVLUMBAZ, DUVAR TIPI, FİLTRELİ	376*100*50	1
M18	FİRİN TEZGAHI, TEPŞİ İSTİFLİ, TABAN RAFLI	90*75*70	1
M19	YEMEK FİRİNİ, GAZLI	10 GN 1/1	1
M21	TEPŞİ TAŞIMA ARABASI, GN 1/1	15 KATLI	1
M22	ÇALIŞMA TEZGAHI, TABAN VE ARA RAFLI, DOLAPLI	150*55*85	1
M22A	ÇALIŞMA TEZGAHI, TABAN VE ARA RAFLI, ETİRAFI KAPALI	150*40*85	1
M23	CHAZALTI BUZDOLABI, ÇİFT SIRA ÇEKMECELİ	120*70*60	3
M24	PASLANMAZ GÖVDELİ TESİSAT DUARI	280 cm	1
M25	DÖRT AÇIK ALEVİLİ OCAK, GAZLI, SETÜSTÜ - MEVCUT	80*70*30	3
M25A	DÖRT AÇIK ALEVİLİ OCAK, GAZLI, SETÜSTÜ	80*73*25	1
M26	KAPALI OCAK, GAZLI, SETÜSTÜ - MEVCUT	80*73*25	1
M26A	CHAZALTI NÖTR DOLAP	40*70*60	1
M27	MAKARNA PİSİRCİ, ELK., SETÜSTÜ - MEVCUT	40*73*25	1
M28	SALAMANDER, ASANSÖRLÜ, ELK.	60*60*60	1
M29	SALAMANDER RAFI	60*60*4	1
M30	TAVA RAFI	280*40*40	1
M31	DAVLUMBAZ, ADA TİPİ, FİLTRELİ - MEVCUT	400*210*50	1
M32	TEZGAH TIPI BUZDOLABI, 3 SIRA ÇEK. - PBIANCO - MEVCUT	178*70*85/135	1
M33	SICAK TABAK DOLABI - MEVCUT	160*70*85	2
M34	SARKIT INFRARED LAMBA	-	6
M35	ÇALIŞMA TEZGAHI, TABAN VE ARA RAFLI	80*70*85	1
M38	SİNEK ÖLDÜRÜCÜ - MEVCUT	-	1
D- BULAŞIK YIKAMA			
D1	BULAŞIK SIYIRMA TEZGAHI - MEVCUT	190*70*85	1
D2	BASKET RAFI - MEVCUT	190*40*60	1
D3	ÇÖP ARABASI - MEVCUT	40*50	1
D5	TEK EYVELİ BYM GİRİŞ TEZGAHI	135*75*85	1
D6	ÖN YIKAMA DUŞU, ARA MUSLUKLU, DUVARA MONTE	110*50	1
D7	YAĞ TUTUCU - MEVCUT	110*50	1
D8	BULAŞIK YIKAMA MAKİNASI, KONVEYÖRLÜ - MEVCUT	2000 d/s	1
D9	DAVLUMBAZ, DUVAR TIPI, FİLTRESİZ - MEVCUT	240*100*50	1
D10	BYM ÇIKIŞ TEZGAHI, TABAN RAFLI	70*75*85	1
D11	YER YIKAMA HORTUMU - MEVCUT	10 mtl	1
D12	İSTİF RAFI, 4 KATLI, DEMONTE - MEVCUT	122*53*160	4
D15	KAZAN YIKAMA EYYESİ - MEVCUT	120*80*57/91	1
D16	ÖN YIKAMA DUŞU, DUVAR MONTE	-	1
D17	ÇALIŞMA TEZGAHI, TABAN RAFLI	100*80*57/91	1
P- PASTANE			
P1	DEPO TIPI BUZDOLABI, TEK KAPILI - MEVCUT	70*85*205	1
P2	SİRALI HAMUR YOĞURMA MAKİNASI - MEVCUT	-	1
P3	MAKE-UP DOLABI, 3 SIRA ÇEKMECELİ	140*70*85/142	1
P4	TEK EYVELİ ÇALIŞMA TEZGAHI	60*70*85	1
P5	MERMER TABLALI ÇALIŞMA TEZGAHI	130*70*85	1
P5A	ÜN-ŞEKER ARABASI - MEVCUT	103 lt	3
P7	KITCHEN AID MİKSER - MEVCUT	6,9 lt	1
P8	CHAZALTI ÇALIŞMA TEZGAHI, TABAN RAFLI - MEVCUT ?	40*70*60	1
P9	İKİ GÖZLÜ OCAK, ELK., SETÜSTÜ	40*70*30	1
P10	FİRİN TEZGAHI - MEVCUT	105*95*70	1
P11	PATİSERİE FİRİNİ	10 GN 2/1	1
P12	DAVLUMBAZ, DUVAR TIPI, FİLTRELİ	160*115*50	1
P13	ÇALIŞMA TEZGAHI, TABAN VE ARA RAFLI	120*40*80	1
P14	TEZGAH TIPI BUZDOLABI, 3 SIRA ÇEKMECELİ	120*70*85	1
P15	ÇALIŞMA TEZGAHI - MEVCUT	190*90*85	1
PS- PASTANE SOĞUK ODA			
PS1	PANEL TİP SOĞUK ODA, ZEMİNLİ, SÜRGÜ KAPILI	290*225*240	1
PS2	İSTİF RAFI, DEMONTE, 4 KATLI - MEVCUT	-	4
F- PASTANE ALTI SOĞUK ODA			
F1	PANEL TİP SOĞUK ODA, ZEMİNLİ, TADİLAT	250*320*240	1
F2	İSTİF RAFI, 4 KATLI, DEMONTE - MEVUT	137*53*160	2
F3	İSTİF RAFI, 4 KATLI, DEMONTE - MEVUT	152*53*160	2
G- PASTANE ALTI DERİN DONDURUCU ODA			
G1	PANEL TİP DERİN DONDURUCU ODA, ZEMİN+KAPLI, TADİLAT	250*320*240	1
G2	İSTİF RAFI, 4 KATLI, DEMONTE - MEVUT	122*53*160	1
G3	İSTİF RAFI, 4 KATLI, DEMONTE - MEVUT	137*53*160	4
H- HAZIRLIK			
H1	DEPO TIPI BUZDOLABI, TEK KAPILI - MEVCUT	70*85*205	1
H2	MAKE-UP BUZDOLABI VEYA TEZGAH - MEVCUT	178*70*85/135	1
H3	GIDA DİLİMLEME MAKİNASI - MEVCUT	-	1
H4	SEBZE DOĞRAMA MAKİNASI - MEVCUT	-	1
H5	POLİETİLEN TABLALI ÇAL. TEZ., TABAN RAFLI, ÇEKMECELİ	150*70*85	1
H6	DUVAR RAFI	150*30*4	1
H7	ÇALIŞMA TEZGAHI, TABAN RAFLI	180*70*85	1
H8	DUVAR RAFI	180*30*4	1
H9	4 AÇIK ALEVİLİ OCAK, GAZLI, SETÜSTÜ - MEVCUT	80*70*30	2
H10	CHAZALTI ÇALIŞMA TEZGAHI - MEVCUT	160*70*60	1
H11	DAVLUMBAZ, DUVAR TIPI, MEVCUT	170*100*50	1
H14	ÇİFT EYVELİ ÇALIŞMA TEZGAHI - MEVCUT	120*70*85	1
H15	SEBZE BASMA EYYESİ	120*70*85	1
H16	ÇALIŞMA TEZGAHI, TABAN RAFLI - MEVCUT	180*70*85	1
K- HAZIRLIK SOĞUK ODA			
K1	PANEL TİP SOĞUK ODA, ZEMİNLİ	180*375*240	1
K2	İSTİF RAFI, 4 KATLI, DEMONTE - MEVCUT	122*46*160	2
K3	İSTİF RAFI, 4 KATLI, DEMONTE - MEVCUT	152*46*160	1
K4	İSTİF RAFI, 4 KATLI, DEMONTE - MEVCUT	152*53*160	1
L- HAZIRLIK DERİN DONDURUCU ODA			
L1	PANEL TİP SOĞUK ODA, ZEMİNLİ	170*375*240	1
L2	İSTİF RAFI, 4 KATLI, DEMONTE - MEVCUT	91*53*160	1
L3	İSTİF RAFI, 4 KATLI, DEMONTE - MEVCUT	137*53*160	2
L4	İSTİF RAFI, 4 KATLI, DEMONTE - MEVCUT	152*53*160	1
N- SOĞUK ODA			
N1	PANEL TİP SOĞUK ODA, ZEMİNLİ - TADİLAT	170*535*240	1
N2	İSTİF RAFI, 4 KATLI, DEMONTE - MEVCUT	137*53*160	4
YER IZGARASI			
Y1	YER IZGARASI - MEVCUT	50*30*14	1
Y2	YER IZGARASI - MEVCUT	75*20*14	3
Y3	YER IZGARASI - MEVCUT	95*30*14	2
Y4	YER IZGARASI	120*30*14	3