


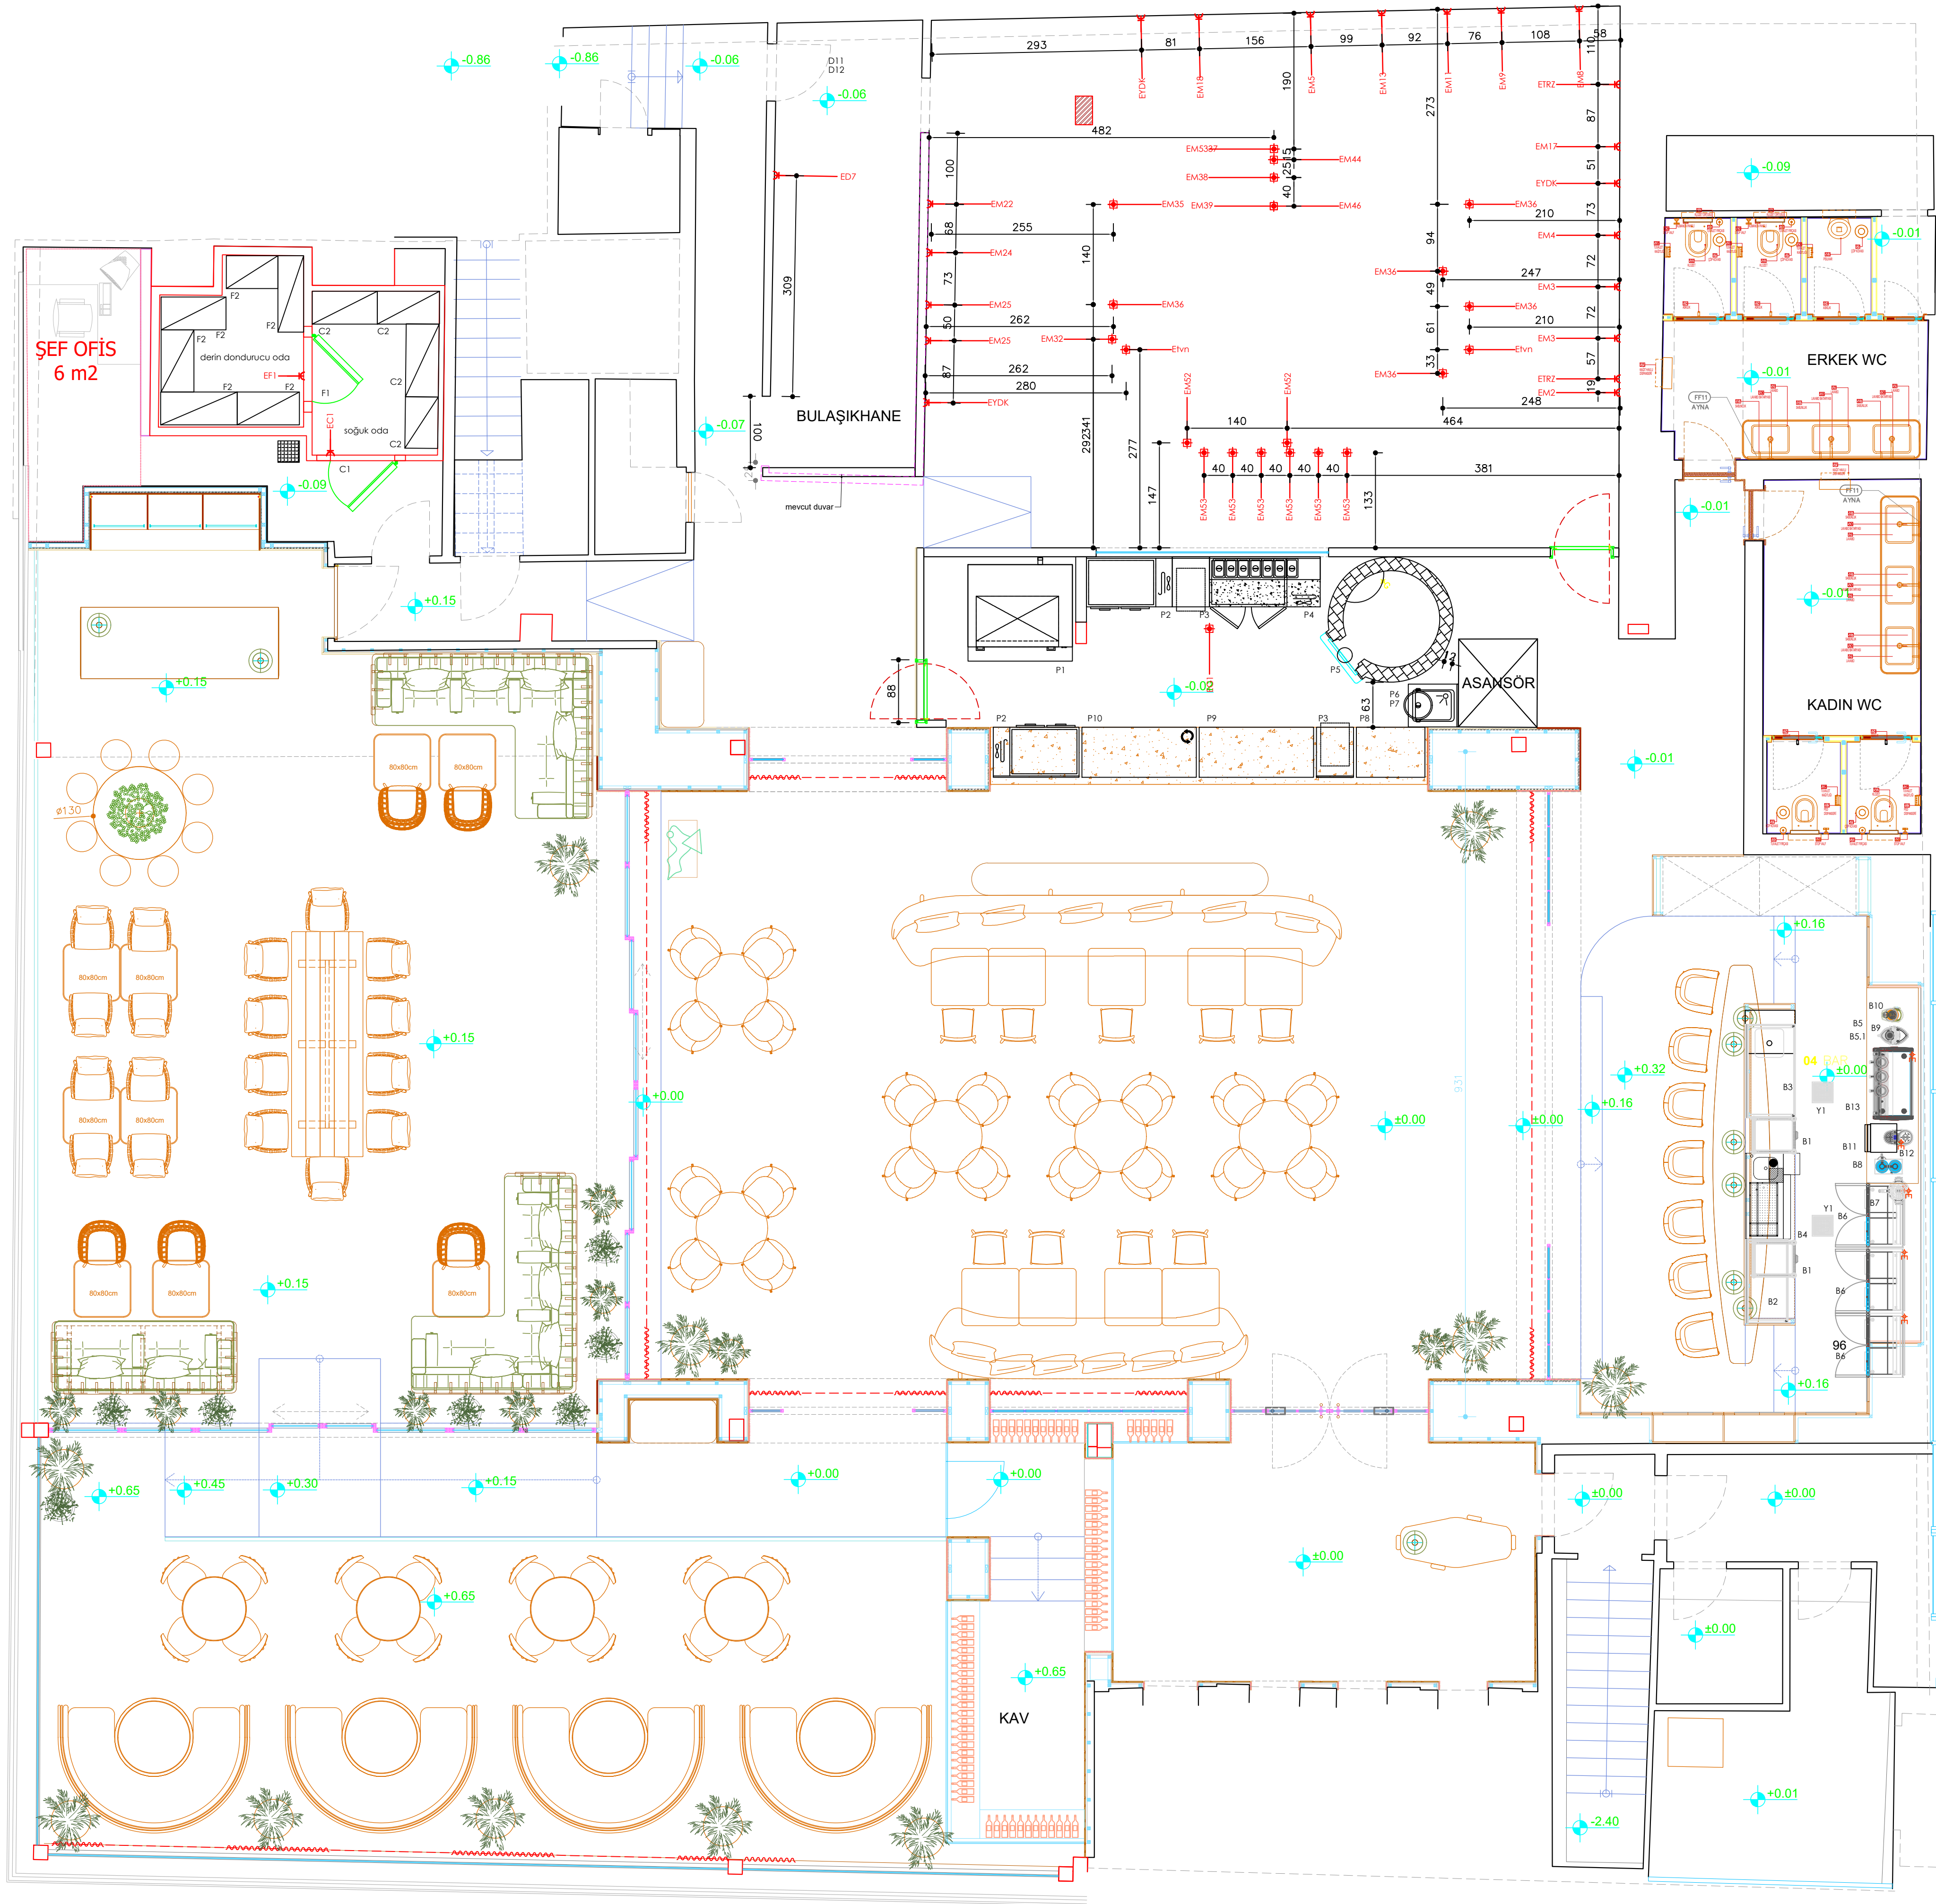

S.NO	ÜRÜN	220/380 V	KW.	AÇIKLAMA	AD.	TOPLAM KW.
PİDE-PIZZA HAZIRLIK						
EM2	BUZ MAKİNASI	220 V, 1.0	KW	H. 45 CM TOPRAKLI PRİZ BIRAKINIZ.	1	1
EM3	DEPO TİPİ BUZDOLABI	220 V, 1.0	KW	H. 190 CM TOPRAKLI PRİZ BIRAKINIZ.	2	2
EM4	DEPO TİPİ BUZDOLABI	220 V, 1.0	KW	H. 190 CM TOPRAKLI PRİZ BIRAKINIZ.	1	1
EM7	GDA DİLİMLEME MAKİNASI	220 V, 1.0	KW	H. 100 CM TOPRAKLI PRİZ BIRAKINIZ.	1	1
EM8	BLOK KAPAKLI DERİN DONDURUCU	220 V, 1.0	KW	H. 45 CM TOPRAKLI PRİZ BIRAKINIZ.	1	1
EM9	BLAST CHILLER	220 V, 1.0	KW	H. 45 CM TOPRAKLI PRİZ BIRAKINIZ.	1	1
EM11	ELECTROLUX MULTISİLM FIRIN	380 V, 6.9	KW	H. 45 CM 2 MT. KABLO UCU BIRAKINIZ.	1	6.9
EM13	ZANUSSI FIRIN	220 V, 1.0	KW	H. 45 CM TOPRAKLI PRİZ BIRAKINIZ.	1	1
EM15	ELECTROLUX FIRIN	220 V, 1.0	KW	H. 45 CM TOPRAKLI PRİZ BIRAKINIZ.	1	1
EM16	FAGOR BUZDOLABI	220 V, 1.0	KW	H. 45 CM TOPRAKLI PRİZ BIRAKINIZ.	1	1
EM22	DEPO TİPİ BUZDOLABI	220 V, 1.0	KW	H. 190 CM TOPRAKLI PRİZ BIRAKINIZ.	1	1
EM24	ESMACH MİKSER	380 V, 2.2	KW	H. 45 CM 2 MT. KABLO UCU BIRAKINIZ.	1	2.2
EM25	MAKARNA MAKİNASI	380 V, 1.1	KW	H. 45 CM 2 MT. KABLO UCU BIRAKINIZ.	2	2.2
EM32	MAKE-UP ÜNİTESİ	220 V, 1.0	KW	H. 10 CM 2 MT. KABLO UCU TOPRAKLI PRİZ BIRAKINIZ.	1	1
EM35	MAKE-UP ÜNİTESİ	220 V, 1.0	KW	H. 10 CM 2 MT. KABLO UCU TOPRAKLI PRİZ BIRAKINIZ.	1	1
EM36	TEZGAH TİPİ BUZDOLABI	220 V, 1.0	KW	H. 10 CM 2 MT. KABLO UCU TOPRAKLI PRİZ BIRAKINIZ.	5	5
EM37	MAKARNA FİŞİRCİ (371099)	380 V, 6.0	KW	H. 45 CM 2 MT. KABLO UCU BIRAKINIZ.	1	6
EM38	MAKARNA FİŞİRCİ (371099)	380 V, 6.0	KW	H. 45 CM 2 MT. KABLO UCU BIRAKINIZ.	1	6
EM39	ÇİHAZALI BUZDOLABI	220 V, 1.0	KW	H. 10 CM 2 MT. KABLO UCU TOPRAKLI PRİZ BIRAKINIZ.	1	1
EM44	FRIÖZ	380 V, 17.4	KW	H. 45 CM 2 MT. KABLO UCU BIRAKINIZ.	1	17.4
EM46	ÇİHAZALI BUZDOLABI	220 V, 1.0	KW	H. 10 CM 2 MT. KABLO UCU TOPRAKLI PRİZ BIRAKINIZ.	1	1
EM52	SICAKLIK DOLABI	220 V, 3.0	KW	H. 10 CM 2 MT. KABLO UCU TOPRAKLI PRİZ BIRAKINIZ.	1	3
EM53	İSİTİCİ LAMBA	220 V, 3.0	KW	TAVANDAN 2 MT. KABLO UCU BIRAKINIZ.	1	3
BULAŞIKHANE						
ED6	BULAŞIK YIKAMA MAKİNASI	380 V, 10.5	KW	H. 45 CM 2 MT. KABLO UCU BIRAKINIZ.	1	10.5
EYDK	YEDEK (3 NOKTAYA 3LU PRİZ)	220 V, 1.0	KW	H. 100 CM TOPRAKLI PRİZ BIRAKINIZ.	3	3
Em	TAVANDAN YEDEK UÇLU PRİZ	220 V, 1.0	KW	H. 100 CM TOPRAKLI PRİZ BIRAKINIZ.	2	2
ETRZ	TRİFAZE YEDEK HAY	380 V, 3.0	KW	H. 100 CM TOPRAKLI PRİZ BIRAKINIZ.	2	6
SOĞUK ODA DEPOLARI						
EC1	SOĞUK ODA	380 V, 4.0	KW	MOTORLUN YERLEŞTİRİLECEĞİ YERE 3 MT KABLO UCU BIRAKINIZ.	1	4
EF1	DERİN DONDURUCU ODA	380 V, 4.0	KW	MOTORLUN YERLEŞTİRİLECEĞİ YERE 3 MT KABLO UCU BIRAKINIZ.	1	4
MÜŞTERİ TEMİNİ ÜRÜNLERİN KATALOG DEĞERLERİNİ KONTROL EDİNİZ						

ELEKTRİK

MARCELLO MATTEO RESTURANT
BAR VE MUTFAK PROJESİ

DESIGNED/TASARIM	ADDEM AKPINAR
DRAWN/ÇİZEN	ADDEM AKPINAR
CHECKED/KONTROL	ADDEM AKPINAR
DATE/TARİH	17.09.2022

Sktürk
ÇAĞLAYAN MAH. FEVZİ ÇAKMAK CAD. NO: 67/B
KAĞITHANE/İSTANBUL
p: 0212 909 4312
w: skturk.com.tr | e: info@skturk.com.tr

00.00.00000
1/50 (A1)

2022-102-3