


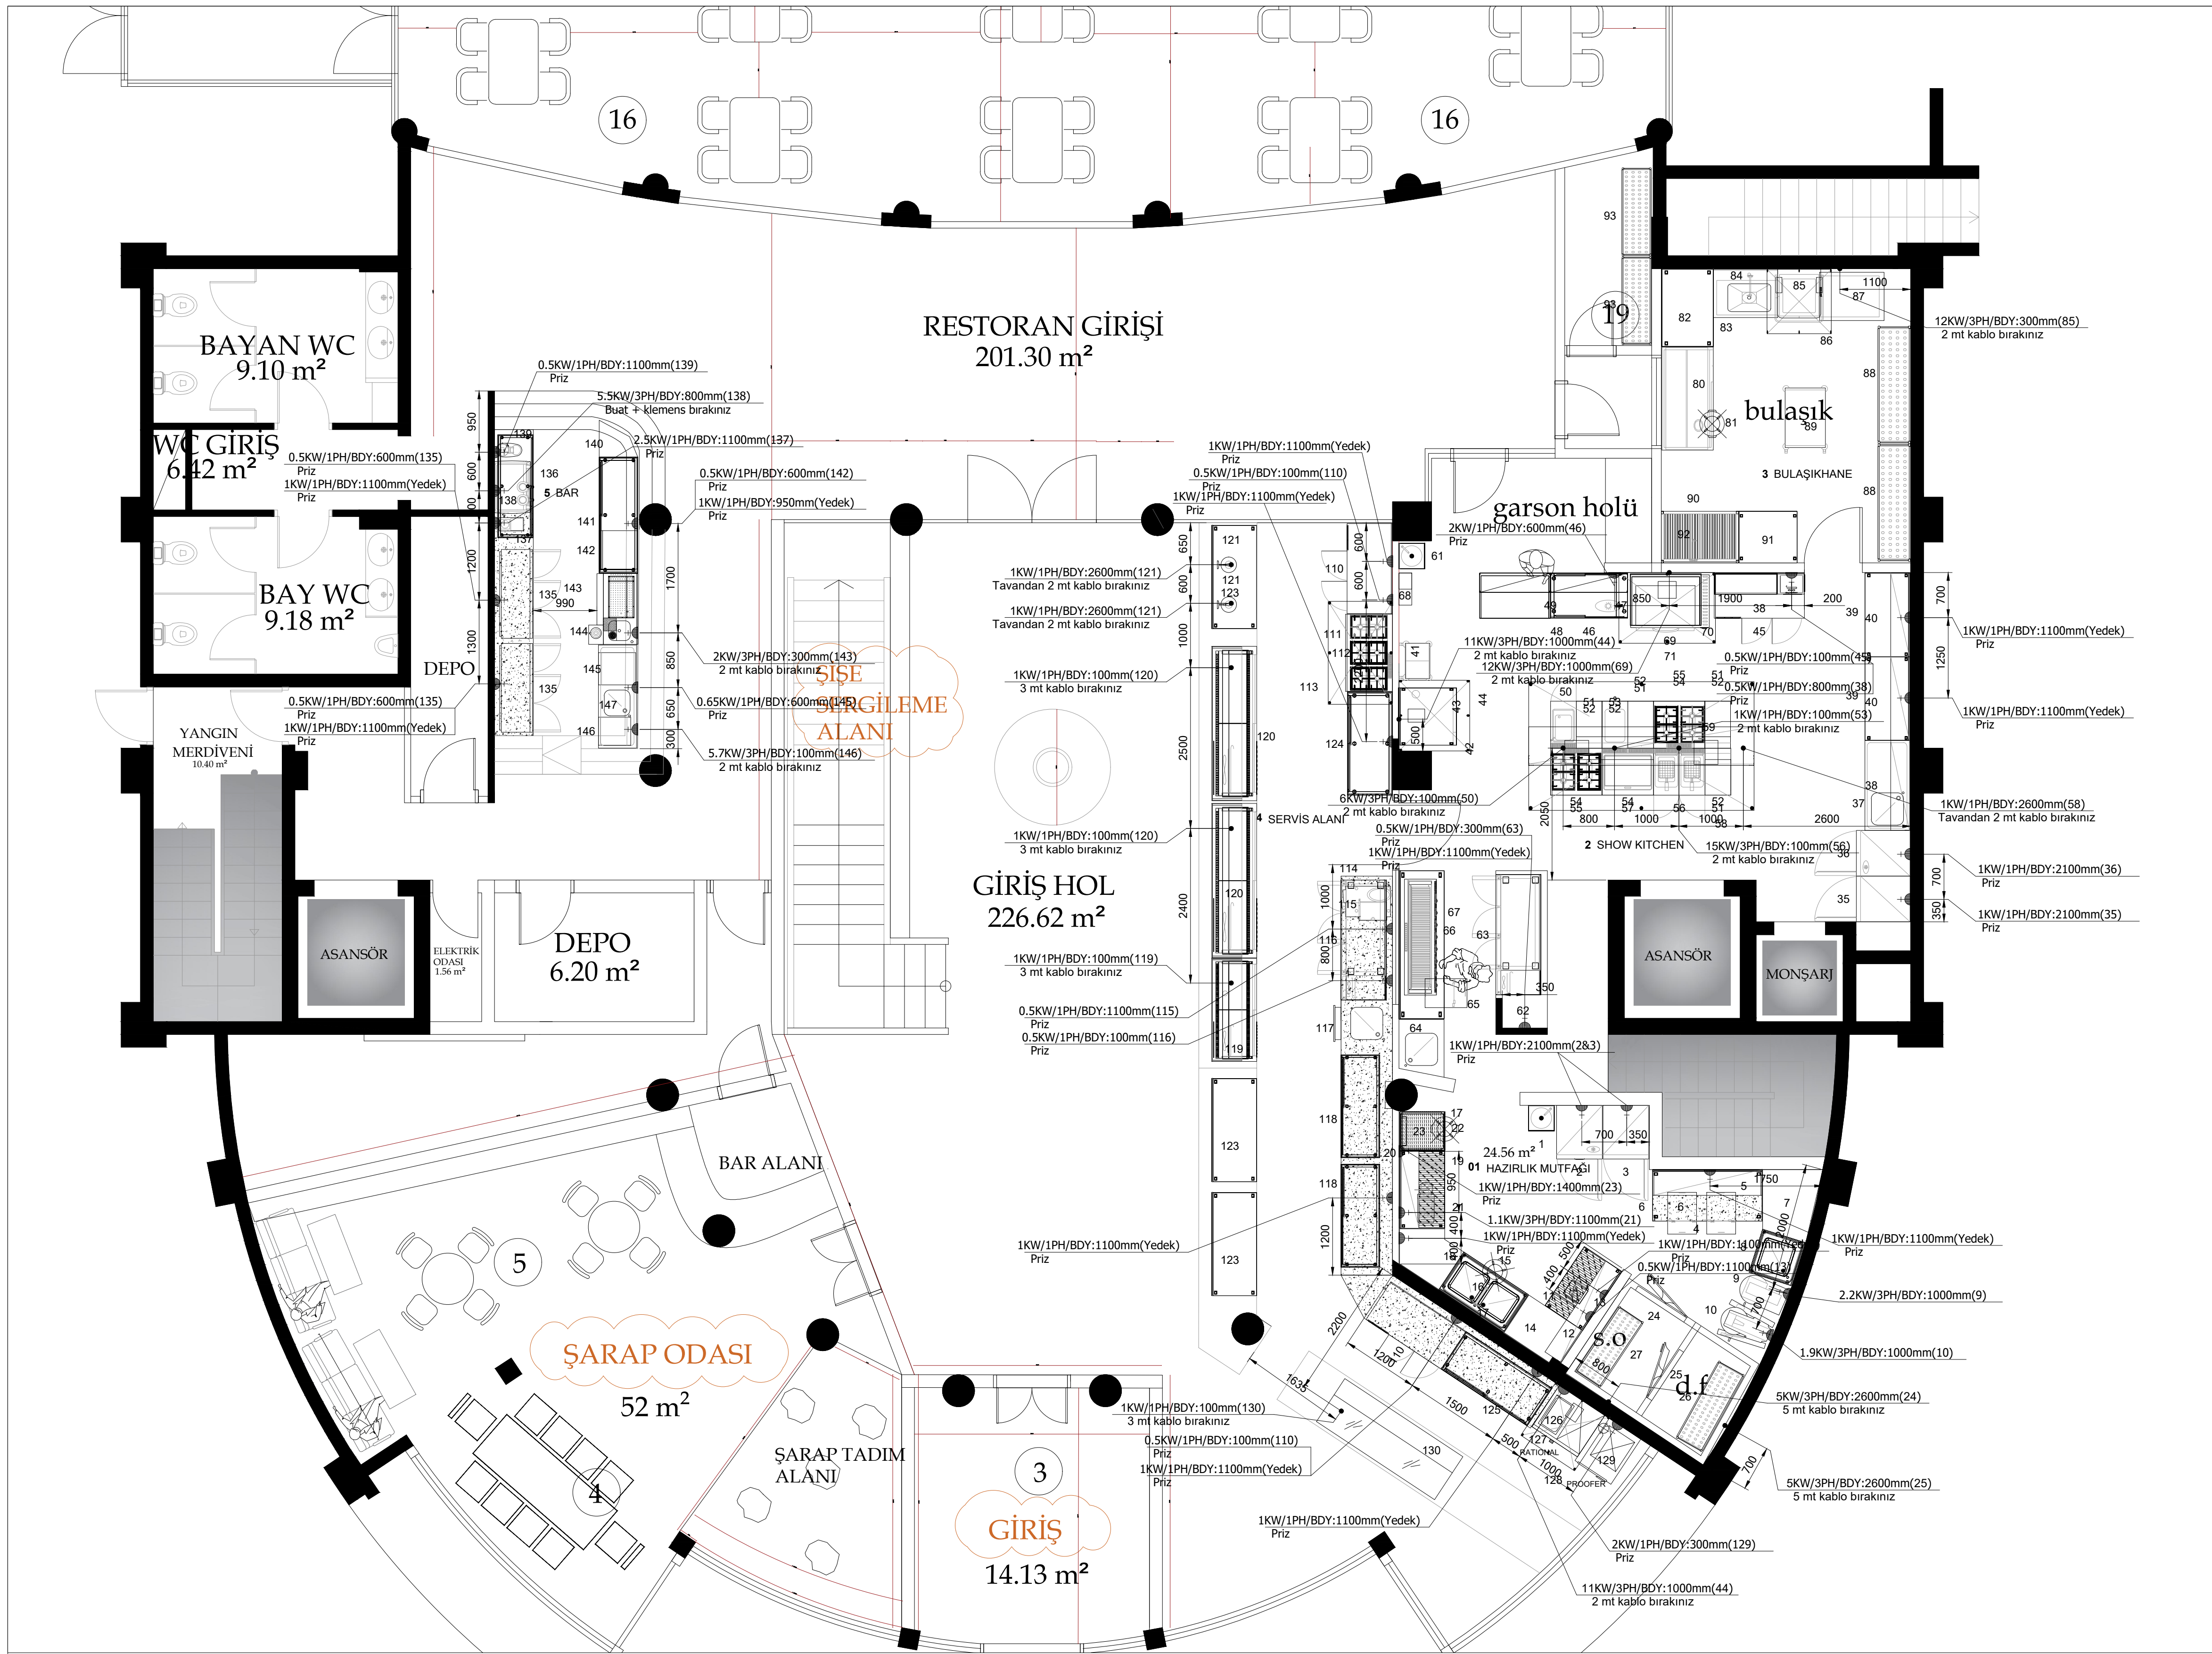

POS	Q.	A/E%KLAMA	BOYUTLAR	MİLLİMETERS
01-HAZIRLIK MUTFAĞI				
1	1	EL YIKAMA EYİYESİ DUVAR TİPİ DİZ KONTROLÜ	400x	400x 332
2	1	GN BUZDOLAP 304 1KAPLI 470L UZAK -2°C ECO	710x	835x 2050
3	1	GN DONDURUCU 1K 470L -22°C TOUCH R290	710x	835x 2050
4	1	MERMER TABLALI ÇALIŞMA TEZGAHI	1700x	850x 650
5	1	ÖNÜ AÇIK DUVAR DOLABI	1700x	400x 650
6	2	UN SEKER ARABASI	450x	650x 650
7	1	KÖSE TEZGAHI	900x	950x 850
8	1	1 EVYELİ TEZGAH 700 MM	700x	700x 1000
9	1	SPIRAL HAMUR YOGURMA MAK 1 HIZLI 32LT. 400/3	420x	720x 670
10	1	40 LT UNLU MAMUL MİKSERİ ELEKTRONİK 1PH	655x	850x 1370
11	1	POLİETİLEN TABLALI ÇALIŞMA TEZGAHI	1100x	700x 850
12	1	DUVAR RAFI	1700x	300x 30
13	1	VEGETABLE PREPARATION MACHINE 2,2L 3/75 RPM - 1 SPEED	390x	340x 610
14	1	ÇALIŞMA TEZGAHI	950x	700x 850
15	1	2 EVYELİ TEZGAH 1200 MM	1200x	700x 1000
16	1	SPREY DUSLU BATARYA 3/4 PREMIUM	800x	425x 1500
17	2	50 L SİS ÇÖP ARABASI KAPAKLI	380x	427x 605
18	1	KÖSE TEZGAHI	1240x	700x 850
19	1	POLİETİLEN TABLALI ÇALIŞMA TEZGAHI	1200x	700x 850
20	1	DUVAR RAFI	1200x	300x 30
21	1	ET KİYMARENDE ATASMAN-NO 22	280x	620x 430
22	1	ET KÜTÜĞÜ - POLİETİLEN TABLALI	600x	700x 850
23	1	BİÇAK STERİL DOLABI - 12 BİÇAK	450x	100x 650
24	1	SOGUK ODA	1240x	1785x 2400
25	1	DERİN DONDURUCU	1785x	1150x 2400
26	1	İSTİF RAFI	1370x	460x 1700
27	1	İSTİF RAFI	1220x	460x 1700
2-SHOW KITCHEN				
35	1	GN DONDURUCU 1K 470L -22°C TOUCH R290	710x	835x 2050
36	1	GN BUZDOLAP 304 1KAPLI 470L -2°C TOUCH R290	710x	835x 2050
37	1	TEK EVYELİ ÇALIŞMA TEZGAHI	1400x	700x 850
38	1	DUVAR RAFI 1400MM	1400x	300x 30
39	1	SALATA VE PIZZA SOĞUK HAZIRLIK ÜNİTESİ	1400x	340x 440
40	2	ÇALIŞMA TEZGAHI SİRTLİ 1200 MM	1300x	700x 1000
41	2	DUVAR RAFI	1300x	300x 30
42	1	GN KÜVET ARABASI 17XGN/1	452x	617x 1590
43	1	ELEK KONVEKSİYON FIRIN CROSSWISE 10X1/1	890x	900x 970
44	1	FIRIN ALT STANDI	890x	900x 600
45	1	DUVAR DAVLUMBAZI 304 1600X1100MM EXPORT	1100x	1100x 500
46	1	SOGUK TEZGAH 280LT 2 KAPILI SİRTLİ HD	1400x	700x 850
47	1	PASSTHROUGH SICAKLIK DOLABI 1200 MM	1200x	700x 900
48	1	ÇİFT SIRA SERVİS RAFI	1200x	300x 700
49	1	SERVİS TEZGAHI	1100x	700x 850
50	1	ÇİFT SIRA SERVİS RAFI	1100x	300x 700
51	1	ELEK MAKARNA PSİRCİ 1X24LT 800MM	400x	730x 850
52	5	SETUSTU ARA TEZGAH ÖNÜ KAPALI 400MM	400x	730x 250
53	1	ÖNÜ AÇIK ALT DOLAP 400MM	400x	550x 600
54	3	SETUSTU ELEKTRİK BAKAR MARİE 400MM	400x	730x 250
55	2	ÖNÜ AÇIK ALT DOLAP 800MM	800x	550x 600
56	1	4 AÇIK ATESLİ GAZLI OCAK 800MM	800x	730x 250
57	1	2X15LT ELEKTRİK FİRITZOZ DOLAPLI 800MM	800x	730x 850
58	1	SETUSTU GAZ IZGARADA DÜZ KROM PLEYT 800MM	800x	730x 250
59	1	ADA TİP DAVLUMBAZ 304 2800X1400MM EXPORT	2500x	2000x 500
60	1	TAVA RAFI	3500x	600x 30
61	1	EL YIKAMA EYİYESİ DUVAR TİPİ DİZ KONTROLÜ	400x	400x 332
62	1	ÇALIŞMA TEZGAHI	2445x	800x 900
63	1	GN 1/1 - TEZGAH TİP BUZDOLABI - INOX İÇ KAPILI	1855x	700x 850
64	1	TEK EVYELİ ÇALIŞMA TEZGAHI	900x	700x 850
65	1	KÖMÜR ARABASI	450x	650x 650
66	1	KENDİNDEN DAVLUMBAZLI KÖMÜRLÜ IZGARA	1800x	500x 1500
67	1	ÇALIŞMA TEZGAHI	2300x	700x 1000
68	1	BÖNCE GALOS DOLABI	400x	150x 300
69	1	PIZZA FIRINI - 6H	1220x	820x 720
70	1	FIRIN ALT STANDI	1100x	800x 850
71	1	DUVAR DAVLUMBAZI 304 1600X1100MM EXPORT	1500x	1100x 500
3-BULAŞIKHANE				
80	1	BULAŞIK KABUL TEZGAHI	1600x	800x 1551
81	1	50 L SİS ÇÖP ARABASI KAPAKLI	380x	427x 605
82	1	ÇALIŞMA TEZGAHI	1200x	800x 500
83	1	KAZAN YIK MAK GİRİŞ TEZGAHI SOL 900MM	1000x	750x 850
84	1	SPREY DUSLU BATARYA 3/4 PREMIUM	800x	425x 1500
85	1	GİYOTİN BULAŞIK MAKİNESİ 80 SEPİS	746x	755x 1549
86	1	DUVAR TİP FİLTRESİZ DAVLUMBAZ	1000x	1000x 500
87	1	BULAŞIK GİRİŞ-ÇIKIŞ TEZGAHI	1000x	750x 910
88	2	İSTİF RAFI	1830x	510x 1700
89	1	BULAŞIK TOPLAMA ARABASI	995x	695x 916
90	1	KAZAN YIKAMA EYİYESİ	1200x	800x 600
91	1	ÇALIŞMA TEZGAHI 900 MM	900x	800x 900
92	1	GN YIKAMA DUSU TEZGAH TİPİ SPREY ÜNİTESİ	300x	200x 1150
93	2	İSTİF RAFI	1370x	460x 1700
4-SERVİS ALANI				
110	2	SOGUK TEZGAH 280LT 2 KAPILI SİRTLİ HD	1400x	700x 850
111	1	6 AÇIK ATESLİ GAZLI OCAK 1200MM	1200x	730x 250
112	1	ÖNÜ AÇIK ALT DOLAP 1200MM	1200x	550x 600
113	1	DUVAR TİP FİLTRELİ DAVLUMBAZ	1600x	1000x 500
114	1	BY 12 DECORATIVE BANKO EVYELİ	5150x	800x 900
115	1	OTOMATİK DÖNMELEME MAKİNESİ 300 MM	760x	520x 590
116	1	GN 1/1 - TEZGAH TİP BUZDOLABI - INOX İÇ KAPILI	1855x	700x 850
117	1	ÇÖP ÜNİTESİ	600x	600x 850
118	2	DOLAPLI ARA RAFLI ÇALIŞMA TEZGAHI	1600x	600x 900
119	1	DÜZ CAMLI SOĞUK TESHİR DOLABI	1600x	700x 1350
120	2	DÜZ CAMLI SOĞUK TESHİR DOLABI	2400x	700x 1350
121	2	İSTİTÇİ LAMBA	240x	240x 216
122	3	TABAK TEZGAHI	1600x	700x 1000
124	1	DOLAPLI ARA RAFLI ÇALIŞMA TEZGAHI	1600x	700x 900
125	1	DOLAPLI ARA RAFLI ÇALIŞMA TEZGAHI	1600x	700x 900
126	1	RATIONAL FIRIN	0x	0x 0
127	1	FIRIN ALT STANDI	0x	0x 0
128	1	DUVAR TİP FİLTRESİZ DAVLUMBAZ	1000x	1000x 500
129	1	MAYALAMA ÜNİTESİ	0x	0x 0
130	1	DISPLAY ÜNİTESİ	2200x	800x 0
5-BAR				
135	2	İÇECEK BUZDOLABI 3 KAPILI	1380x	500x 910
136	1	KAHVE ÇEKMECELİ DOLAPLI ARA RAFLI ÇALIŞMA TEZGAHI	1600x	550x 900
137	1	FIL KAHVE MAK MANUEL İDAM 2PLEYT	205x	360x 430
138	1	2 GRUPLU ESPRESSO KAHVE MAKİNESİ	817x	559x 570
139	1	KAHVE DEĞİRMENİ	220x	400x 620
140	1	KÖSE TEZGAHI	550x	600x 850
141	1	KİSMİ DOLAPLI ARA RAFLI ÇALIŞMA TEZGAHI	1800x	600x 900
142	1	TEZGAH ALTI DONDURUCU 160LT	600x	600x 825
143	1	KORTİYL ÜNİTESİ BLENDER EYİVELİ SİREK RAFLI ALTI SOĞUK DOLAPLI	1200x	635x 850
144	1	BAR BLENDER	188x	410 170x
145	1	BUZ MAKİNESİ 42 KG/GÜN HAVA SOĞUTMALI	500x	580x 820
146	1	BAR YIK MAK [XS] DRENAJ P DET DİSP 30B/S	436x	495x 670
147	1	TEK EVYELİ ÇALIŞMA TEZGAHI	1600x	600x 850

AKKOZA

MUTFAK YERLEŞİM PLANI


DESİGN BY	MURAT ÖDÜL	DRAWING NO	DATE	SCALE
DRAWING BY	MURAT ÖDÜL	11072024	11/07/2024	1/50
CHECKED BY	MURAT ÖDÜL			

Merkez Mh. Günebakan Sk. No:24/B
Kâğıthane/İstanbul

\\..._Desktop\MURAT LOGO.jpg

ELEKTRİK TESİSAT DETAYI

ÖRNEK

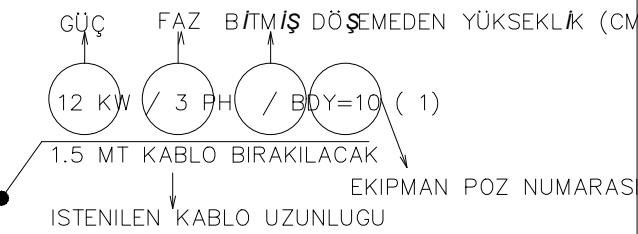

GÖSTERİM

ŞALTER

1 FAZLI PRİZ

3 FAZLI PRİZ

BAĞANTI NOKTASI

BDY BİTİMİS DÖŞEMEDEN YÜKSEKLİK

BÜTÜN ÖLÇÜLER CMM'DR

PRİZ DETAYI 1

TEZGAH TİPİ BUZDOLAPLARI İÇİN LÜTFEN PRİZ DETAYI 2 UYGULAYINIZ.

PRİZ DETAYI 2