


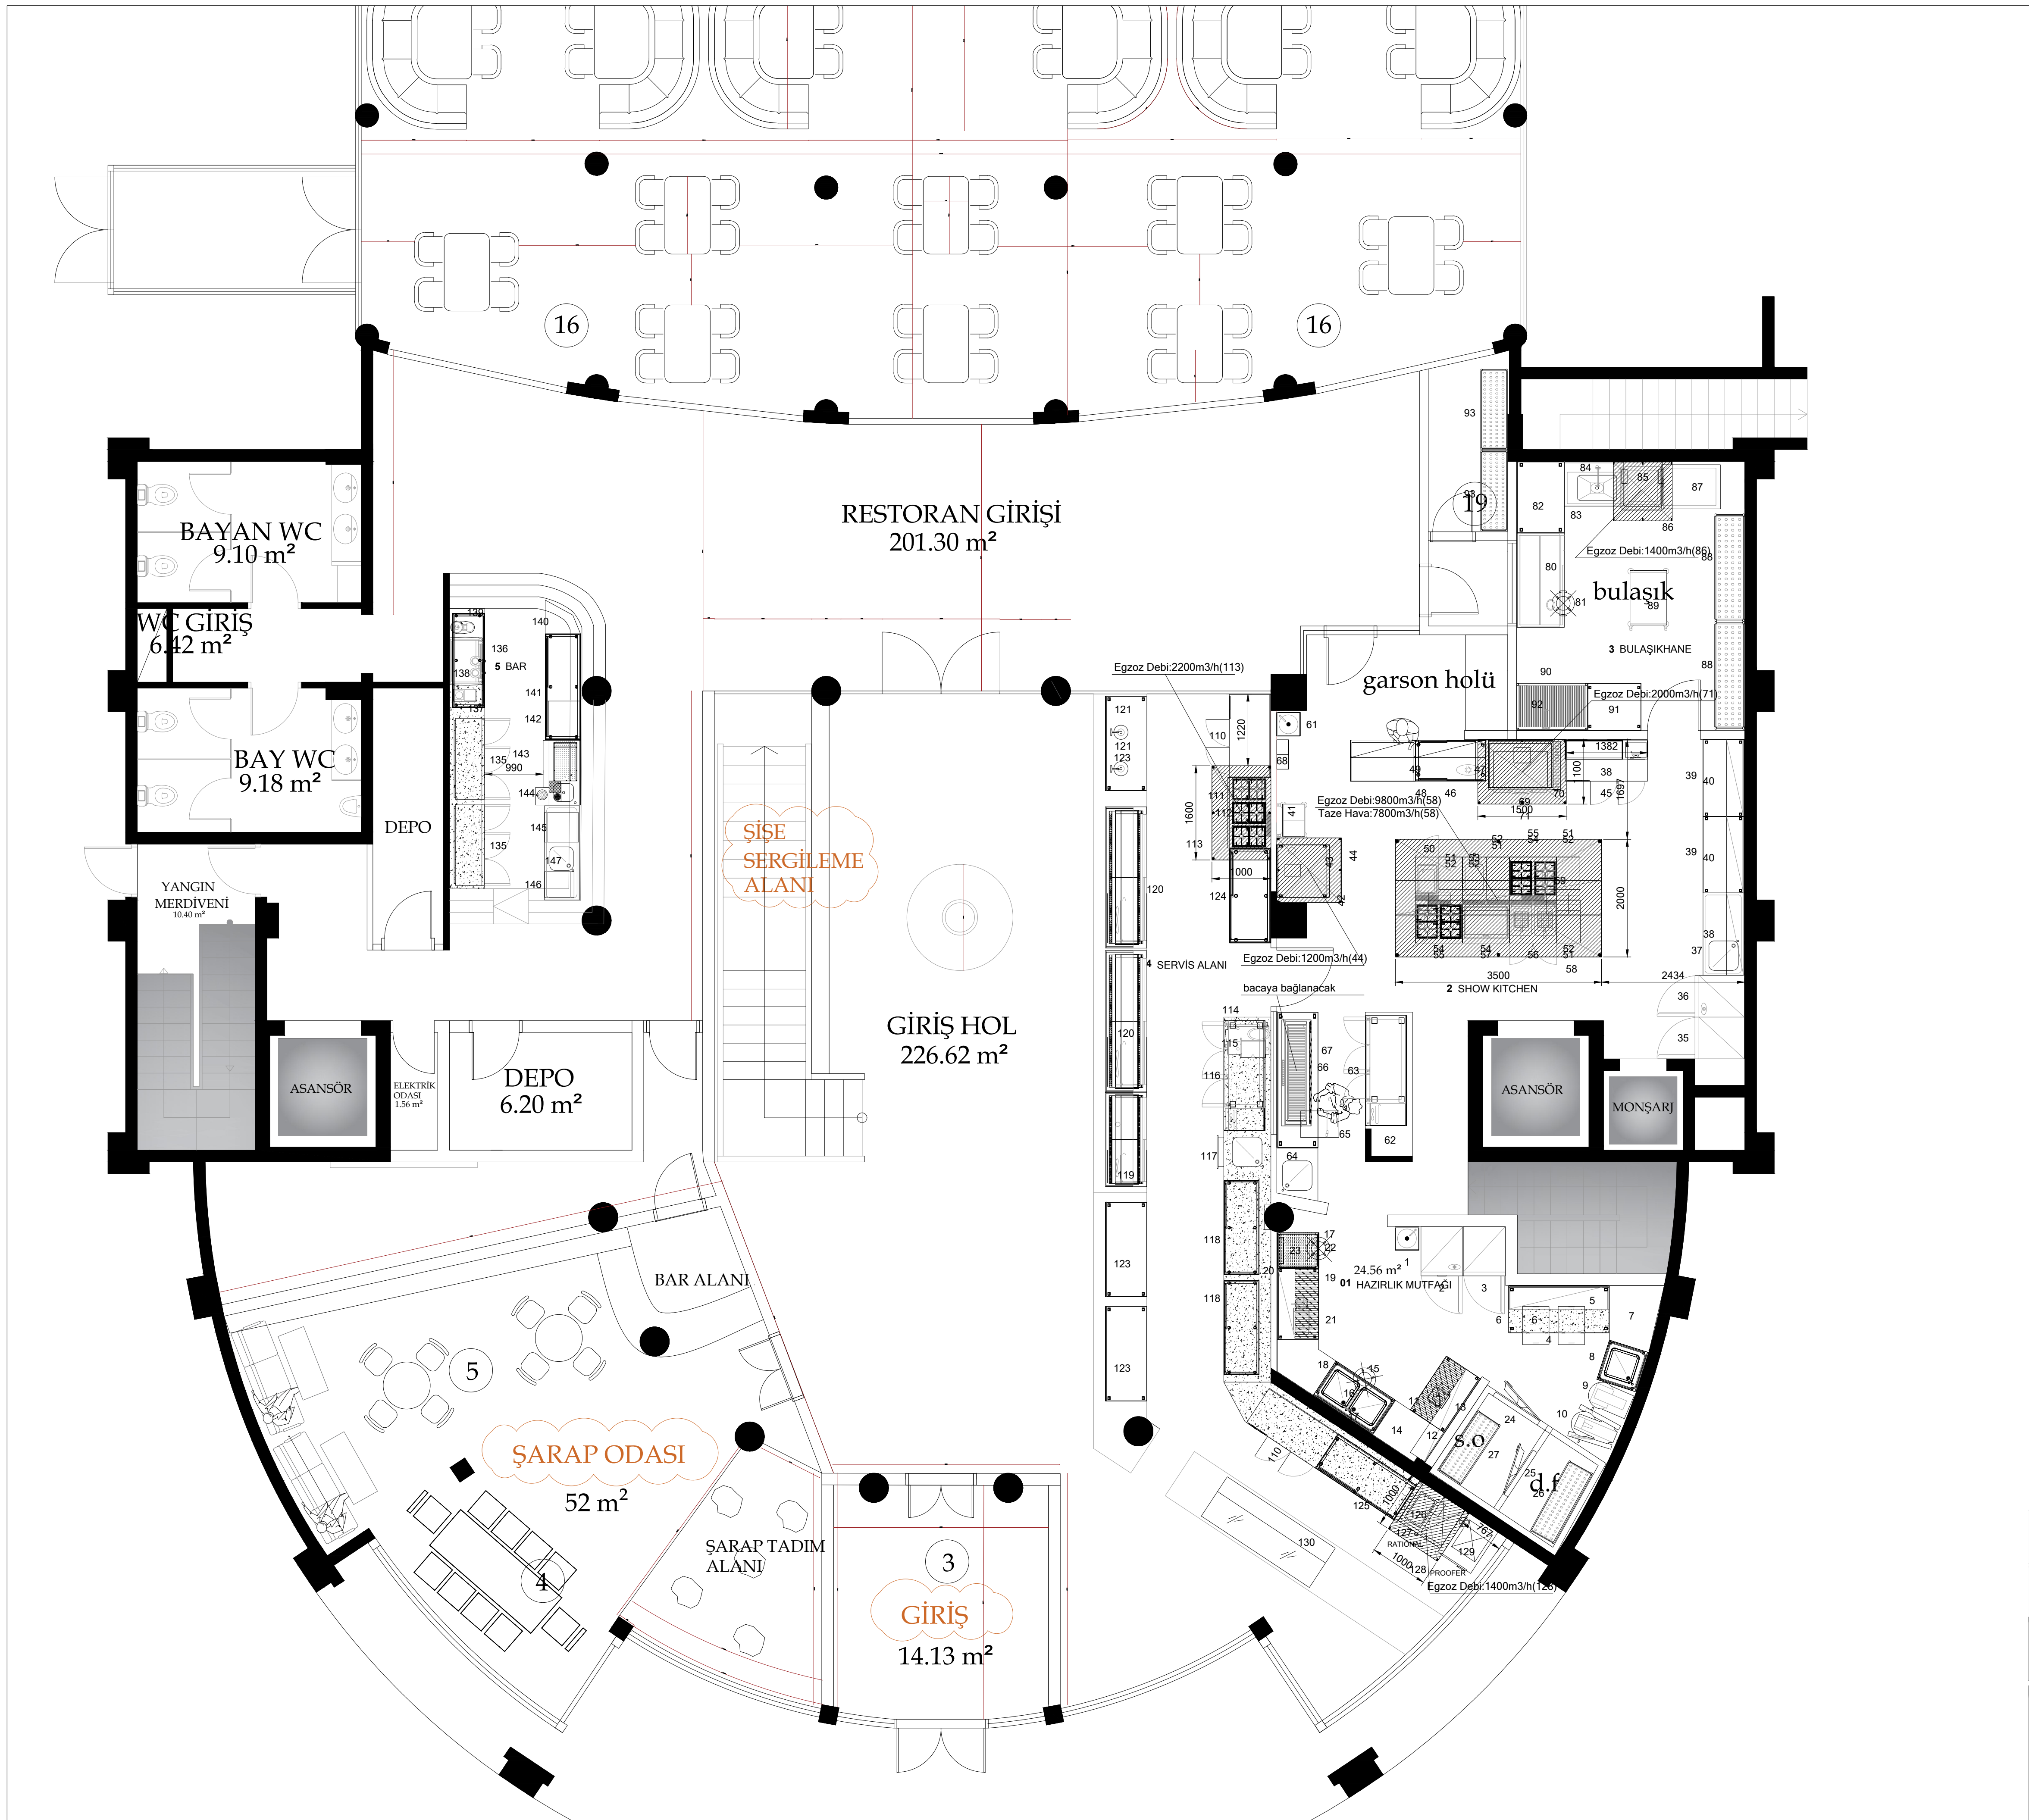

POS	Q.	A/E%KLAMA	BOYUTLAR MILLİMETERS		
01-HAZIRLIK MUTFAĞI					
1	1	EL YIKAMA EYİYESİ,DUVAR TIPI,DİZ KONTROLÜ	400x	400x	332
2	1	GN BUZDOLAP,304,1KAPİ-470L,UZAK-2°C-ECO	710x	835x	2050
3	1	GN D DONDURUCU,1K-470L,-22°C,TOUCH,R290	710x	835x	2050
4	1	MERMER TABLALI ÇALIŞMA TEZGAHI	1700x	850x	850
5	1	ONÜ AÇIK DUVAR DOLABI	1700x	400x	650
6	2	UN SEKER ARABASI	450x	650x	660
7	1	KÖSE TEZGAHI	900x	950x	850
8	1	1 EVVELİ TEZGAH 700 MM	700x	700x	1000
9	1	SPIRAL HAMUR YOGURTMA MAK.1 HIZLI-32LT. 400/3	420x	720x	670
10	1	40 LT UNLU MAMUL MİKSERİ,ELEKTRONİK-1PH	655x	850x	1370
11	1	POLİETİLEN TABLALI ÇALIŞMA TEZGAHI	1100x	700x	850
12	1	DUVAR RAFI	1700x	300x	30
13	1	VEGETABLE PREPARATION MACHINE 2,2L 3/5 RPM - 1 SPEED	390x	340x	610
14	1	ÇALIŞMA TEZGAHI	980x	700x	850
15	1	2 EVVELİ TEZGAH 1200 MM	1200x	700x	1000
16	1	SPREY DUSLU BATARYA 3/4 PREMIUM	800x	425x	1500
17	2	50 L SİS ÇÖP ARABASI-KAPAKLI	380x	427x	605
18	1	KÖSE TEZGAHI	1240x	700x	850
19	1	POLİETİLEN TABLALI ÇALIŞMA TEZGAHI	1200x	700x	850
20	1	DUVAR RAFI	1200x	300x	30
21	1	ET KIYMA/RENDE ATASMANI-NO.22	280x	620x	430
22	1	ET KÜTÜĞÜ - POLİETİLEN TABLALI	600x	700x	850
23	1	BİÇAK STERİL DOLABI - 12 BİÇAK	450x	150x	650
24	1	SOGUK ODA	1240x	1785x	2400
25	1	DERİN DONDURUCU	1785x	1150x	2400
26	1	İSTİF RAFI	1370x	460x	1700
27	1	İSTİF RAFI	1220x	460x	1700
2-SHOW KITCHEN					
35	1	GN D DONDURUCU,1K-470L,-22°C,TOUCH,R290	710x	835x	2050
36	1	GN BUZDOLAP,1 KAPİ-470L,-2°C,TOUCH,R290	710x	835x	2050
37	1	TEK EVVELİ ÇALIŞMA TEZGAHI	1400x	700x	850
38	1	DUVAR RAFI 1400MM	1400x	300x	30
38	1	SALATA VE PIZZA SOĞUK HAZIRLIK ÜNİTESİ	1400x	340x	440
39	2	ÇALIŞMA TEZGAHI, SIRTILI 1200 MM	1300x	700x	1000
40	2	DUVAR RAFI	1300x	300x	30
41	1	GN KÜVET ARABASI-17XGN/1	452x	617x	1590
42	1	ELEK KONVEKSİYON FIRIN CROSSWISE-10X1/1	890x	900x	970
43	1	FIRIN ALT STANDI	890x	900x	600
44	1	DUVAR DAVLUMBAZI,304-1600X1100MM EXPORT	1100x	1100x	500
45	1	SOGUK TEZGAH 280LT.2 KAPILI,SIRTILİHD	1400x	700x	850
46	1	PASSTHROUGH SICAKLIK DOLABI 1200 MM	1200x	700x	900
47	1	ÇİFT SIRA SERVİS RAFI	1200x	300x	700
48	1	SERVİS TEZGAHI	1100x	700x	850
49	1	ÇİFT SIRA SERVİS RAFI	1100x	300x	700
50	1	ELEK MAKARNA PSİRCİ,1X24LT,800MM	400x	730x	850
51	4	SETÜSTÜ ARA TEZGAH,ONÜ KAPALI-400MM	400x	730x	250
52	5	ONÜ AÇIK ALT DOLAP-400MM	400x	550x	600
53	1	SETÜSTÜ ELEKTRİK BİNA-MARİE-400MM	400x	730x	250
54	3	ONÜ AÇIK ALT DOLAP-800MM	800x	550x	600
55	2	4-AÇIK ATESLİ GAZLI OCAK-800MM	800x	730x	250
56	1	2X15LT ELEKTRİK FİRİTOZ DOLAPLI-800MM	800x	730x	850
57	1	SETÜSTÜ GAZ İZGARADUZ KROM PLEYT-800MM	800x	730x	250
58	1	ADA TİP DAVLUMBAZ,304-2800X1400MM EXPORT	2500x	2000x	500
59	1	TAVA RAFI	350x	600x	30
61	1	EL YIKAMA EYİYESİ,DUVAR TIPI,DİZ KONTROLÜ	400x	400x	332
62	1	ÇALIŞMA TEZGAHI	2445x	800x	900
63	1	GN 1/1 - TEZGAH TİP BUZDOLABI - INOX ÜÇ KAPILI	1865x	700x	850
64	1	TEK EVVELİ ÇALIŞMA TEZGAHI	900x	700x	850
65	1	KÖMÜR ARABASI	450x	650x	660
66	1	KENDİNDEN DAVLUMBAZLI KÖMÜRLÜ İZGARA	1800x	500x	1500
67	1	ÇALIŞMA TEZGAHI	2300x	700x	1000
68	1	BİNE GALOS DOLABI	400x	150x	300
69	1	PIZZA FIRINI - 6H	1220x	620x	720
70	1	FIRIN ALT STANDI	1100x	800x	850
71	1	DUVAR DAVLUMBAZI,304-1600X1100MM EXPORT	1500x	1100x	500
3-BULASIKHANE					
80	1	BULASIK KABUL TEZGAHI	1600x	800x	1551
81	1	50 L SİS ÇÖP ARABASI-KAPAKLI	380x	427x	605
82	1	ÇALIŞMA TEZGAHI	1200x	800x	900
83	1	KAZAN YIK.MAK.GİRİŞ TEZGAHI.SOL.900MM	1000x	750x	850
84	1	SPREY DUSLU BATARYA 3/4 PREMIUM	800x	425x	1500
85	1	GYOTİN BULASIK MAKİNESİ,80 SEPİS	748x	755x	1549
86	1	DUVAR TİP FİLTRESİZ DAVLUMBAZ	1000x	1000x	500
87	1	BULASIK GİRİŞ-ÇIKIŞ TEZGAHI	1000x	750x	910
88	2	İSTİF RAFI	1830x	510x	1700
89	1	BULASIK TOPLAMA ARABASI	995x	695x	916
90	1	KAZAN YIKAMA EYİYESİ	1200x	800x	600
91	1	ÇALIŞMA TEZGAHI 900 MM	900x	800x	900
92	1	GN YIKAMA DUSLU TEZGAH TİP,SPREY ÜNİTELİ	300x	200x	1150
93	2	İSTİF RAFI	1370x	460x	1700
4-SERVİS ALANI					
110	2	SOGUK TEZGAH 280LT.2 KAPILI,SIRTILİHD	1400x	700x	850
111	1	6-AÇIK ATESLİ GAZLI OCAK-1200MM	1200x	730x	250
112	1	ONÜ AÇIK ALT DOLAP-1200MM	1200x	550x	600
113	1	DUVAR TİP FİLTRELİ DAVLUMBAZ	1600x	1000x	500
114	1	BY 10 DECORATIVE BAKKİ EVVELİ	5150x	800x	900
115	1	OTOMATİK DİLİMLEME MAKİNESİ-300 MM	760x	520x	590
116	1	GN 1/1 - TEZGAH TİP BUZDOLABI - INOX ÜÇ KAPILI	1865x	700x	850
117	1	ÇÖP ÜNİTESİ	600x	600x	850
118	2	DOLAPLI ARA RAFLI ÇALIŞMA TEZGAHI	1600x	600x	900
119	1	DUZ CAMLI SOĞUK TESHİR DOLABI	1600x	700x	1350
120	1	DUZ CAMLI SOĞUK TESHİR DOLABI	2400x	700x	1350
121	2	İSTİTİ LAMBA	240x	240x	216
123	3	TABAK TEZGAHI	1600x	700x	1000
124	1	DOLAPLI ARA RAFLI ÇALIŞMA TEZGAHI	1600x	700x	900
125	1	DOLAPLI ARA RAFLI ÇALIŞMA TEZGAHI	1600x	700x	900
126	1	RATIONAL FIRIN	0x	0x	0
127	1	FIRIN ALT STANDI	0x	0x	0
128	1	DUVAR TİP FİLTRESİZ DAVLUMBAZ	1000x	1000x	500
129	1	MAYALAMA ÜNİTESİ	0x	0x	0
130	1	DISPLAY ÜNİTESİ	2200x	800x	0
5-BAR					
135	2	İÇECEK BUZDOLABI 3 KAPILI	1380x	500x	910
136	1	KAHVE ÇEKMECELİ DOLAPLI ARA RAFLI ÇALIŞMA TEZGAHI	1600x	550x	900
137	1	FIL.KAHVE MAK.MANUEL,İDAM,2PLEYT	205x	360x	430
138	1	2-GRUPLU ESPRESSO KAHVE MAKİNESİ	817x	559x	570
139	1	KAHVE DEĞİRMENİ	220x	400x	620
140	1	KÖSE TEZGAHI	550x	600x	850
141	1	KİSİMİ DOLAPLI ARA RAFLI ÇALIŞMA TEZGAHI	1800x	600x	900
142	1	TEZGAH ALTI DONDURUCU,160LT	600x	600x	825
143	1	KORTİYEL ÜNİTESİ,BLENDER EYİVELİ,SBRELK RAFLI,ALTİ SOĞUK DOLAPLI	1200x	635x	850
144	1	BAR BLENDER	170x	188x	410
145	1	BUZ MAKİNESİ 42 KG/GÜN, HAVA SOĞUTMALI	500x	580x	820
146	1	BAR YIK.MAK.(XS)+DRENAJ P.DET.DİSP.30B/S	436x	495x	670
147	1	TEK EVVELİ ÇALIŞMA TEZGAHI	1600x	600x	850

AKKOZA

MUTFAK YERLEŞİM PLANI

DESİGN BY	MURAT ÖDÜL	DRAWİNG NO	DATE	SCALE
DRAWİNG BY	MURAT ÖDÜL	11072024	11/07/2024	1/50
CHECKED BY	MURAT ÖDÜL			

Merkez Mh. Günebakan Sk. No:24/B
Kâğıthane/İstanbul

\\._Desktop\MURAT LOGO.jpg